


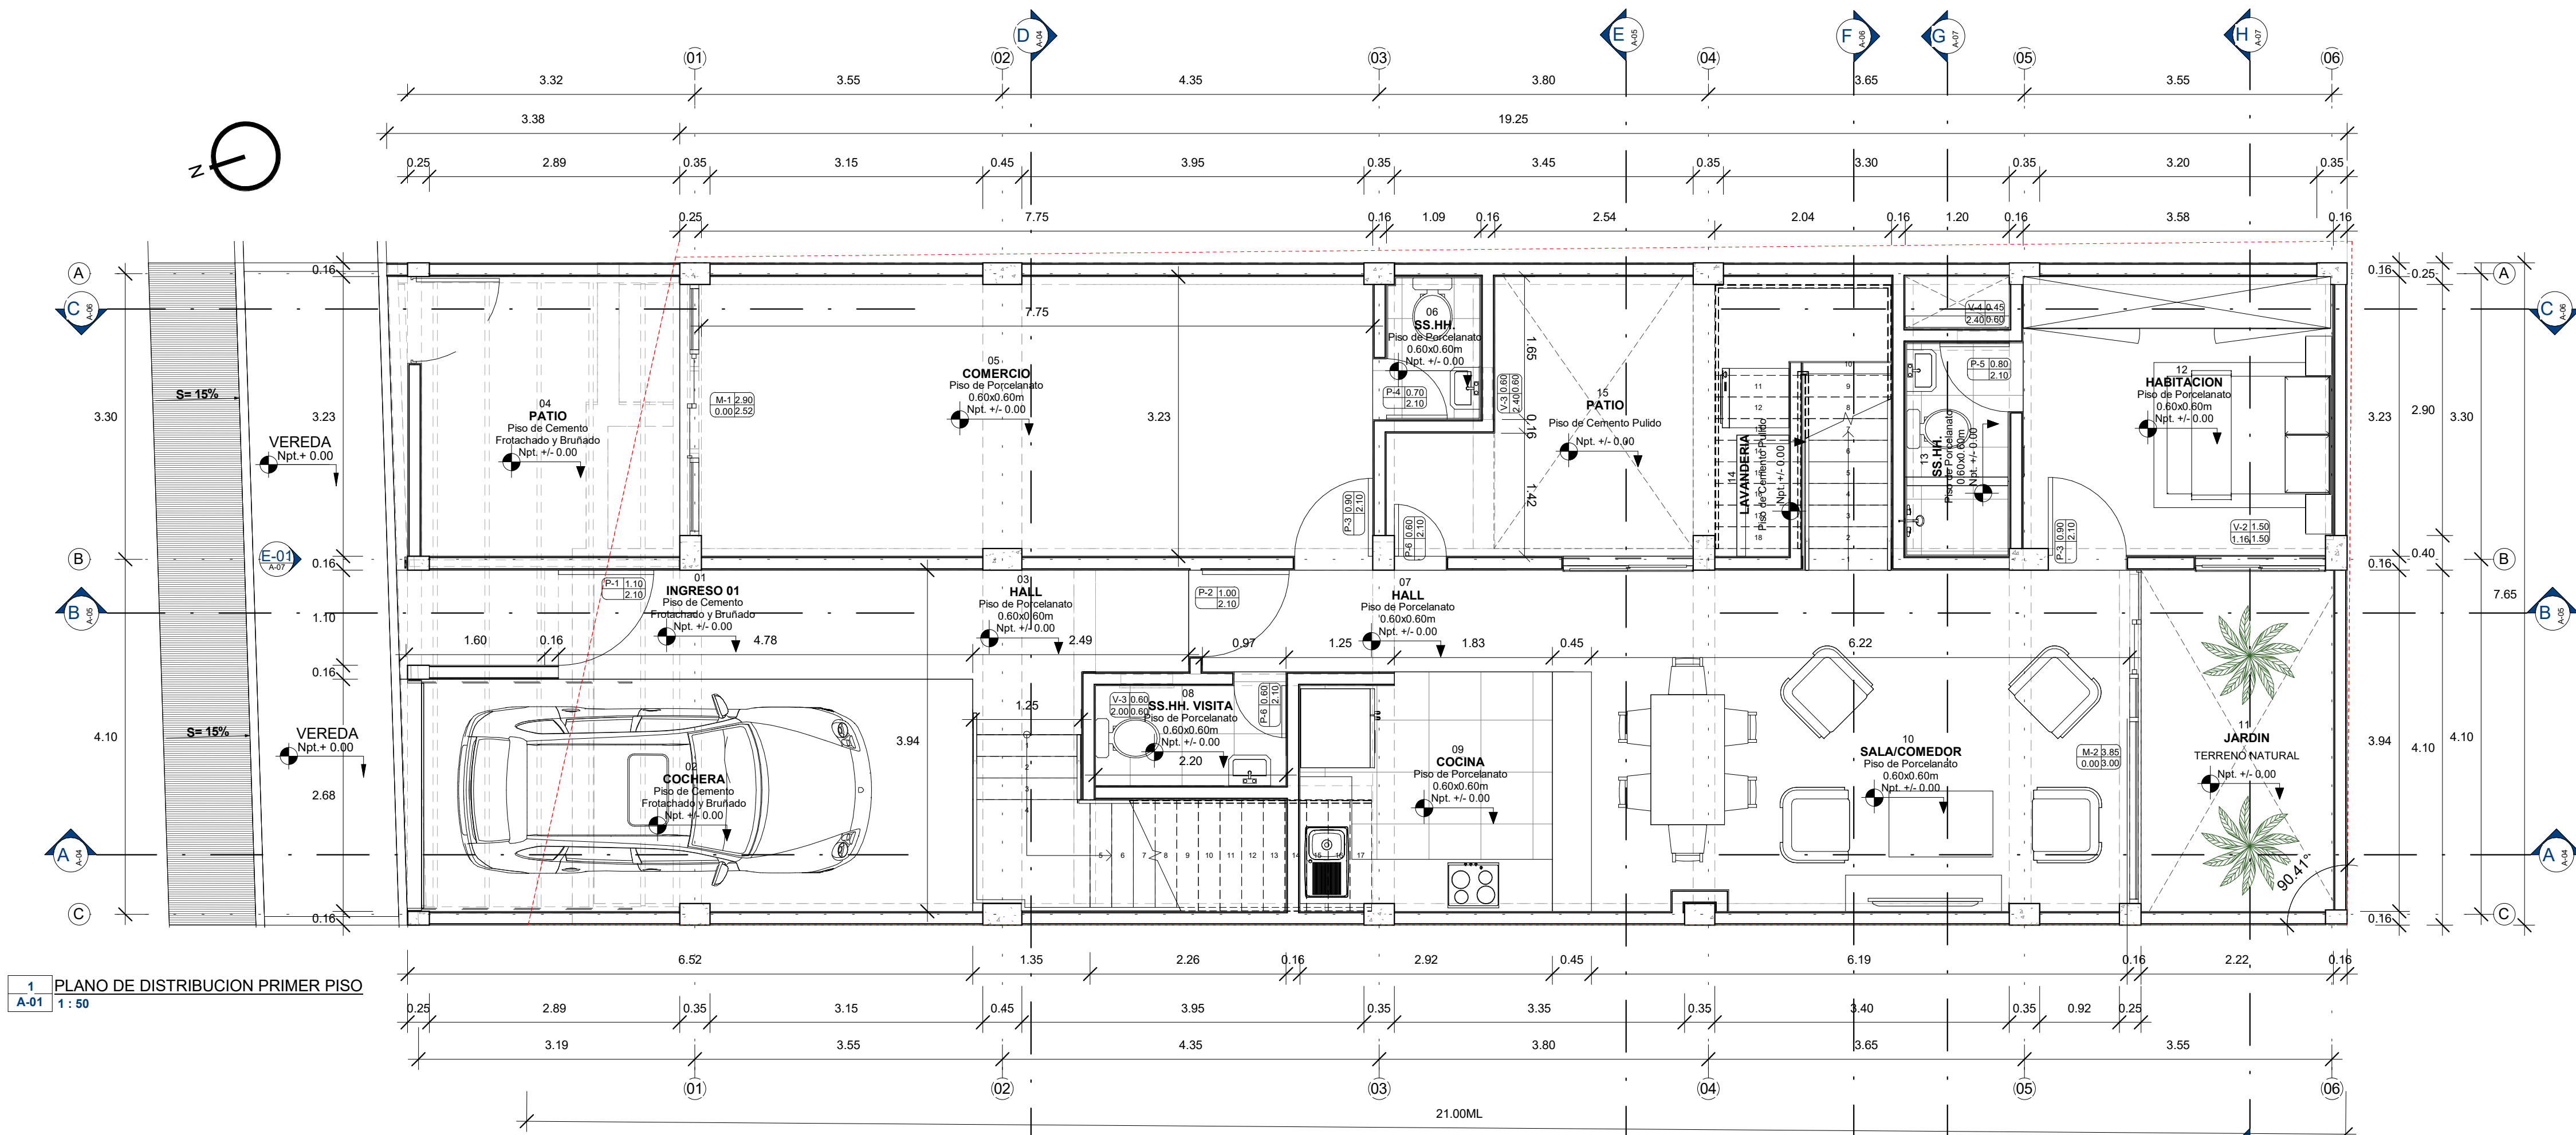


1 PLANO DE DISTRIBUCION PRIMER PISO
A-01 1:50

Tabla de planificación de áreas (Área Techada)	
Nombre	Área
Área 1er Piso	137.828
Área 2do Piso	132.519
Área 3er Piso	137.889
Área 4to Piso	137.922
Área Azotea	20.666
Total general: 5	566.624

CARPINTERIA METALICA - 1er y 2do Piso					
COD.	Largo	Alto	Aleitar	Área	Nivel
M-1	2.90	2.52	0.00	7.32	Npt. +/- 0.00
M-2	3.85	3.00	0.00	11.55	Npt. +/- 0.00
Npt. +/- 0.00: 2					
M-2	1.45	2.80	0.00	4.06	Npt.+3.25
M-3	1.45	2.80	0.00	4.06	Npt.+3.25
M-4	1.10	2.65	0.00	2.92	Npt.+3.25
Npt.+3.25: 3					
Total general: 5					

CUADRO DE VANOS PUERTAS -1er y 2do PISO				
COD.	Anchura	Altura	Total	Nivel
P-1	1.10	2.10	1	Npt. +/- 0.00
P-1: 1				
P-2	1.00	2.10	1	Npt. +/- 0.00
P-2: 1				
P-3	0.90	2.10	1	Npt. +/- 0.00
P-3	0.90	2.10	1	Npt. +/- 0.00
P-3: 2				
P-4	0.70	2.10	1	Npt. +/- 0.00
P-4: 1				
P-5	0.80	2.10	1	Npt. +/- 0.00
P-5: 1				
P-6	0.60	2.10	1	Npt. +/- 0.00
P-6	0.60	2.10	1	Npt. +/- 0.00
P-6: 2				
PM-2	2.60	2.10	1	Npt. +/- 0.00
PM-2: 1				
Npt. +/- 0.00: 9				
P-2	1.00	2.10	1	Npt.+3.25
P-2: 1				
P-3	0.90	2.10	1	Npt.+3.25
P-3	0.90	2.10	1	Npt.+3.25
P-3: 2				
P-3	0.90	2.10	1	Npt.+3.25
P-3	0.90	2.10	1	Npt.+3.25
P-3: 5				
P-4	0.70	2.10	1	Npt.+3.25
P-4	0.70	2.10	1	Npt.+3.25
P-4: 2				
P-4	0.70	2.10	1	Npt.+3.25
P-7	1	2.10	1	Npt.+3.25
Npt.+3.25: 11				


CUADRO DE VANOS VENTANA-1er y 2do PISO					
COD.	Aleitar	Anchura	Altura	Total	Nivel
V-2	1.16	1.50	1.50	1	Npt. +/- 0.00
V-2	1.35	1.50	1.50	1	Npt. +/- 0.00
V-2: 2					
V-3	2.00	0.60	0.60	1	Npt. +/- 0.00
V-3	2.40	0.60	0.60	1	Npt. +/- 0.00
V-3: 2					
V-4	2.40	0.60	0.45	1	Npt. +/- 0.00
V-4: 1					
V-1	0.90	1.10	1.50	1	Npt.+3.25
V-1: 1					
V-2	1.15	1.50	1.50	1	Npt.+3.25
V-2	1.15	1.50	1.50	1	Npt.+3.25
V-2: 3					
V-3	2.18	0.60	0.60	1	Npt.+3.25
V-3	2.15	0.60	0.60	1	Npt.+3.25
V-3	2.05	0.60	0.60	1	Npt.+3.25
V-3	2.20	0.60	0.60	1	Npt.+3.25
V-3: 4					
Npt.+3.25: 8					8
Total general: 13					13

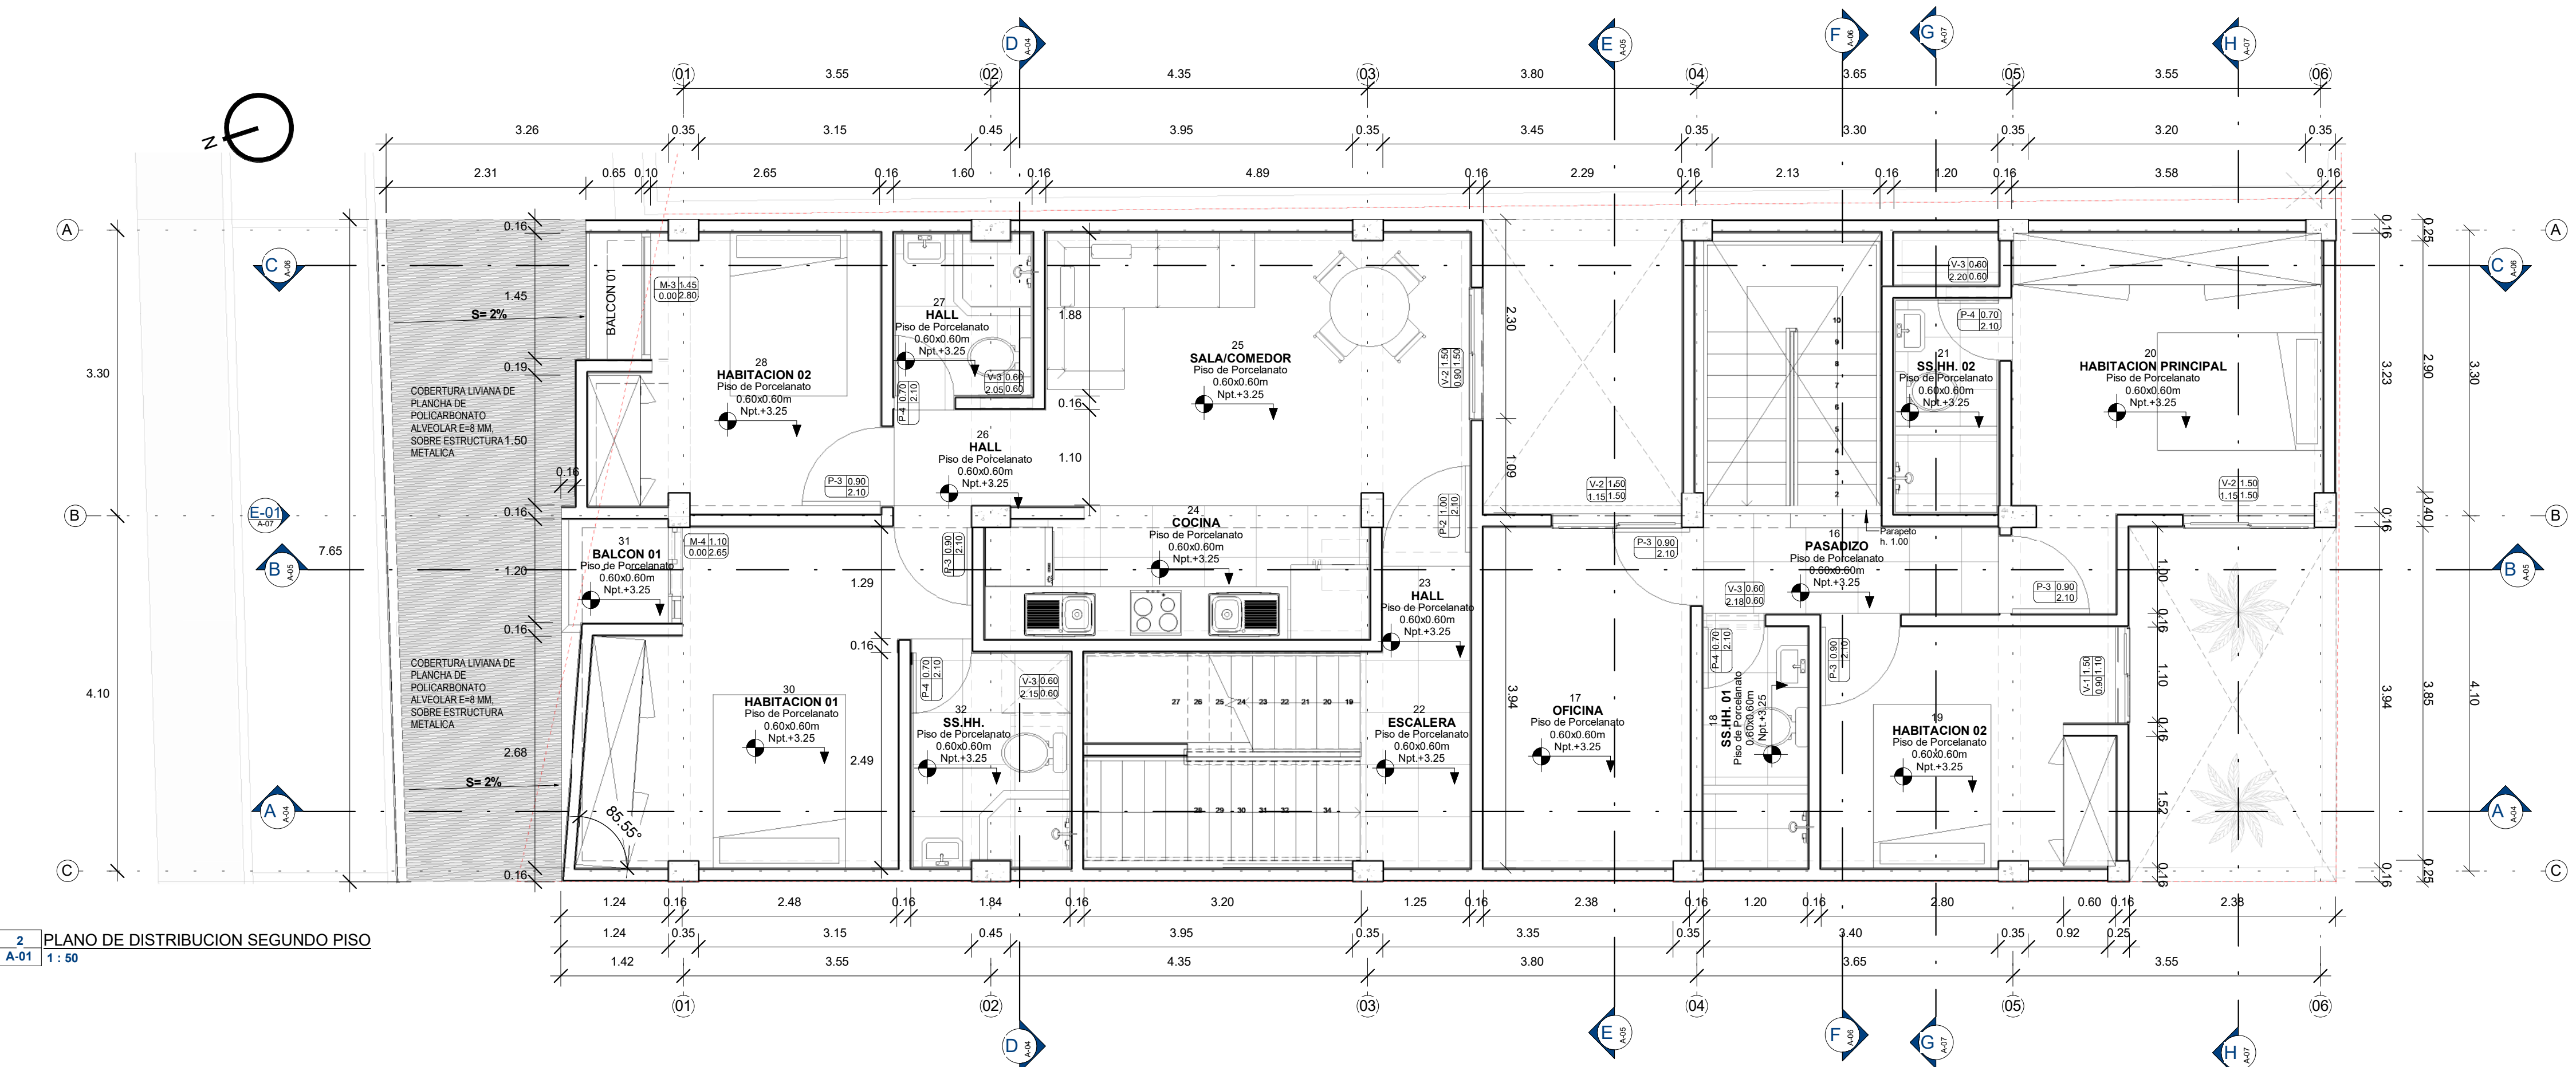


2 PLANO DE DISTRIBUCION SEGUNDO PISO
A-01 1:50

01_PRIMER Y SEGUNDO PISO				
N°	Nombre	Acabado del suelo	Área	Departamento
01	INGRESO 01	Piso de Cemento Frotado y Bruñado	6.11	AREA COMUN
02	COCHERA	Piso de Cemento Frotado y Bruñado	17.11	AREA COMUN
03	HALL	Piso de Porcelanato 0.60x0.60m	3.53	DUPLEX
04	PATIO	Piso de Cemento Frotado y Bruñado	10.09	AREA LIBRE
05	COMERCIO	Piso de Porcelanato 0.60x0.60m	25.16	DUPLEX
06	SS.HH.	Piso de Porcelanato 0.60x0.60m	1.86	DUPLEX
07	HALL	Piso de Porcelanato 0.60x0.60m	5.32	DUPLEX
08	SS.HH. VISITA	Piso de Porcelanato 0.60x0.60m	2.58	DUPLEX
09	COCINA	Piso de Porcelanato 0.60x0.60m	9.17	DUPLEX
10	SALA/COMEDOR	Piso de Porcelanato 0.60x0.60m	24.31	DUPLEX
11	JARDIN	TERRENO NATURAL	8.87	AREA LIBRE
12	HABITACION	Piso de Porcelanato 0.60x0.60m	11.63	DUPLEX
13	SS.HH.	Piso de Porcelanato 0.60x0.60m	3.04	DUPLEX
14	LAVANDERIA	Piso de Cemento Pulido	4.75	DUPLEX
15	PATIO	Piso de Cemento Pulido	9.29	DUPLEX
Npt. +/- 0.00: 15				
16	PASADIZO	Piso de Porcelanato 0.60x0.60m	3.56	DUPLEX
17	OFICINA	Piso de Porcelanato 0.60x0.60m	9.36	DUPLEX
18	SS.HH. 01	Piso de Porcelanato 0.60x0.60m	3.34	DUPLEX
19	HABITACION 02	Piso de Porcelanato 0.60x0.60m	9.32	DUPLEX
20	HABITACION PRINCIPAL	Piso de Porcelanato 0.60x0.60m	12.82	DUPLEX
21	SS.HH. 02	Piso de Porcelanato 0.60x0.60m	2.96	DUPLEX
22	ESCALERA	Piso de Porcelanato 0.60x0.60m	10.54	CIRCULACION VERTICAL
23	HALL	Piso de Porcelanato 0.60x0.60m	1.00	CIRCULACION HORIZONTAL
24	COCINA	Piso de Porcelanato 0.60x0.60m	6.59	DEPARTAMENTO 01
25	SALA/COMEDOR	Piso de Porcelanato 0.60x0.60m	15.82	DEPARTAMENTO 01
26	HALL	Piso de Porcelanato 0.60x0.60m	2.02	DEPARTAMENTO 01
27	HALL	Piso de Porcelanato 0.60x0.60m	2.97	DEPARTAMENTO 01
28	HABITACION 02	Piso de Porcelanato 0.60x0.60m	9.55	DEPARTAMENTO 01
29	BALCON 01	Piso de Porcelanato 0.60x0.60m	0.87	DEPARTAMENTO 01
30	HABITACION 01	Piso de Porcelanato 0.60x0.60m	13.85	DEPARTAMENTO 01
31	BALCON 01	Piso de Porcelanato 0.60x0.60m	1.52	DEPARTAMENTO 01
32	SS.HH.	Piso de Porcelanato 0.60x0.60m	4.54	DEPARTAMENTO 01
Npt.+3.25: 17				110.64
Total general: 32				253.46

EDIFICIO MULTIFAMILIAR			
PROYECTO: VIVIENDA MULTIFAMILIAR			
PLANO: PLANO DE DISTRIBUCION PRIMER Y SEGUNDO PISO	FECHA: JULIO-2021	DIBUJO Y MODELADO BIM:	
ESPECIALIDAD: ARQUITECTURA	ESC: 1:50		
DISEÑO: NELSON DAZA DONAIRES	PLANO:	A-01	
UBICACION: Jr. Libertad N° 333, barrio de Zaragoza			
Direto: MOYOBA	Proyecto: MOYOBA	Región: SAN MARTIN	Nelson Daza Donaires

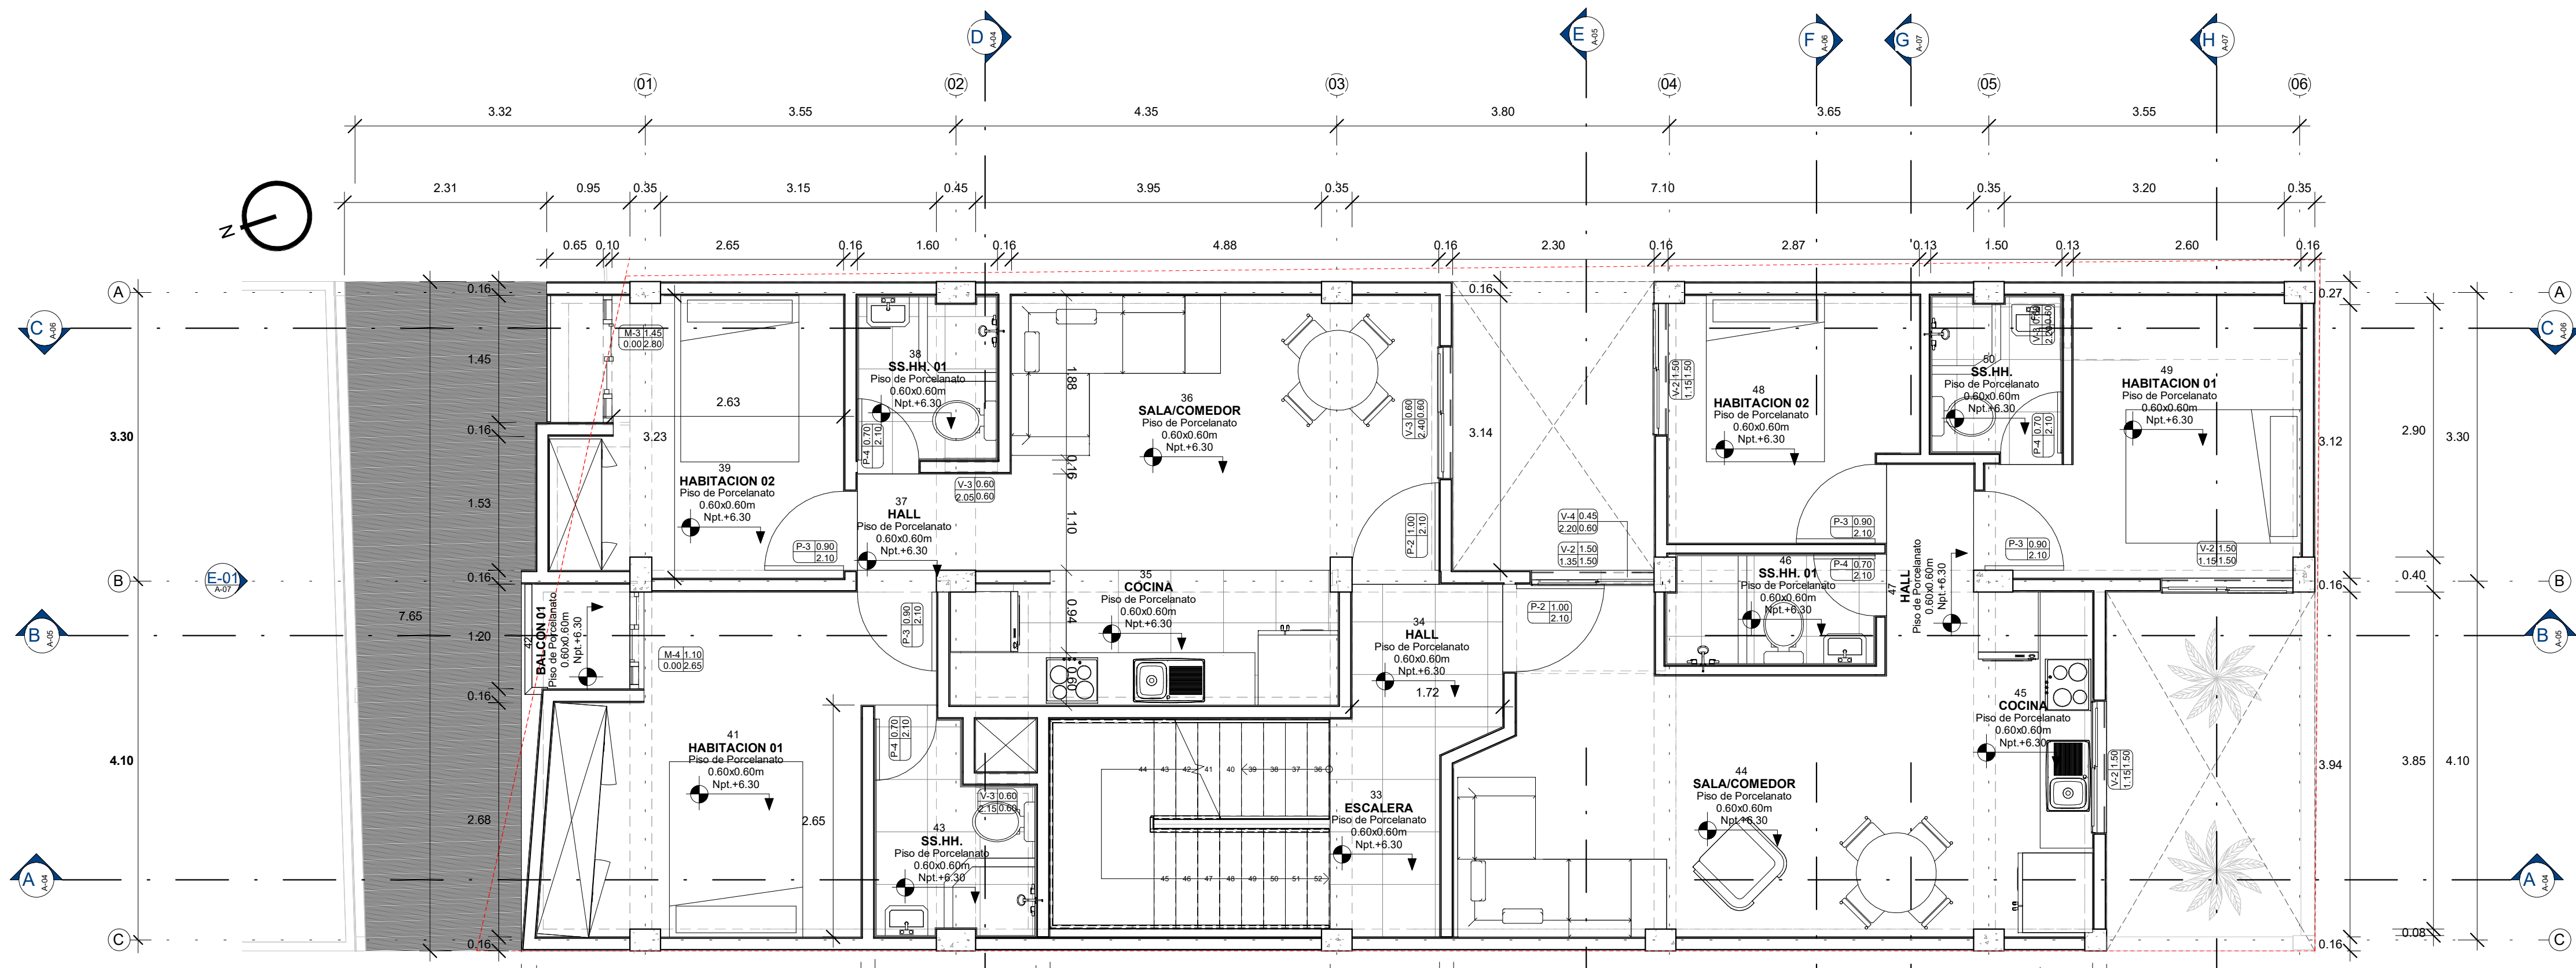

1 PLANO DE DISTRIBUCION TERCER PISO
A-02 1:50

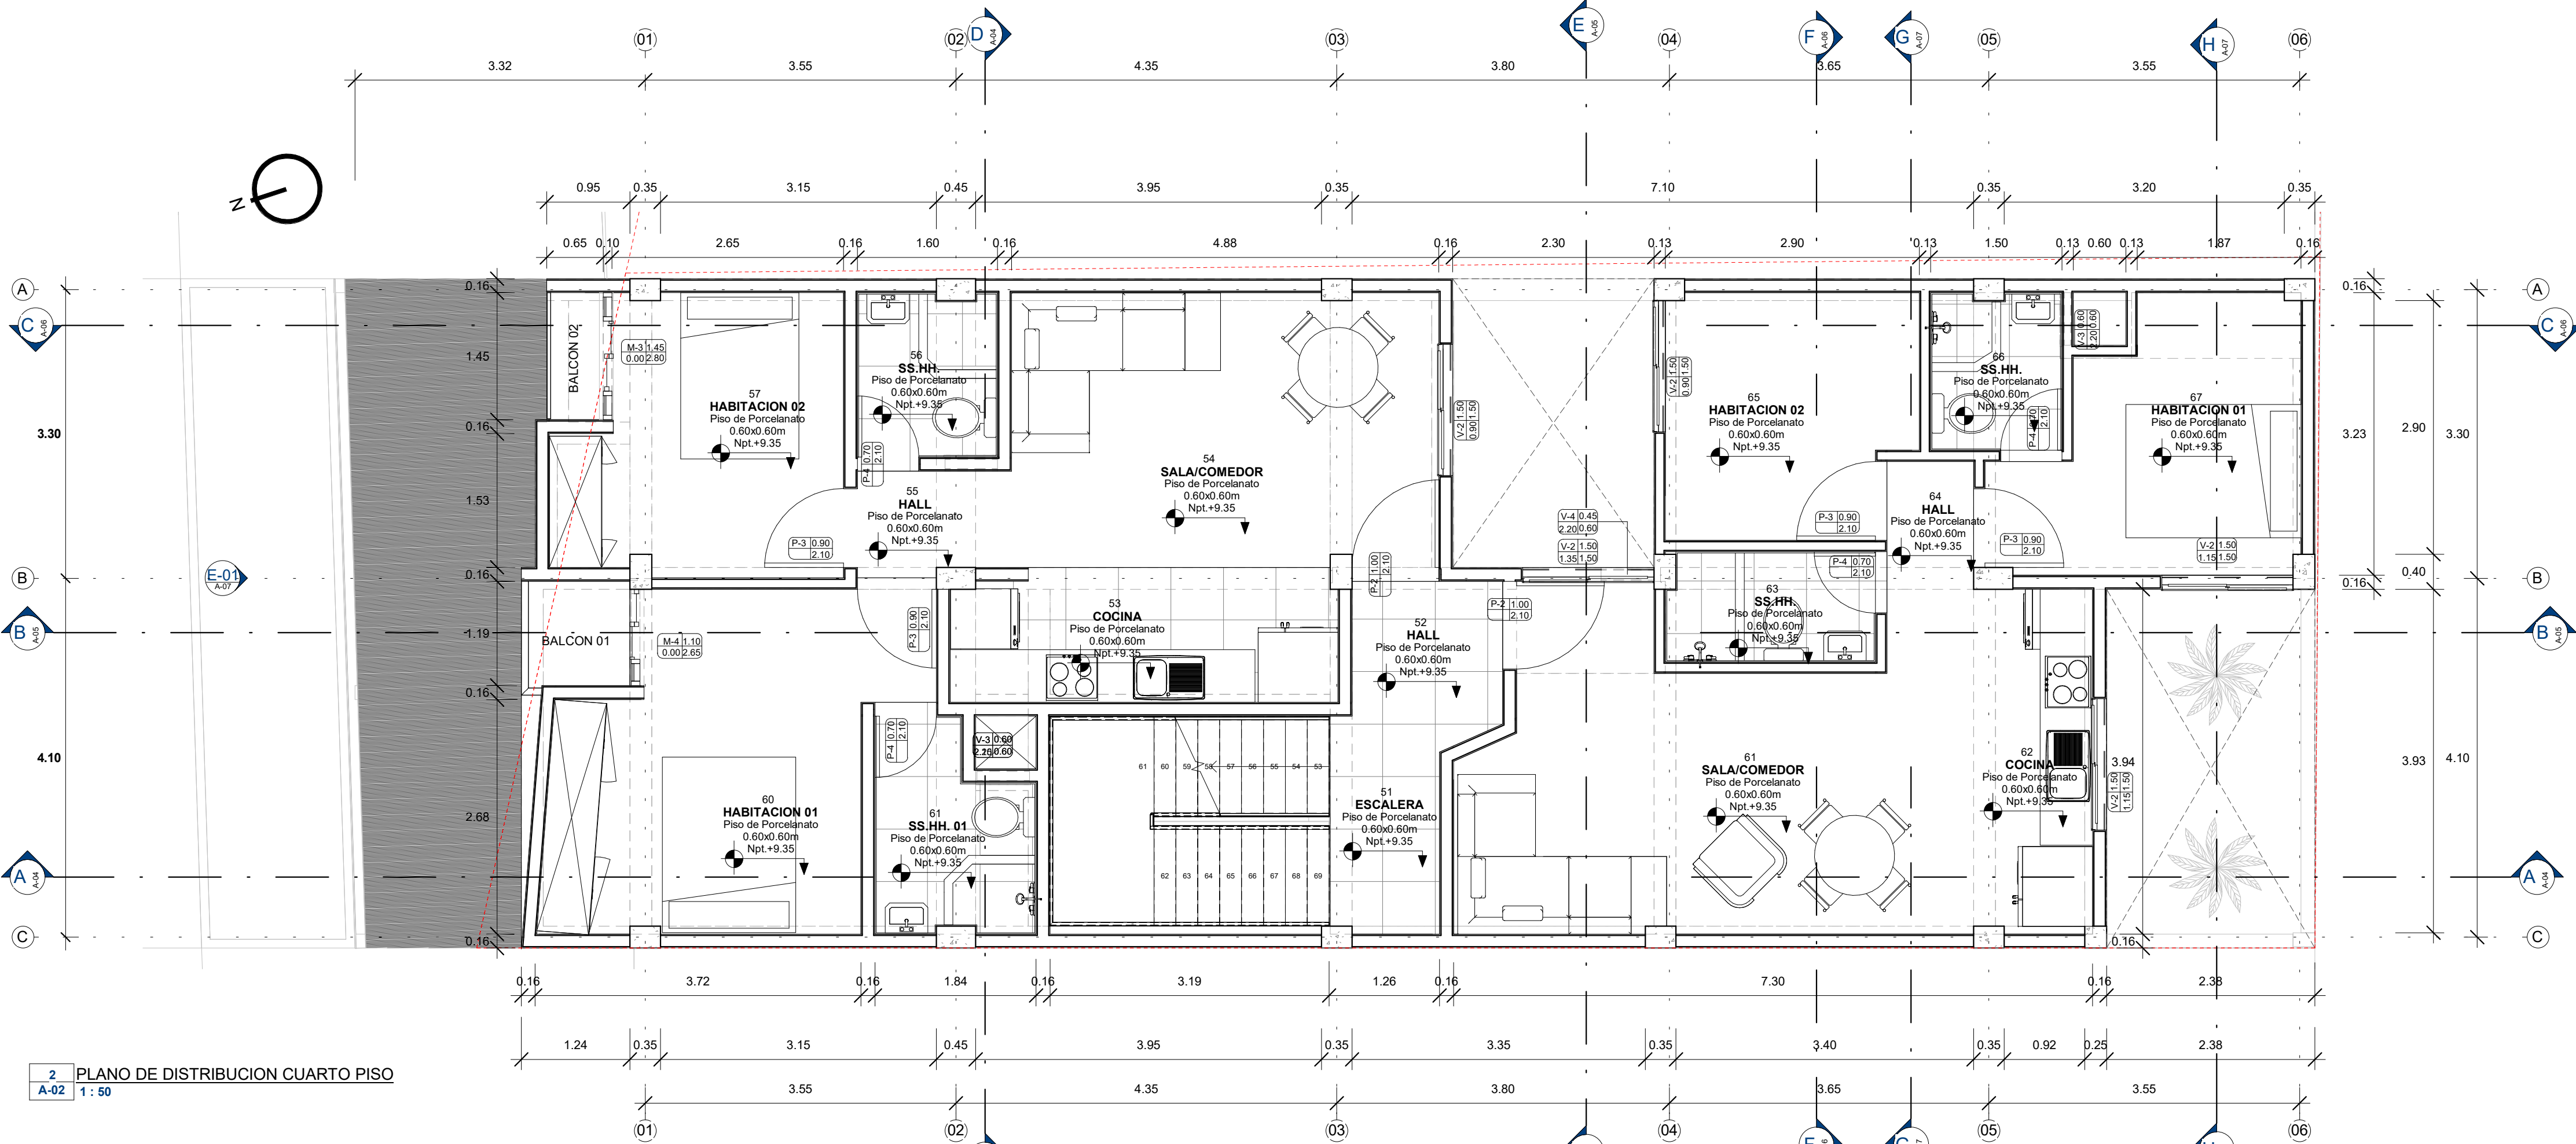

2 PLANO DE DISTRIBUCION CUARTO PISO
A-02 1:50

02_TERCER Y CUARTO PISO					
Nº	Nivel	Nombre	Acabado del suelo	Área	Departamento
33	Npt.+6.30	ESCALERA	Piso de Porcelanato 0.60x0.60m	11.19	CIRCULACION VERTICAL
34	Npt.+6.30	HALL	Piso de Porcelanato 0.60x0.60m	2.65	CIRCULACION HORIZONTAL
35	Npt.+6.30	COCINA	Piso de Porcelanato 0.60x0.60m	6.59	DEPARTAMENTO 02
36	Npt.+6.30	SALA/COMEDOR	Piso de Porcelanato 0.60x0.60m	15.70	DEPARTAMENTO 02
37	Npt.+6.30	HALL	Piso de Porcelanato 0.60x0.60m	1.57	DEPARTAMENTO 02
38	Npt.+6.30	SS.HH. 01	Piso de Porcelanato 0.60x0.60m	2.97	DEPARTAMENTO 02
39	Npt.+6.30	HABITACION 02	Piso de Porcelanato 0.60x0.60m	9.50	DEPARTAMENTO 02
40	Npt.+6.30	BALCON 01	Piso de Porcelanato 0.60x0.60m	0.87	DEPARTAMENTO 02
41	Npt.+6.30	HABITACION 01	Piso de Porcelanato 0.60x0.60m	13.85	DEPARTAMENTO 02
42	Npt.+6.30	BALCON 01	Piso de Porcelanato 0.60x0.60m	1.51	DEPARTAMENTO 02
43	Npt.+6.30	SS.HH.	Piso de Porcelanato 0.60x0.60m	3.89	DEPARTAMENTO 02
44	Npt.+6.30	SALA/COMEDOR	Piso de Porcelanato 0.60x0.60m	18.71	DEPARTAMENTO 03
45	Npt.+6.30	COCINA	Piso de Porcelanato 0.60x0.60m	5.32	DEPARTAMENTO 03
46	Npt.+6.30	SS.HH. 01	Piso de Porcelanato 0.60x0.60m	2.97	DEPARTAMENTO 03
47	Npt.+6.30	HALL	Piso de Porcelanato 0.60x0.60m	2.41	DEPARTAMENTO 03
48	Npt.+6.30	HABITACION 02	Piso de Porcelanato 0.60x0.60m	7.58	DEPARTAMENTO 03
49	Npt.+6.30	HABITACION 01	Piso de Porcelanato 0.60x0.60m	9.64	DEPARTAMENTO 03
50	Npt.+6.30	SS.HH.	Piso de Porcelanato 0.60x0.60m	2.67	DEPARTAMENTO 03
Npt.+6.30: 18				119.80	
51	Npt.+9.35	ESCALERA	Piso de Porcelanato 0.60x0.60m	11.19	CIRCULACION VERTICAL
52	Npt.+9.35	HALL	Piso de Porcelanato 0.60x0.60m	2.65	DEPARTAMENTO 05
53	Npt.+9.35	COCINA	Piso de Porcelanato 0.60x0.60m	6.63	DEPARTAMENTO 05
54	Npt.+9.35	SALA/COMEDOR	Piso de Porcelanato 0.60x0.60m	15.70	DEPARTAMENTO 04
55	Npt.+9.35	HALL	Piso de Porcelanato 0.60x0.60m	1.59	DEPARTAMENTO 04
56	Npt.+9.35	SS.HH.	Piso de Porcelanato 0.60x0.60m	2.97	DEPARTAMENTO 04
57	Npt.+9.35	HABITACION 02	Piso de Porcelanato 0.60x0.60m	9.57	DEPARTAMENTO 04
58	Npt.+9.35	BALCON 02	Piso de Porcelanato 0.60x0.60m	0.87	DEPARTAMENTO 04
59	Npt.+9.35	BALCON 01	Piso de Porcelanato 0.60x0.60m	1.54	DEPARTAMENTO 04
60	Npt.+9.35	HABITACION 01	Piso de Porcelanato 0.60x0.60m	13.86	DEPARTAMENTO 04
61	Npt.+9.35	SS.HH. 01	Piso de Porcelanato 0.60x0.60m	3.89	DEPARTAMENTO 04
61	Npt.+9.35	SALA/COMEDOR	Piso de Porcelanato 0.60x0.60m	19.66	DEPARTAMENTO 05
62	Npt.+9.35	COCINA	Piso de Porcelanato 0.60x0.60m	5.32	DEPARTAMENTO 05
63	Npt.+9.35	SS.HH.	Piso de Porcelanato 0.60x0.60m	2.97	DEPARTAMENTO 05
64	Npt.+9.35	HALL	Piso de Porcelanato 0.60x0.60m	1.44	DEPARTAMENTO 05
65	Npt.+9.35	HABITACION 02	Piso de Porcelanato 0.60x0.60m	7.67	DEPARTAMENTO 05
66	Npt.+9.35	SS.HH.	Piso de Porcelanato 0.60x0.60m	2.67	DEPARTAMENTO 05
67	Npt.+9.35	HABITACION 01	Piso de Porcelanato 0.60x0.60m	9.11	DEPARTAMENTO 05
Npt.+9.35: 18				119.31	
68	Npt.+12.40	AZOTEA	Piso de Cemento Pulido	109.51	AREA COMUN
Npt.+12.40: 1				109.51	
69	Npt.+14.80	MEZZANINE	--	18.89	AREA COMUN
Npt.+14.80: 1				18.89	
Total general: 38				367.30	

CUADRO DE VANOS VENTANA-3er y 4to PISO					
COD.	Alfeizar	Anchura	Altura	Total	Nivel
V-2	1.15	1.50	1.50	1	Npt.+6.30
V-2	0.90	1.50	1.50	1	Npt.+6.30
V-2	1.15	1.50	1.50	1	Npt.+6.30
V-2	1.15	1.50	1.50	1	Npt.+6.30
V-2	0.60	1.50	1.50	1	Npt.+6.30
V-2: 5					5
V-3	2.05	0.60	0.60	1	Npt.+6.30
V-3	2.20	0.60	0.60	1	Npt.+6.30
V-3	2.20	0.60	0.60	1	Npt.+6.30
V-3: 3					3
V-4	2.20	0.60	0.45	1	Npt.+6.30
V-4: 1					1
Npt.+6.30: 9					9
V-2	1.15	1.50	1.50	1	Npt.+9.35
V-2	0.90	1.50	1.50	1	Npt.+9.35
V-2	1.15	1.50	1.50	1	Npt.+9.35
V-2	0.90	1.50	1.50	1	Npt.+9.35
V-2	0.60	1.50	1.50	1	Npt.+9.35
V-2: 5					5
V-3	2.20	0.60	0.60	1	Npt.+9.35
V-3	2.05	0.60	0.60	1	Npt.+9.35
V-3	2.20	0.60	0.60	1	Npt.+9.35
V-3: 3					3
V-4	2.20	0.60	0.45	1	Npt.+9.35
V-4: 1					1
Npt.+9.35: 9					9
Total general: 18					18

CUADRO DE VANOS PUERTAS -3er y 4to PISO					
COD.	Anchura	Altura	Total	Nivel	
P-2	1.00	2.10	1	Npt.+6.30	
P-2	1.00	2.10	1	Npt.+6.30	
P-2: 2					2
P-3	0.90	2.10	1	Npt.+6.30	
P-3	0.90	2.10	1	Npt.+6.30	
P-3	0.90	2.10	1	Npt.+6.30	
P-3: 3					3
P-4	0.70	2.10	1	Npt.+6.30	
P-4	0.70	2.10	1	Npt.+6.30	
P-4	0.70	2.10	1	Npt.+6.30	
P-4: 3					3
P-7	0.80	2.10	1	Npt.+6.30	
P-7	0.80	2.10	1	Npt.+6.30	
P-7: 2					2
Npt.+6.30: 12					12
P-2	1.00	2.10	1	Npt.+9.35	
P-2	1.00	2.10	1	Npt.+9.35	
P-2: 2					2
P-3	0.90	2.10	1	Npt.+9.35	
P-3	0.90	2.10	1	Npt.+9.35	
P-3	0.90	2.10	1	Npt.+9.35	
P-3: 3					3
P-4	0.70	2.10	1	Npt.+9.35	
P-4	0.70	2.10	1	Npt.+9.35	
P-4	0.70	2.10	1	Npt.+9.35	
P-4: 3					3
P-7	0.80	2.10	1	Npt.+9.35	
P-7	0.80	2.10	1	Npt.+9.35	
P-7: 2					2
Npt.+9.35: 12					12

CARPINTERIA METALICA - 3er y 4to Piso					
COD.	Largo	Alto	Alfeizar	Área	Nivel
M-3	1.45	2.80	0.00	4.06	Npt.+6.30
M-3	1.45	2.80	0.00	4.06	Npt.+9.35
0.00: 2					2
M-4	1.10	2.65	0.00	2.92	Npt.+6.30
M-4	1.10	2.65	0.00	2.92	Npt.+9.35
0.00: 2					2
Total general: 4					4

EDIFICIO MULTIFAMILIAR

PROYECTO: VIVIENDA MULTIFAMILIAR

PLANO: PLANO DE DISTRIBUCION TERCER Y CUARTO PISO

ESPECIALIDAD: ARQUITECTURA

DISEÑO: NELSON DAZA DONAIRES

UBICACION: Jr. Libertad N° 333, barrio de Zaragoza


FECHA: JULIO-2021

ESC: 1:50

PLANO:



DIBUJO Y MODELADO BIM: A-02

Nelson Daza Donaires

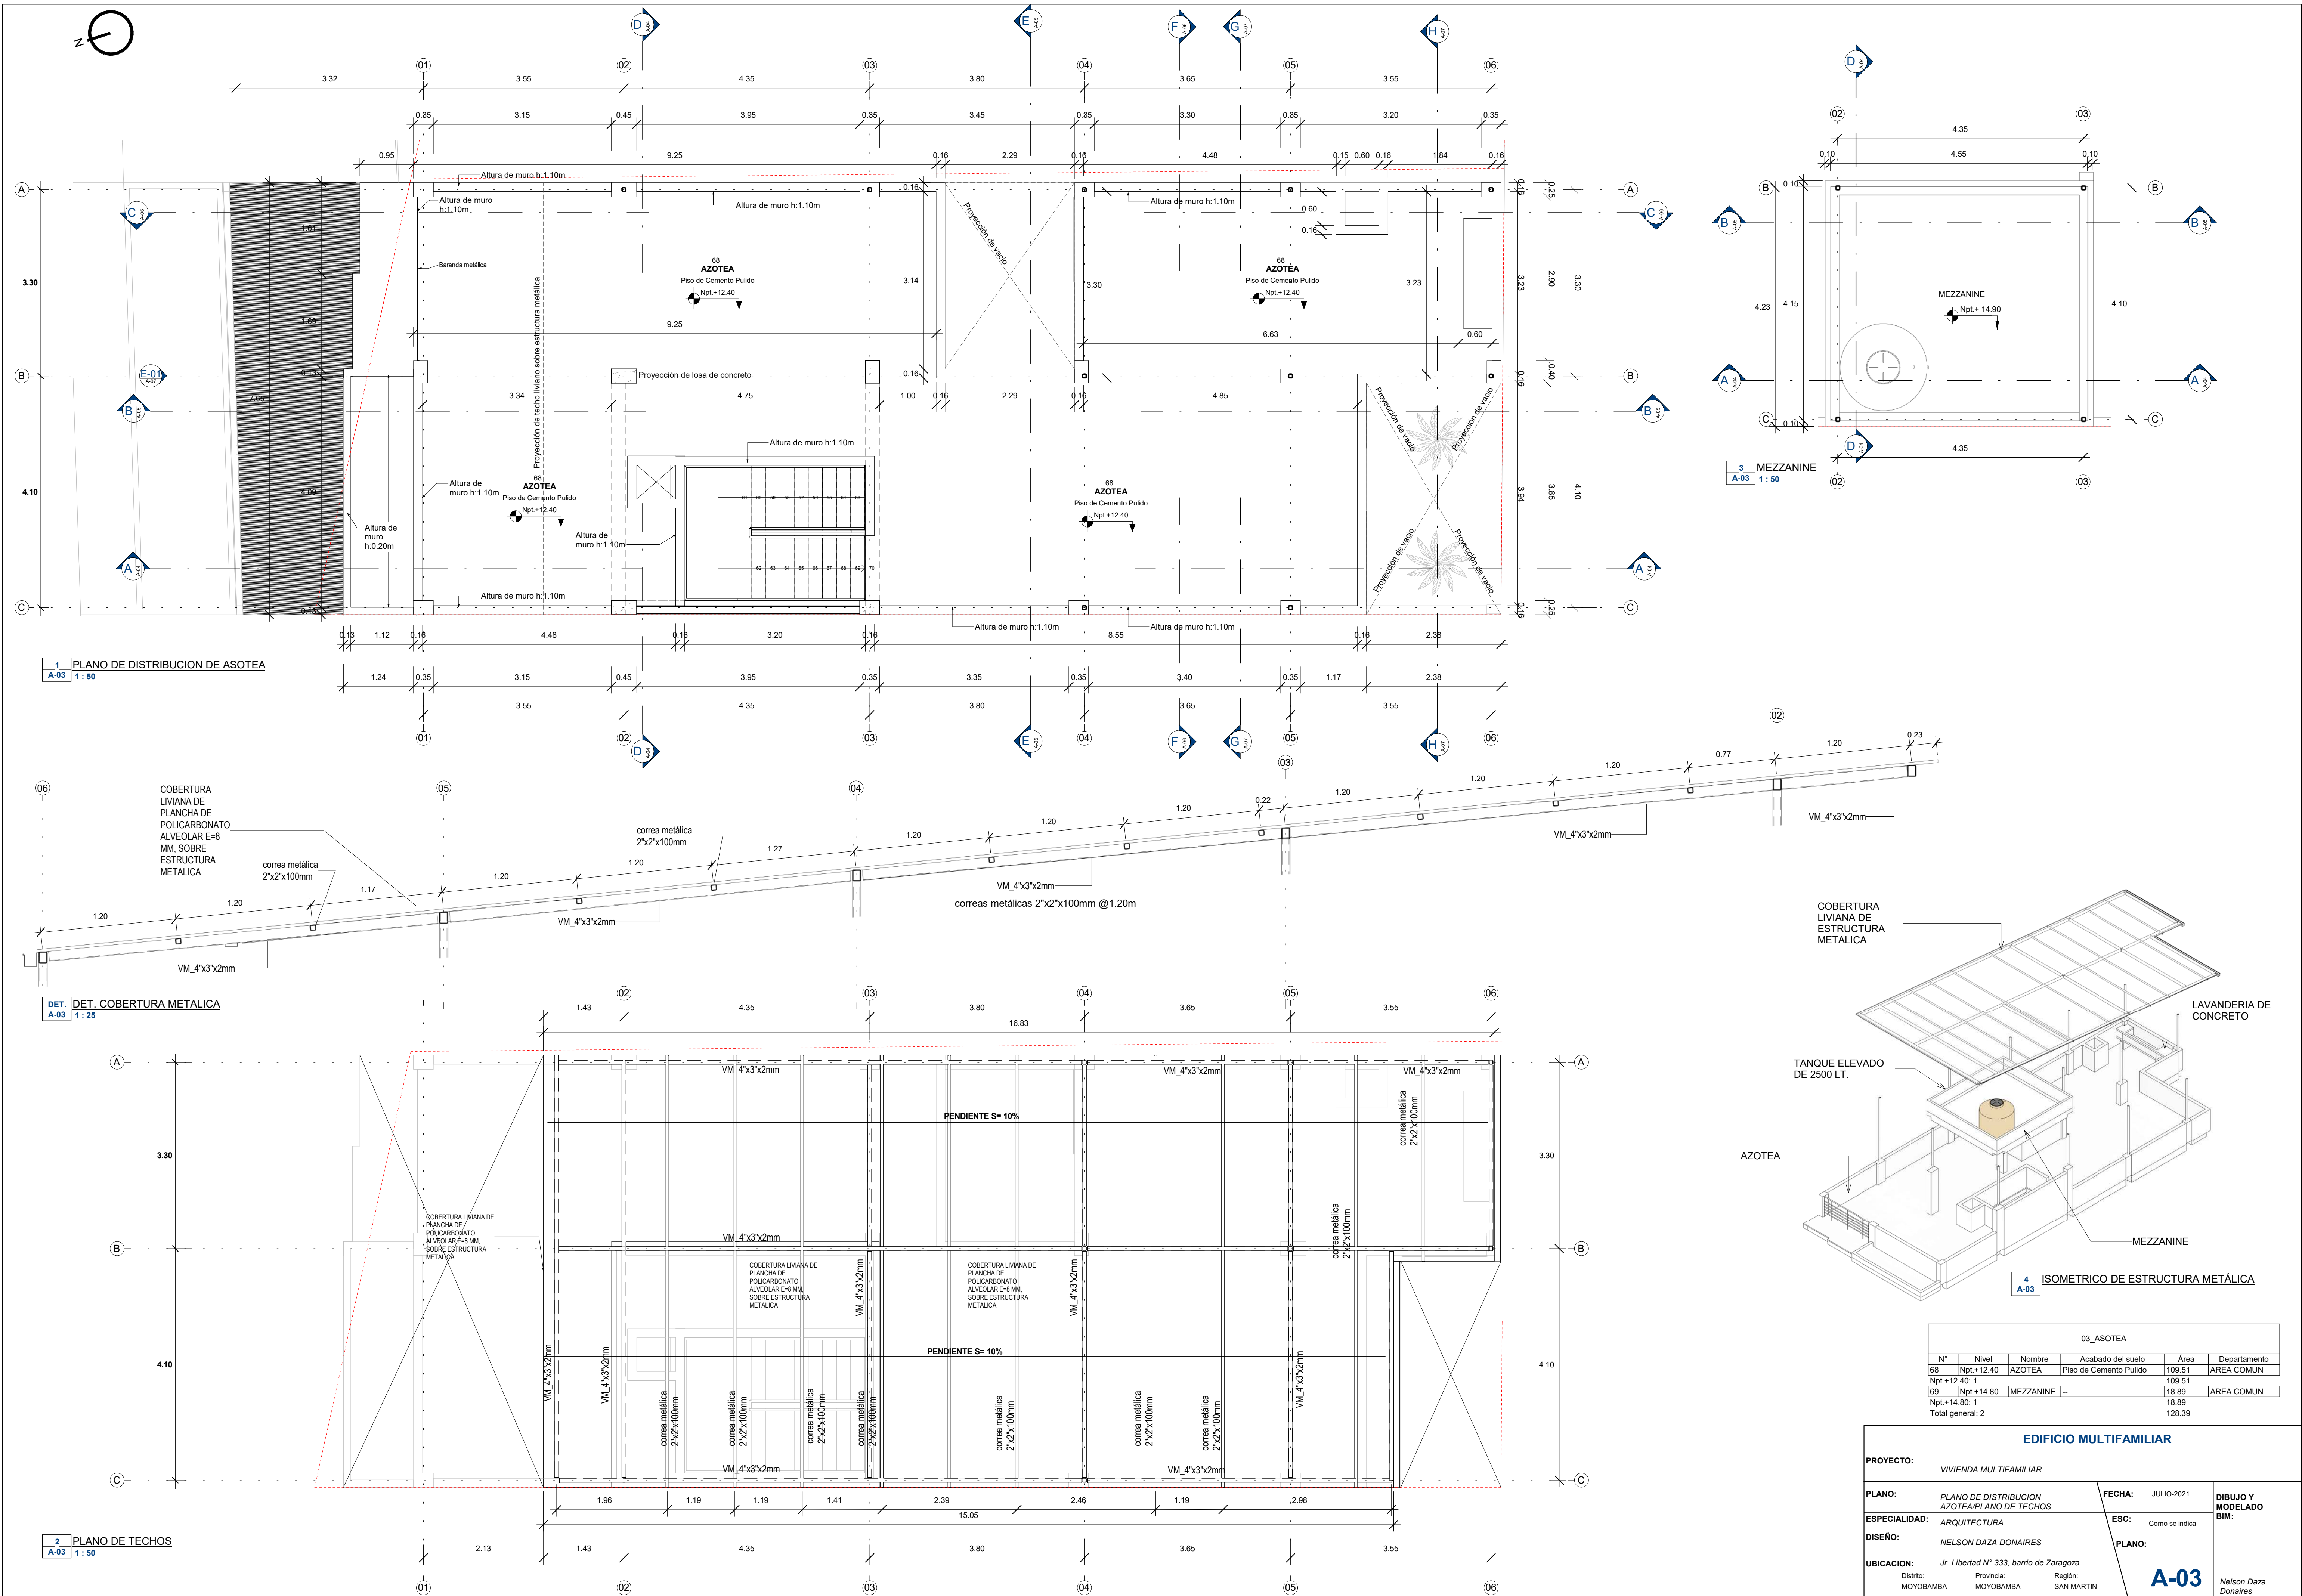


03_AZOTEA				
N°	Nivel	Nombre	Acabado del suelo	Área
68	Npt.+12.40	AZOTEA	Piso de Cemento Pulido	109.51
Npt.+12.40: 1				109.51
69	Npt.+14.80	MEZZANINE	--	18.89
Npt.+14.80: 1				18.89
Total general: 2				128.39

EDIFICIO MULTIFAMILIAR			
PROYECTO: VIVIENDA MULTIFAMILIAR			
PLANO:	PLANO DE DISTRIBUCION AZOTEA/PLANO DE TECHOS	FECHA:	JULIO-2021
ESPECIALIDAD:	ARQUITECTURA	ESC:	Como se indica
DISEÑO:	NELSON DAZA DONAIRES	PLANO:	
UBICACION:	Jr. Libertad N° 333, barrio de Zaragoza		
Distrito: MOYOBAMBA		Provincia: MOYOBAMBA	Región: SAN MARTIN
			A-03
			Nelson Daza Donaires

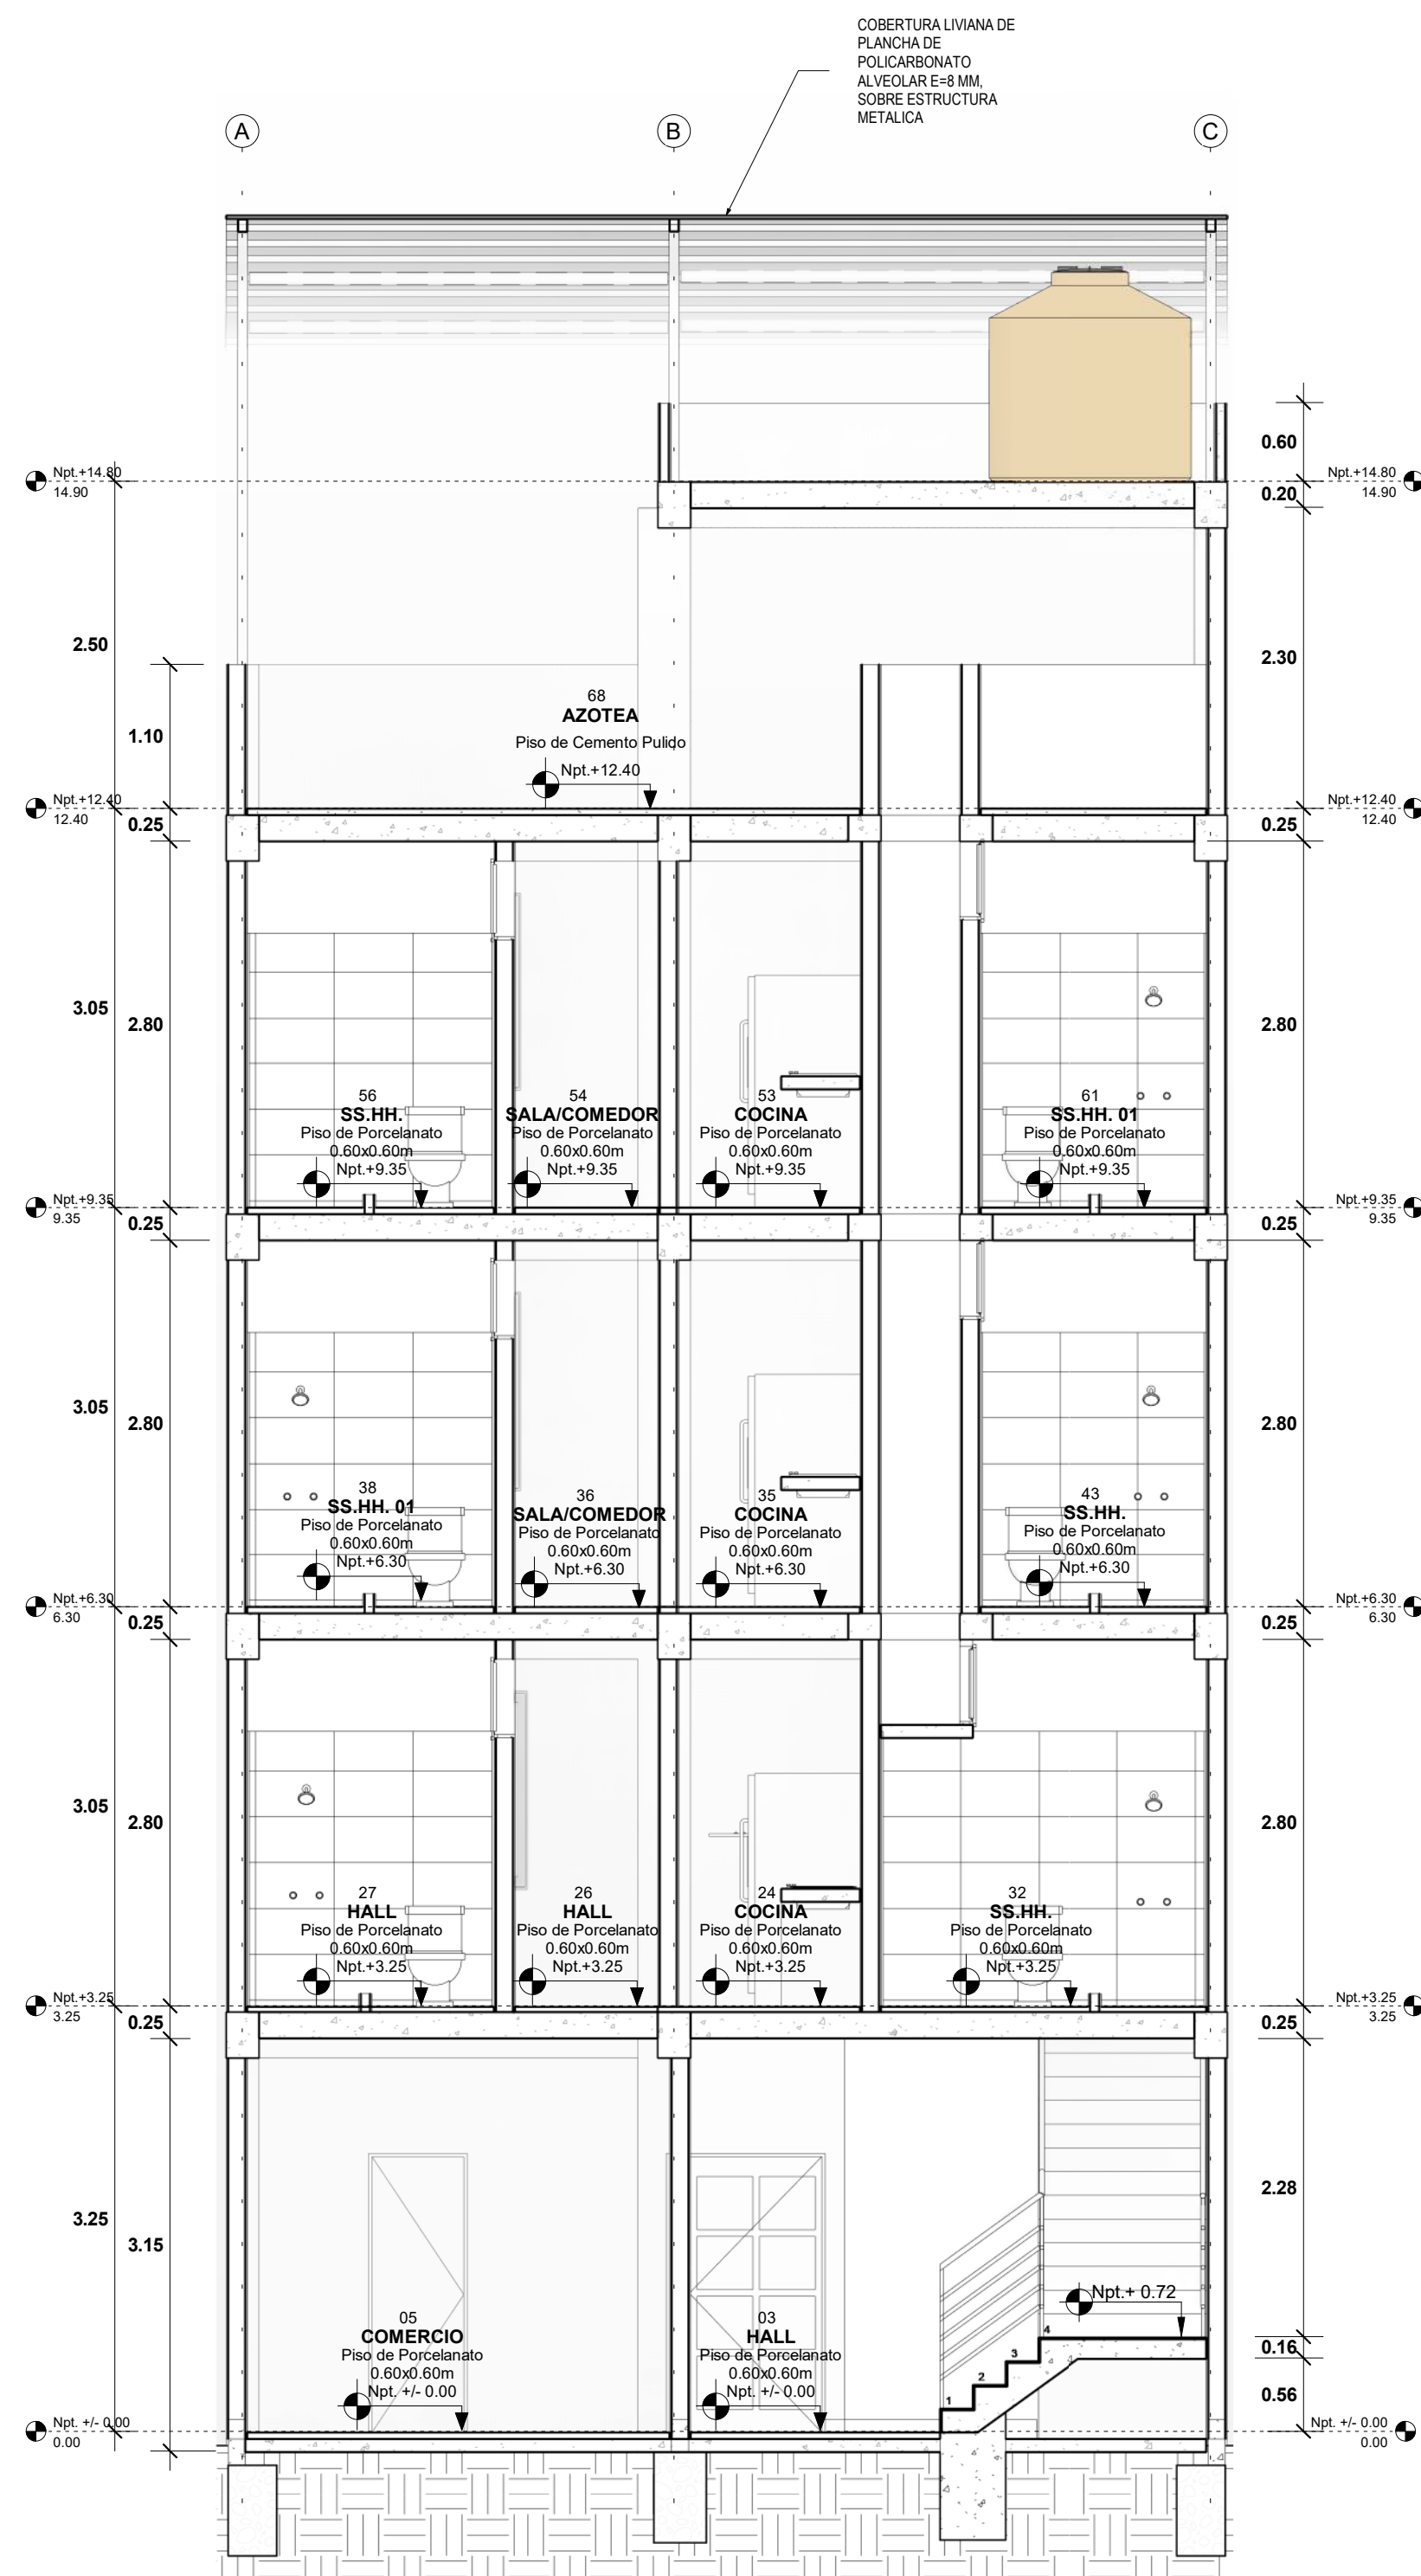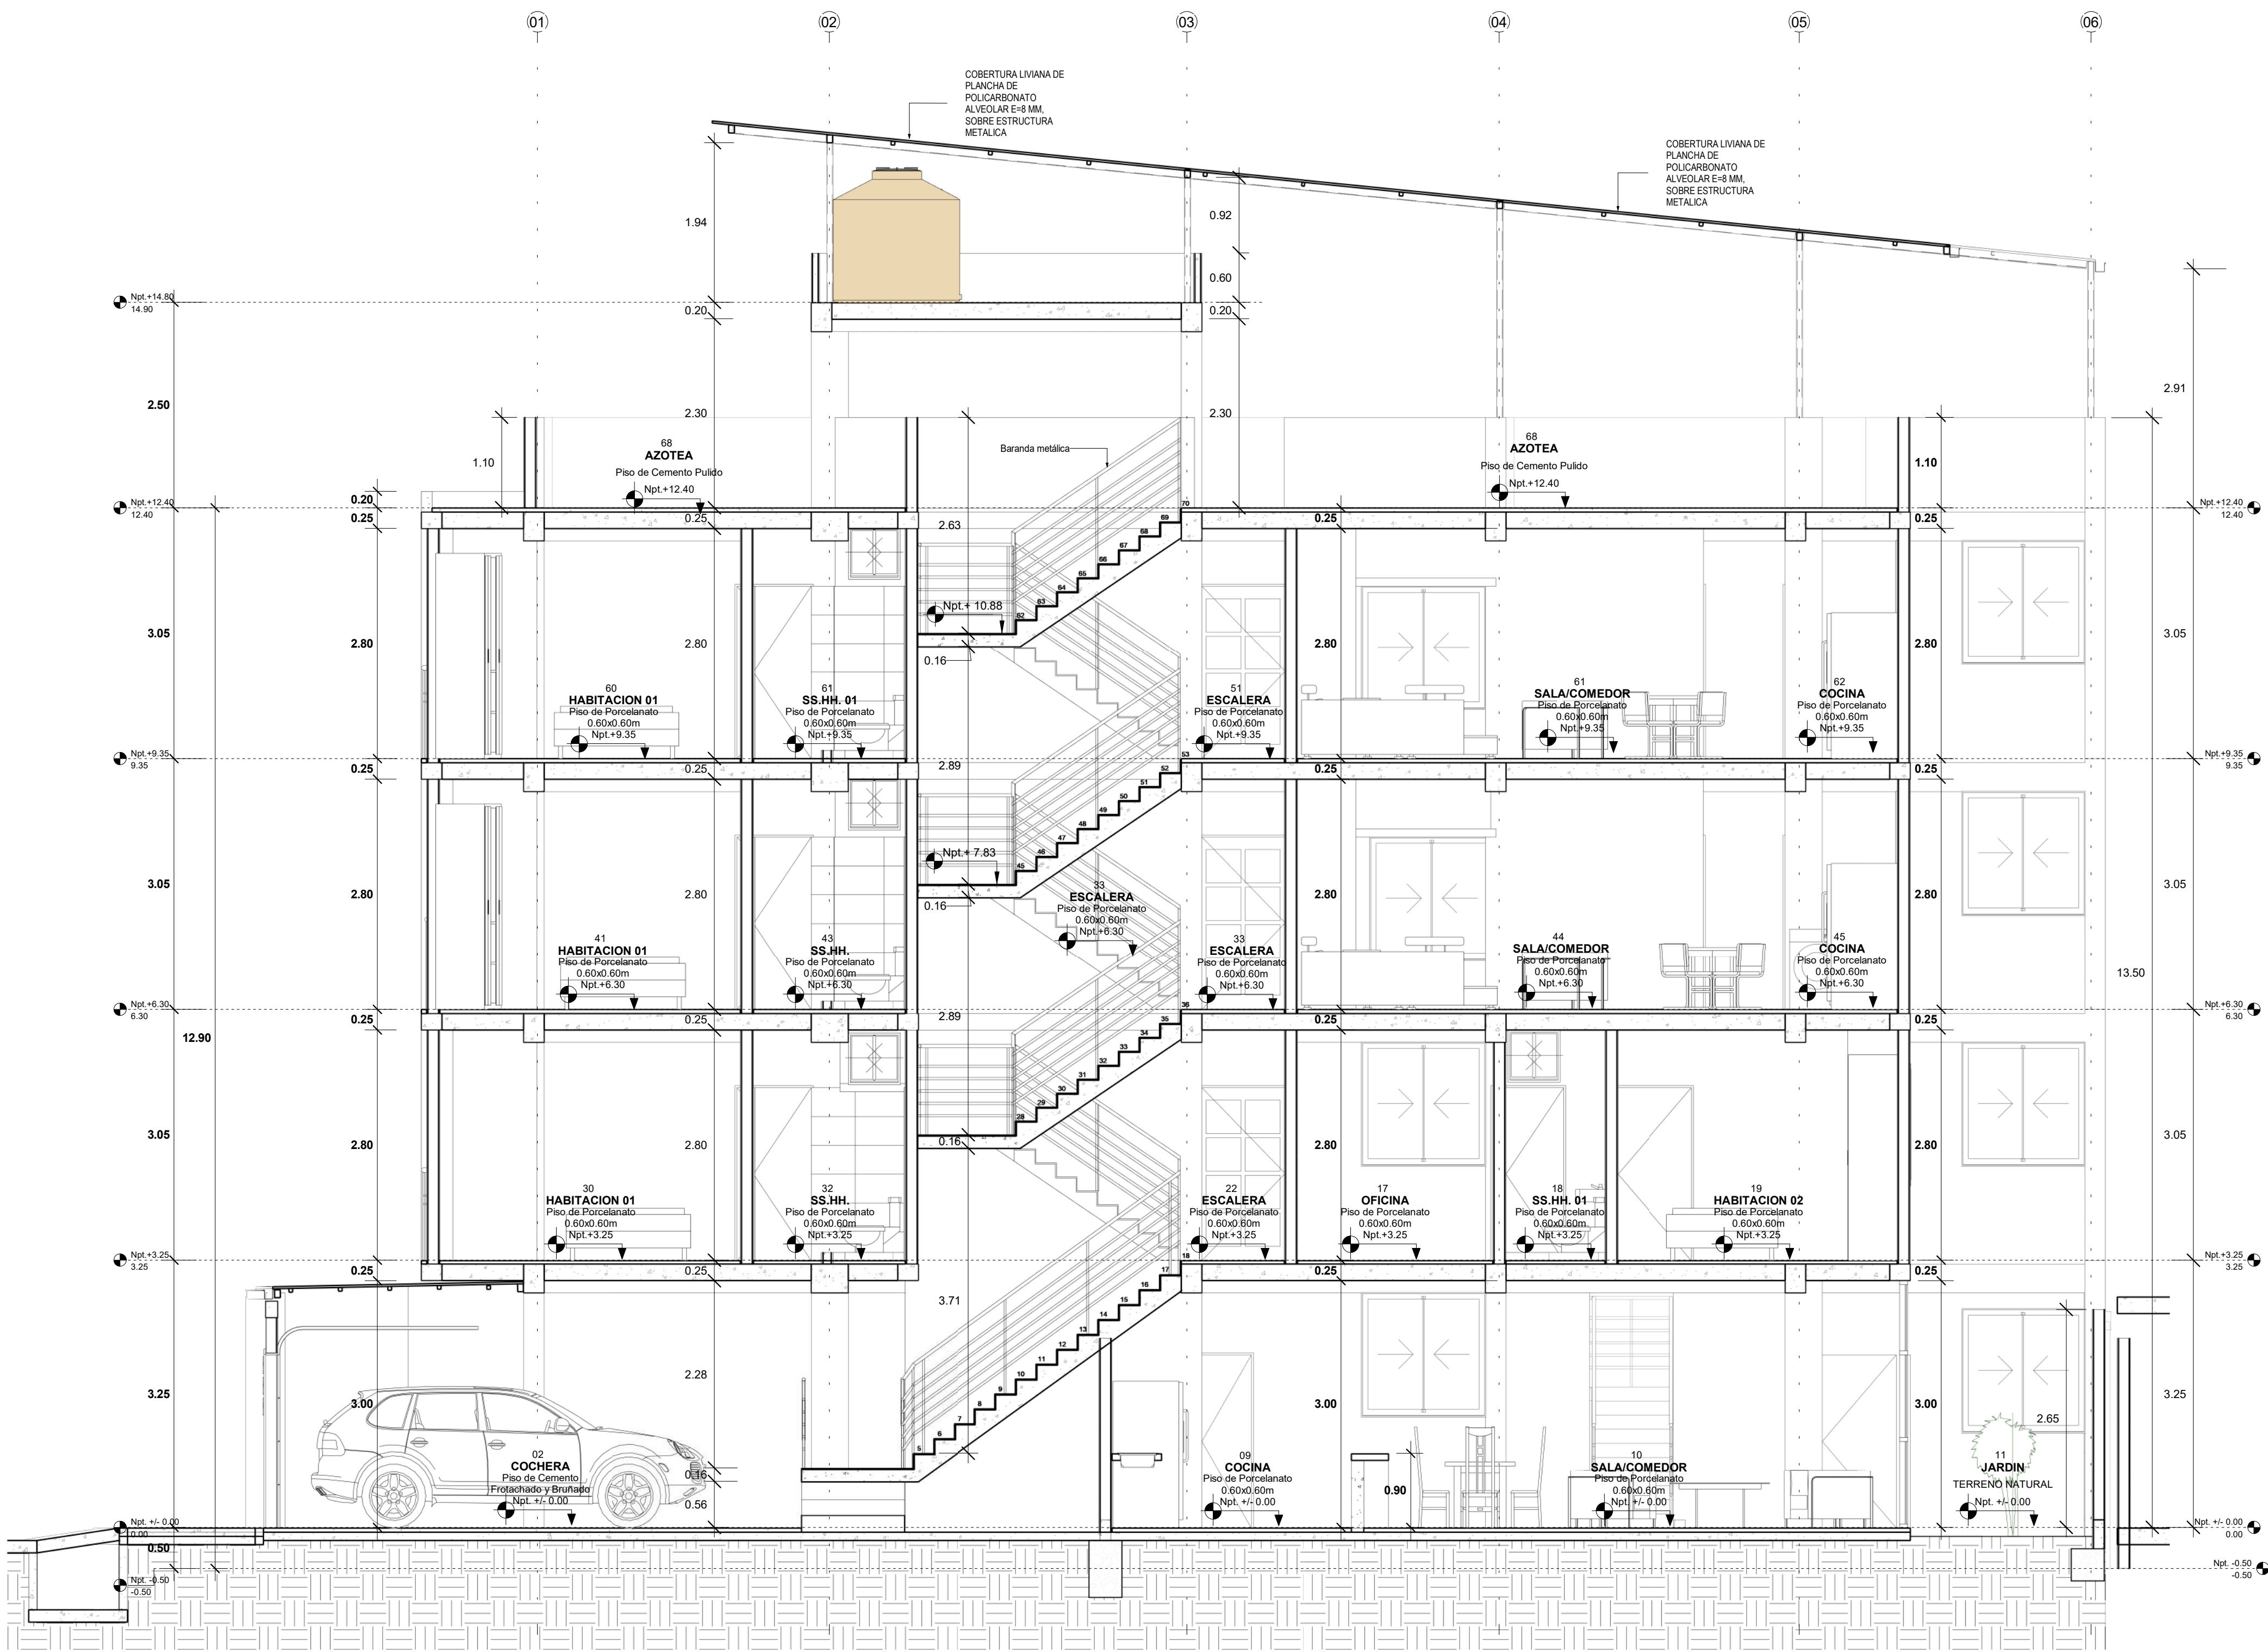


A CORTE LONGITUDINAL A-A
A-04 1:50

EDIFICIO MULTIFAMILIAR			
PROYECTO: VIVIENDA MULTIFAMILIAR			
PLANO: CORTES	FECHA: JULIO-2021		DIBUJO Y MODELADO BIM:
ESPECIALIDAD: ARQUITECTURA	ESC: 1 : 50		
DISEÑO: NELSON DAZA DONAIRES	PLANO:		
UBICACION: Jr. Libertad N° 333, barrio de Zaragoza		A-04	
Districto: MOYOBAMBA	Provincia: MOYOBAMBA		Región: SAN MARTIN
Nelson Daza Donaires			

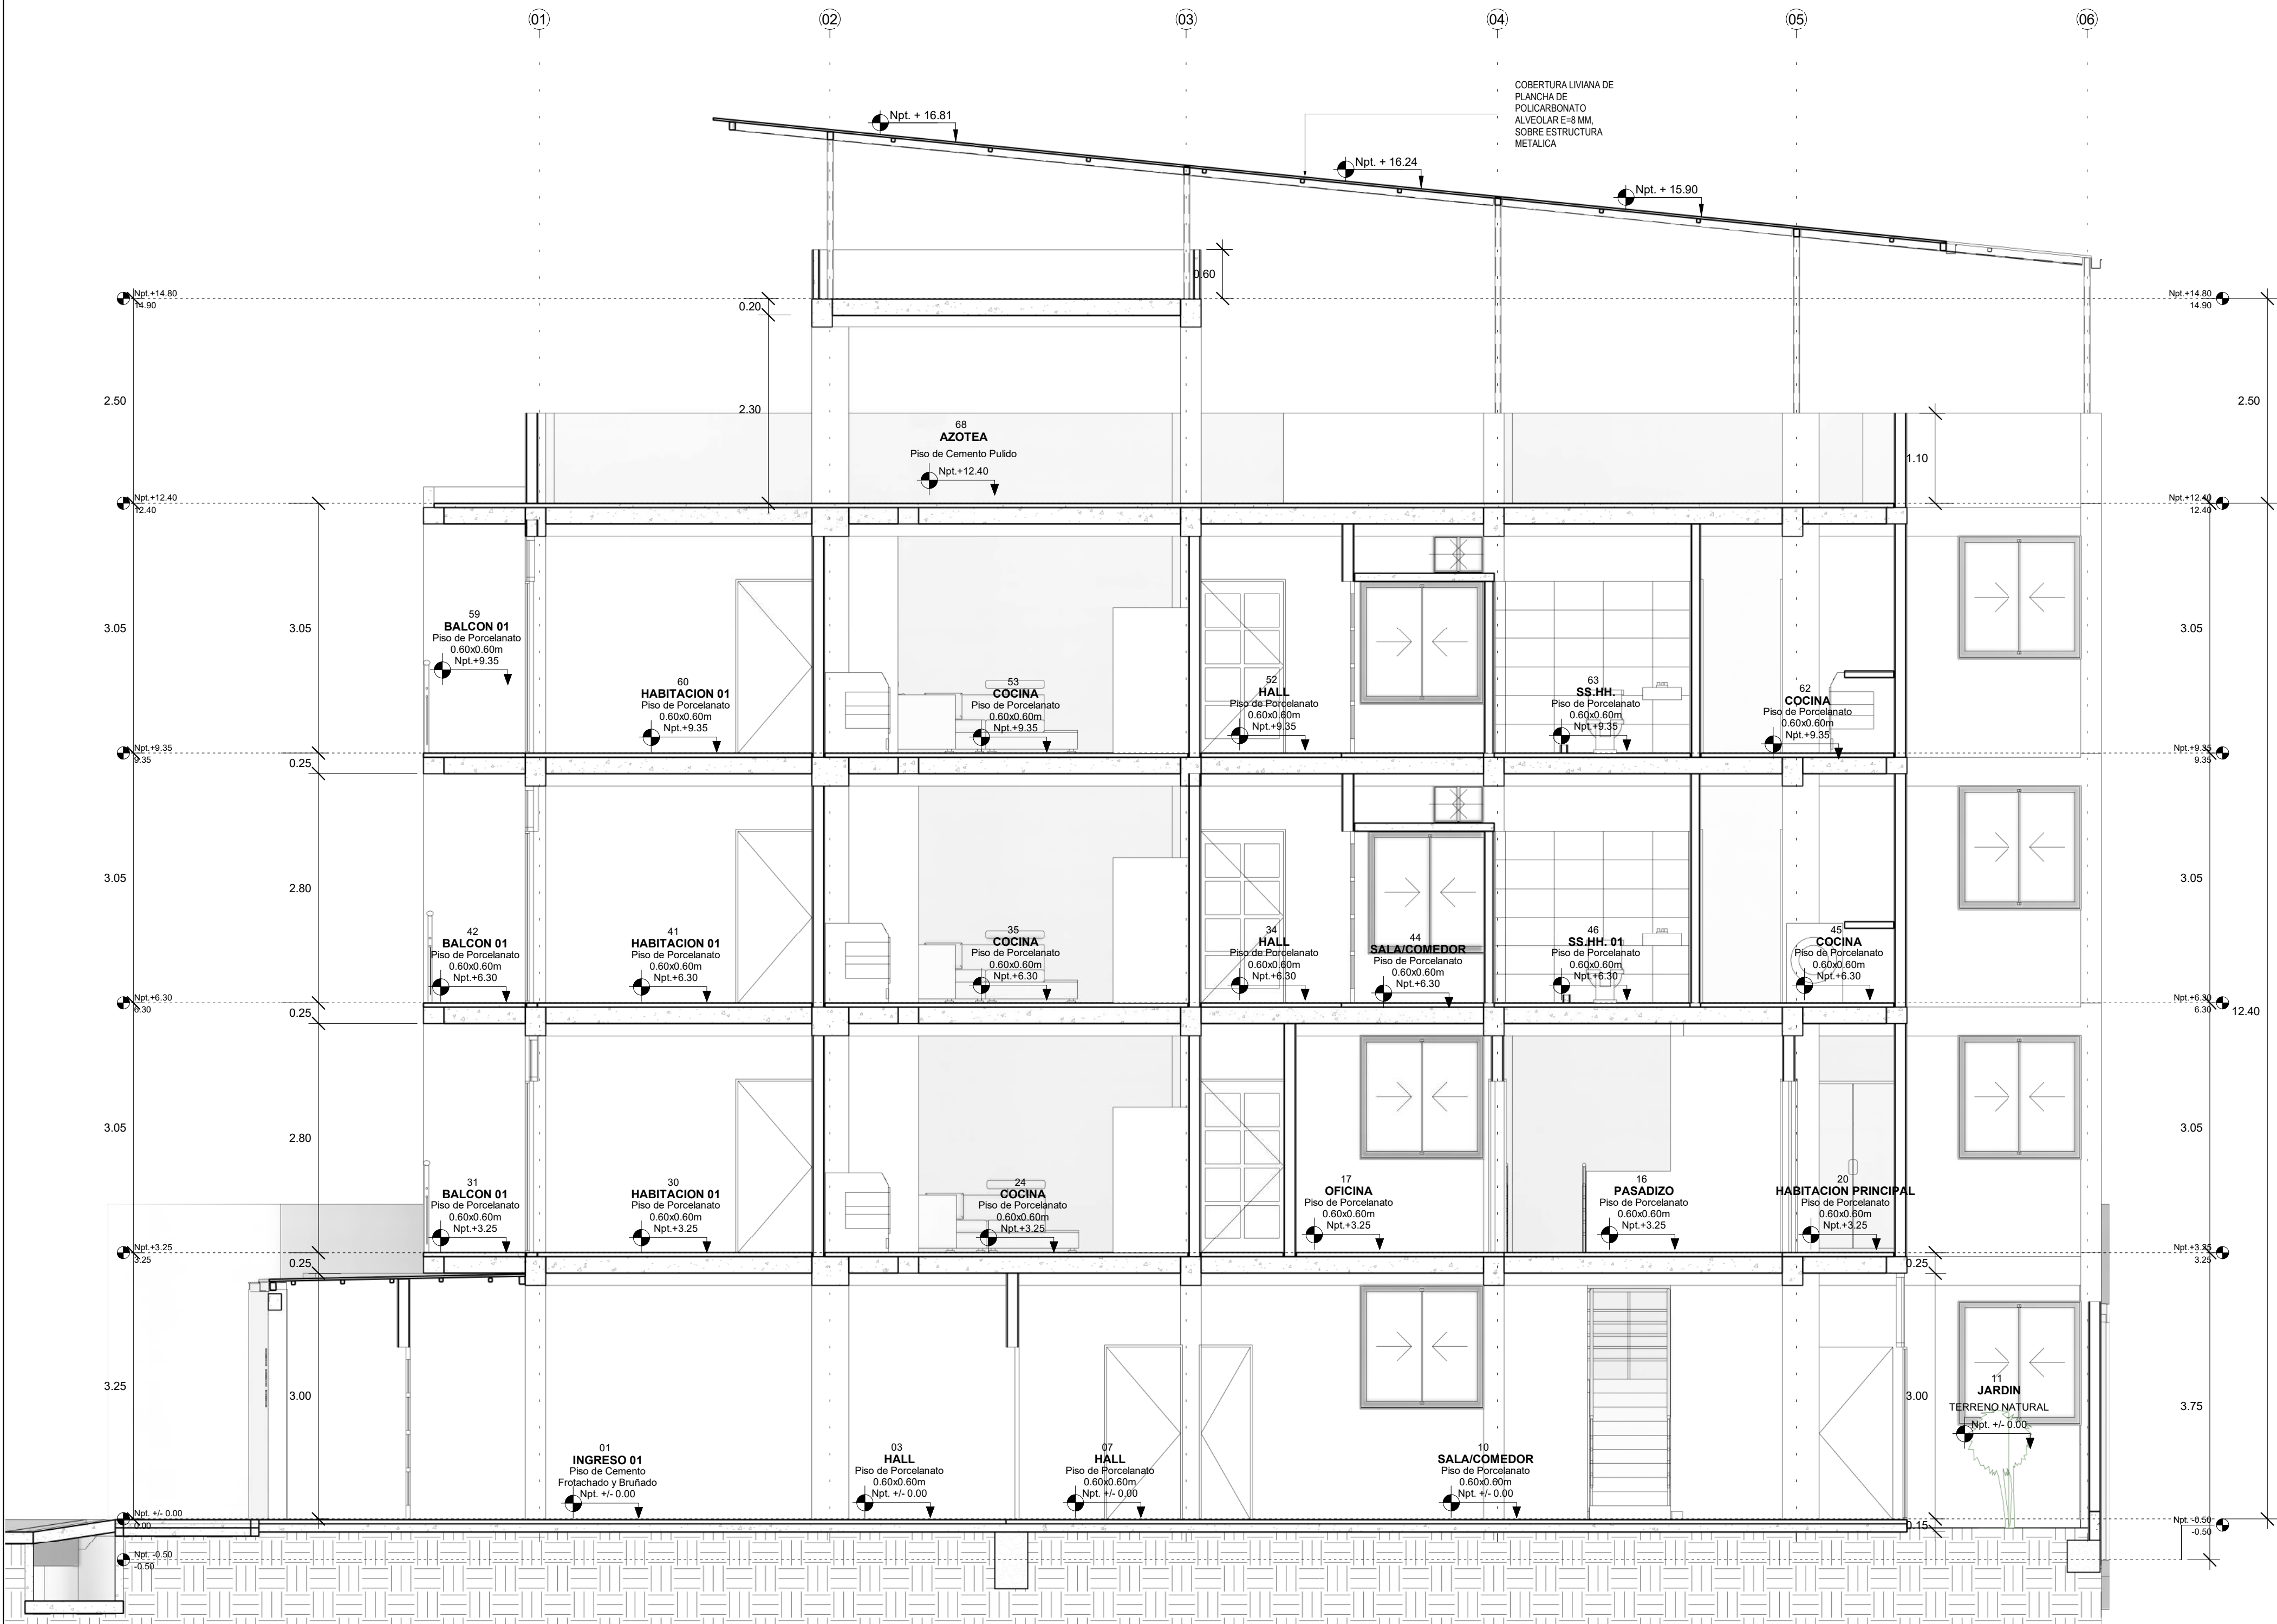


B CORTE LONGITUDINAL B-B
A-05 1:50

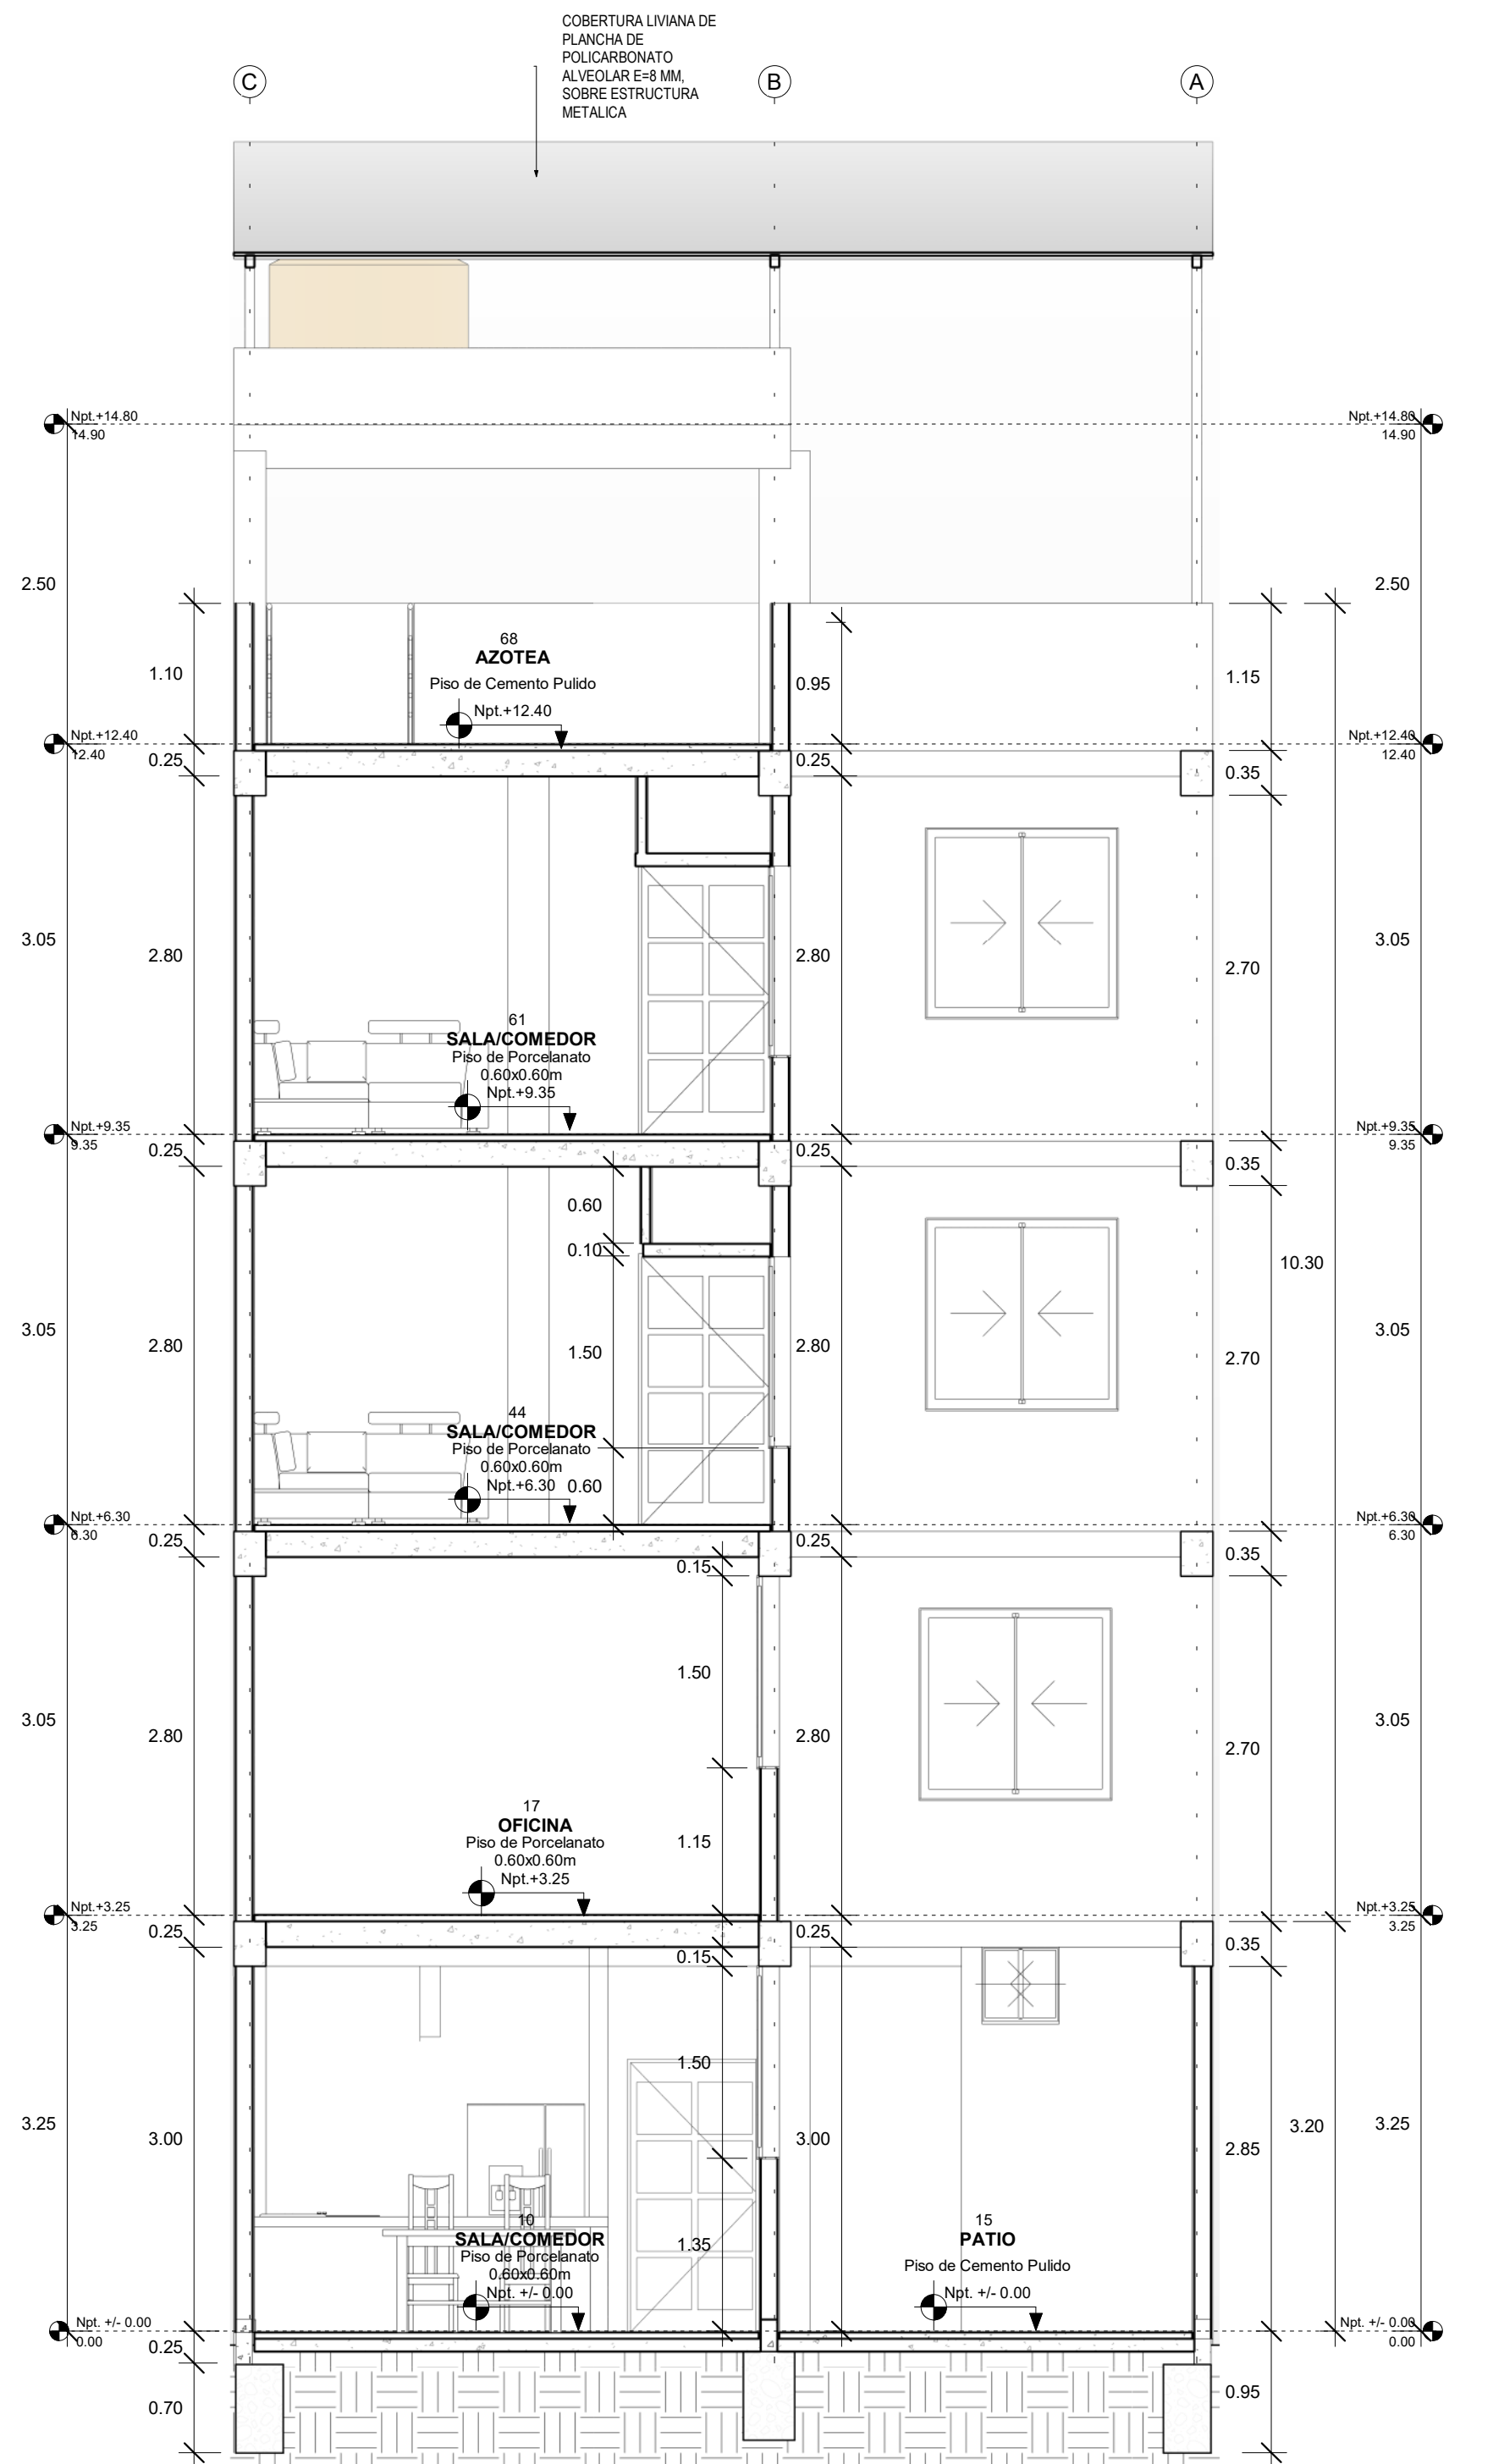


E CORTE TRANSVERSAL E-E
A-05 1:50

EDIFICIO MULTIFAMILIAR				
PROYECTO: VIVIENDA MULTIFAMILIAR				
PLANO: CORTES	FECHA: JULIO-2021	DIBUJO Y MODELADO BIM:		
ESPECIALIDAD: ARQUITECTURA	ESC: 1:50			
DISEÑO: NELSON DAZA DONAIRES	PLANO:	A-05		
UBICACION: Jr. Libertad N° 333, barrio de Zaragoza				
Dirección: MOYOBAMBA	Provincia: MOYOBAMBA	Región: SAN MARTIN	Nelson Daza Donaires	

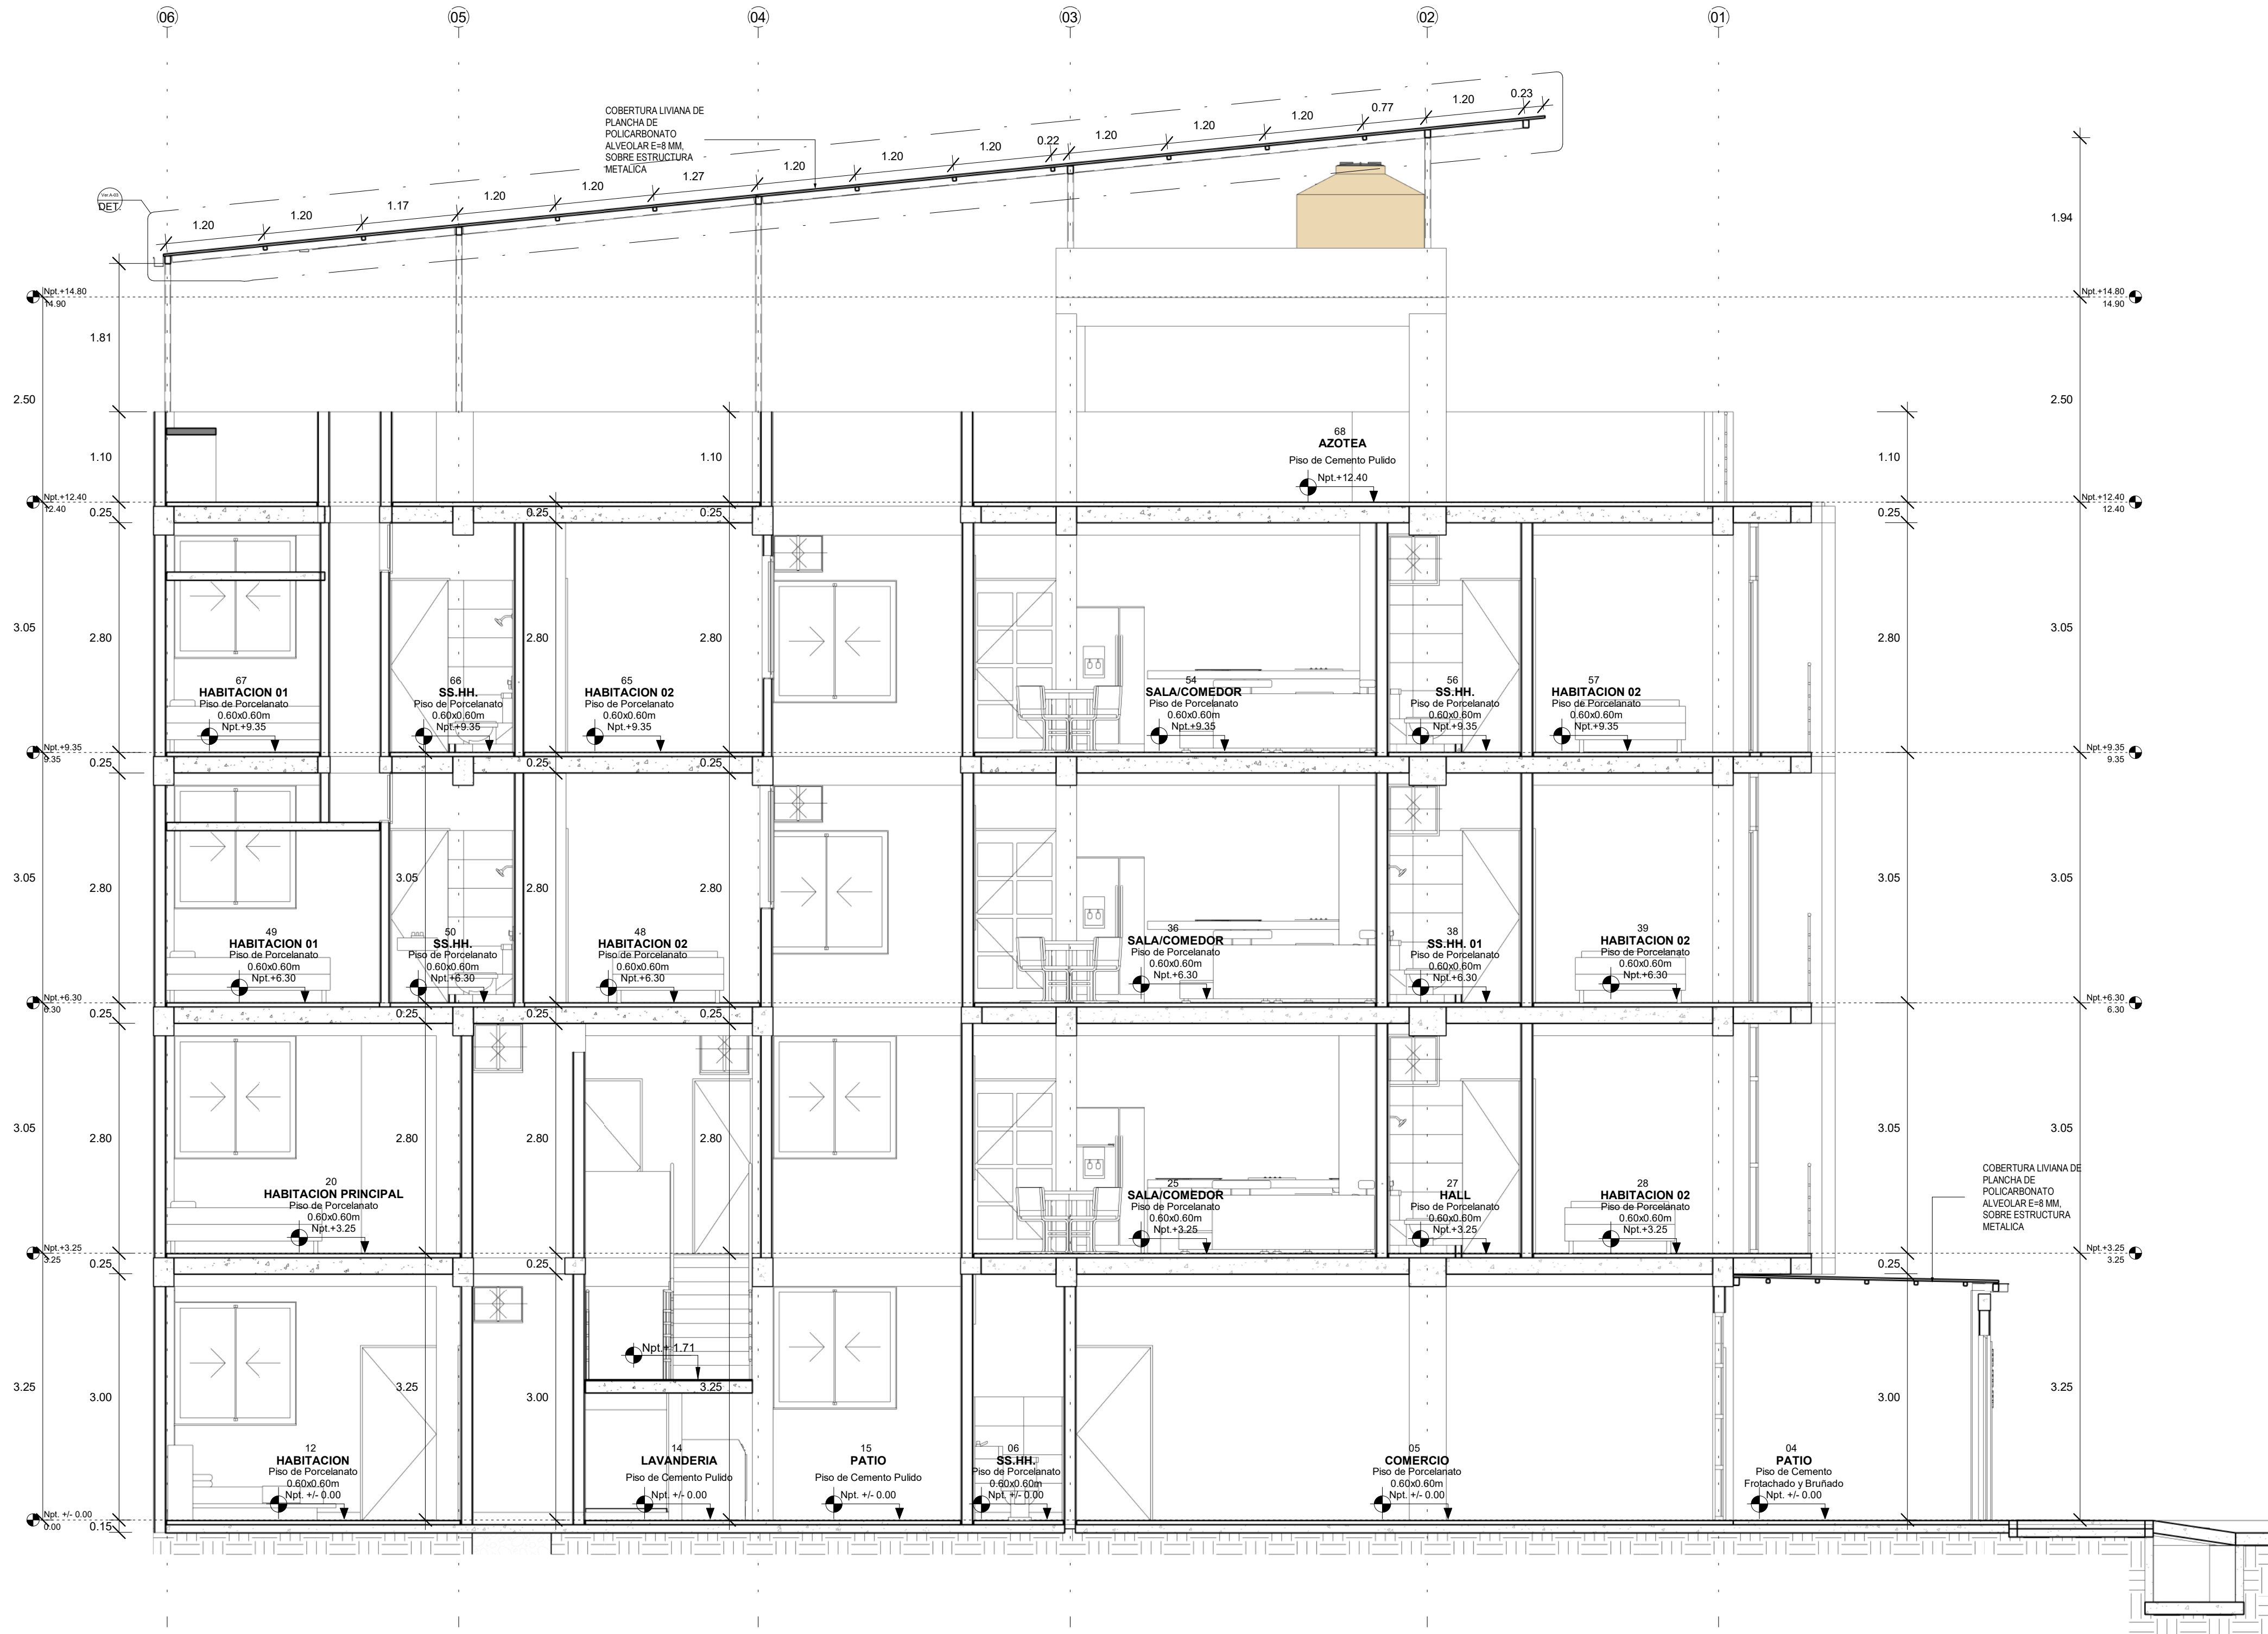

C CORTE LONGITUDINAL C-C
A-06 1: 50

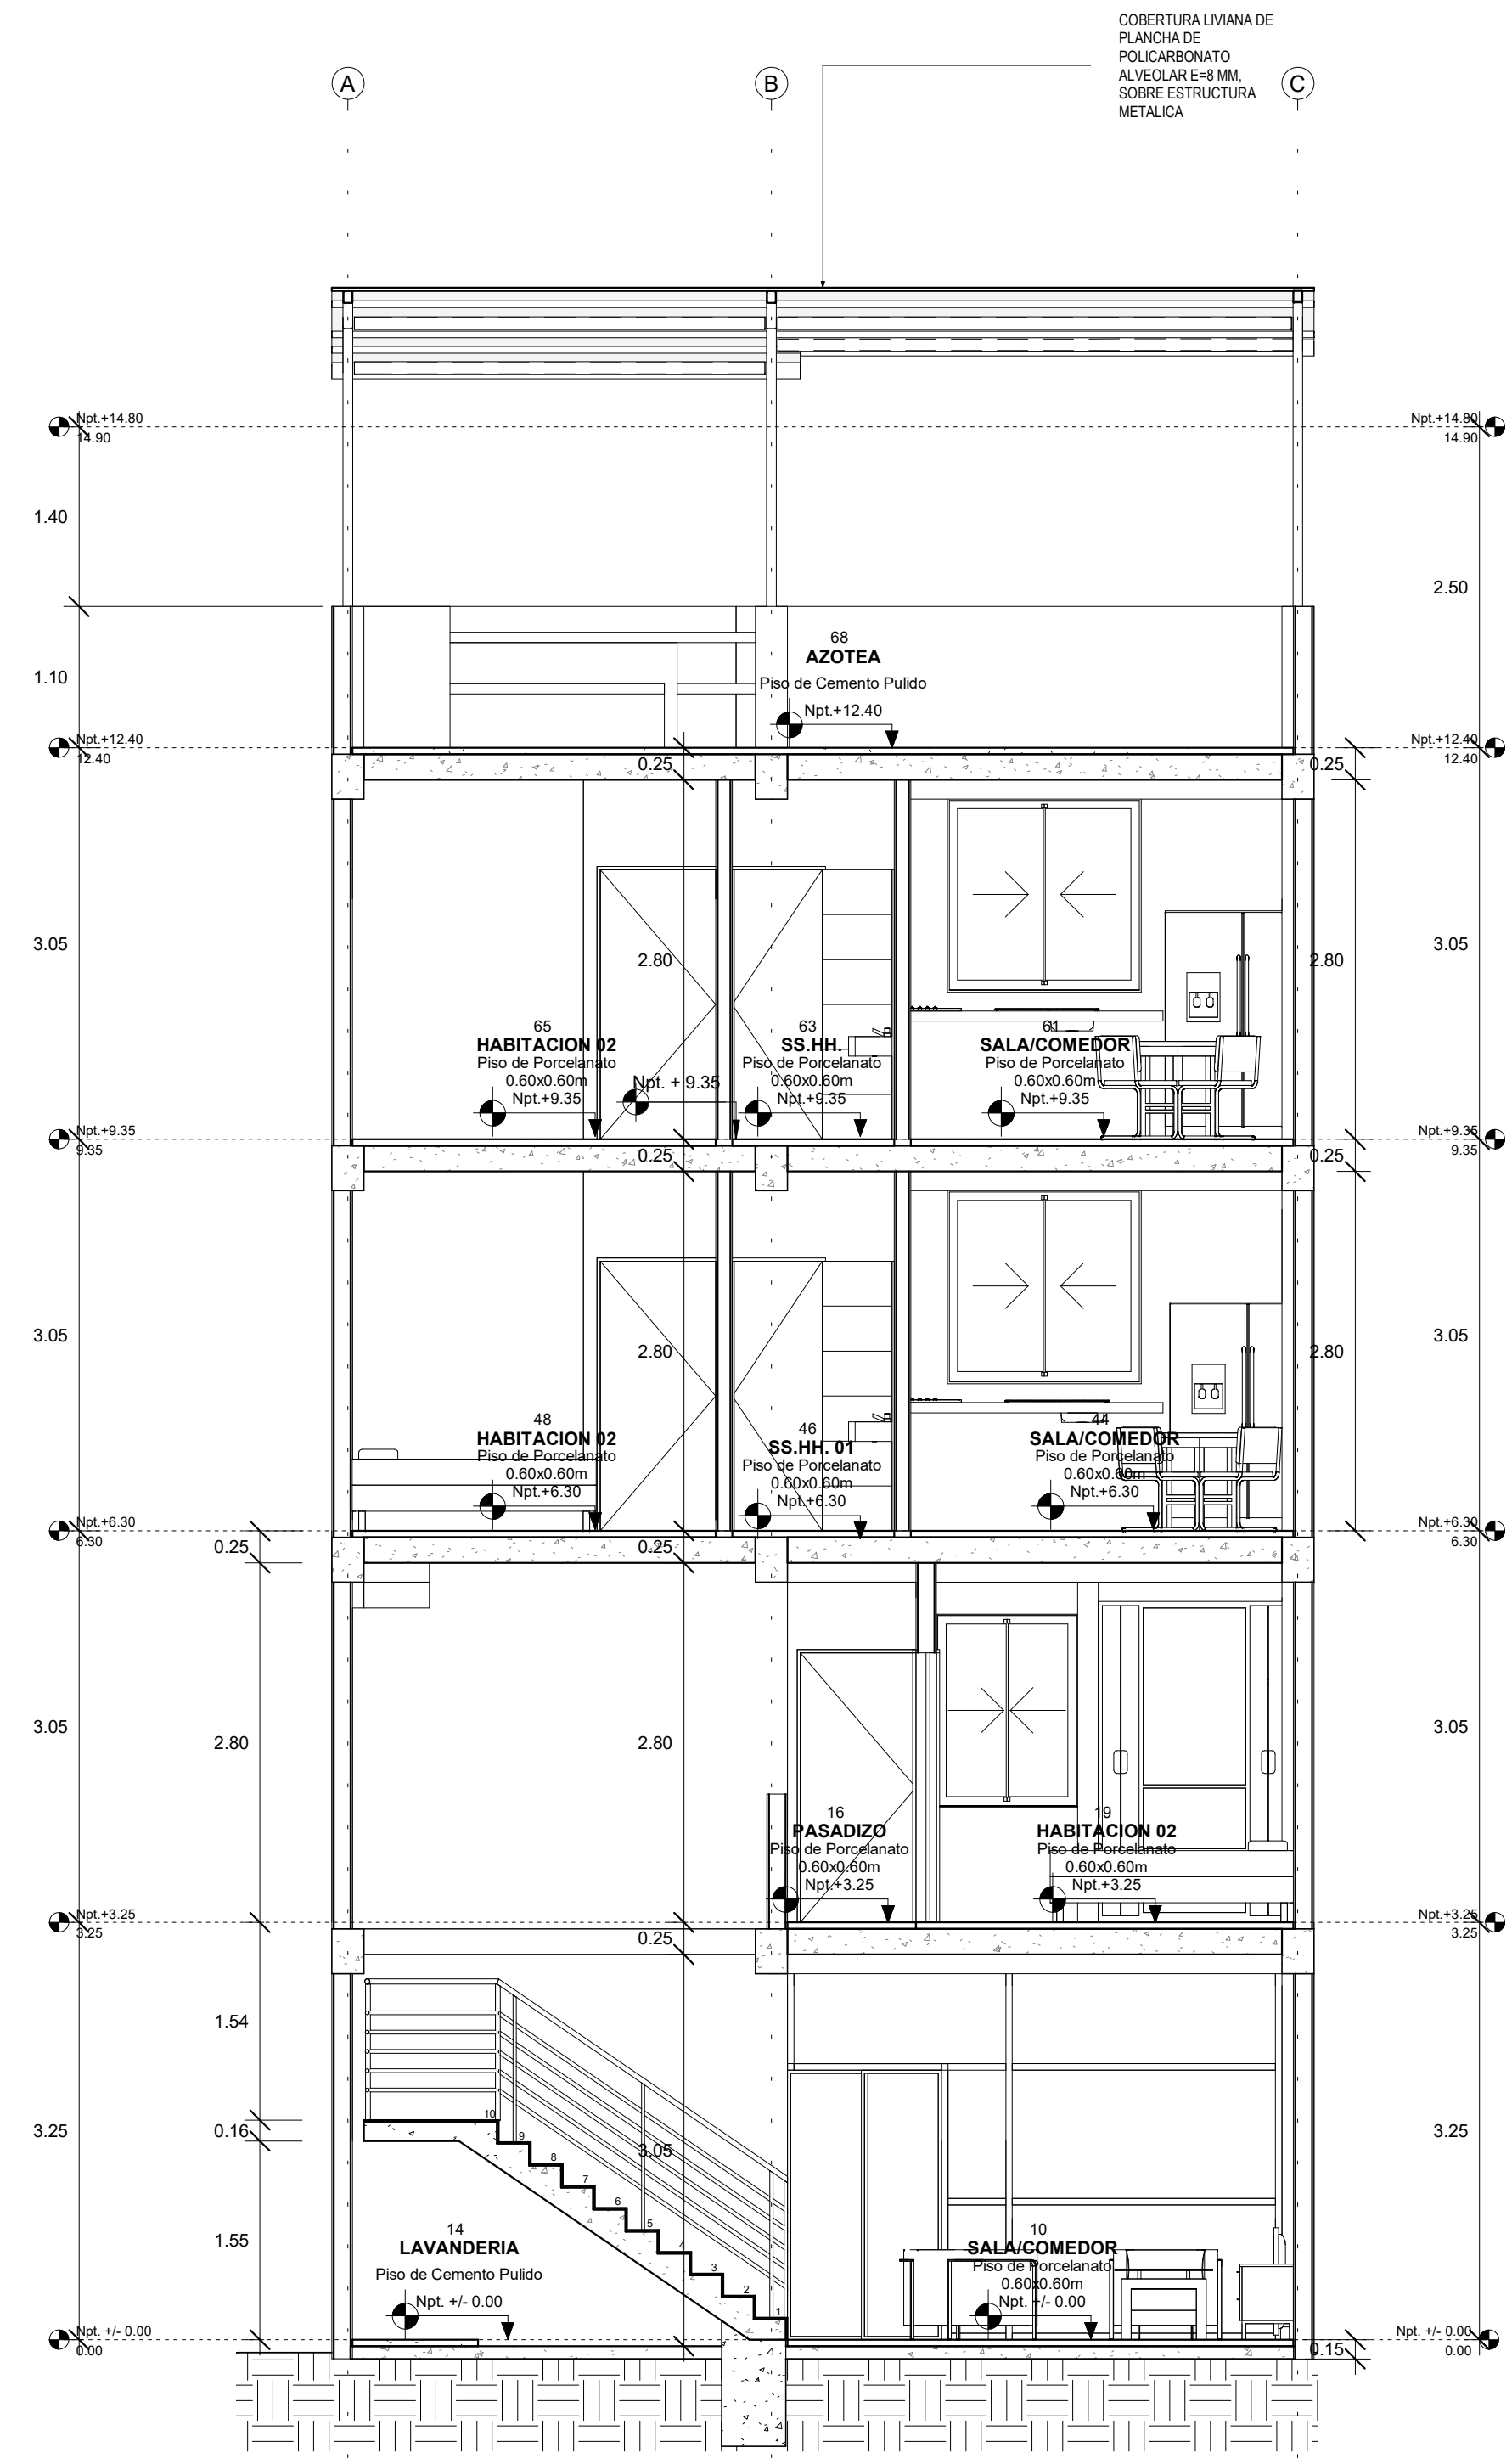

F CORTE TRANSVERSAL F-F
A-06 1: 50

EDIFICIO MULTIFAMILIAR

PROYECTO: VIVIENDA MULTIFAMILIAR				DIBUJO Y MODELADO BIM: A-06 Nelson Daza Donaire
PLANO: CORTES	FECHA: JULIO-2021			
ESPECIALIDAD: ARQUITECTURA	ESC: 1 : 50			
DISEÑO: NELSON DAZA DONAIRES	PLANO:			
UBICACION: Jr. Libertad N° 333, barrio de Zaragoza				
Distrito: MOYOBAMBA	Provincia: MOYOBAMBA	Región: SAN MARTIN		



EEDIFICIO MULTIFAMILIAR					
PROYECTO:	VIVIENDA MULTIFAMILIAR				
PLANO:	ELEVACIONES		FECHA:	JULIO-2021	DIBUJO Y MODELADO BIM: A-07 <i>Nelson Daza Donaires</i>
ESPECIALIDAD:	ARQUITECTURA		ESC:	1 : 50	
DISEÑO:	NELSON DAZA DONAIRES		PLANO:		
UBICACION:	Jr. Libertad N° 333, barrio de Zaragoza				
Distrito: MOYOBA MBA	Provincia: MOYOBA MBA	Region: SAN MARTIN			