



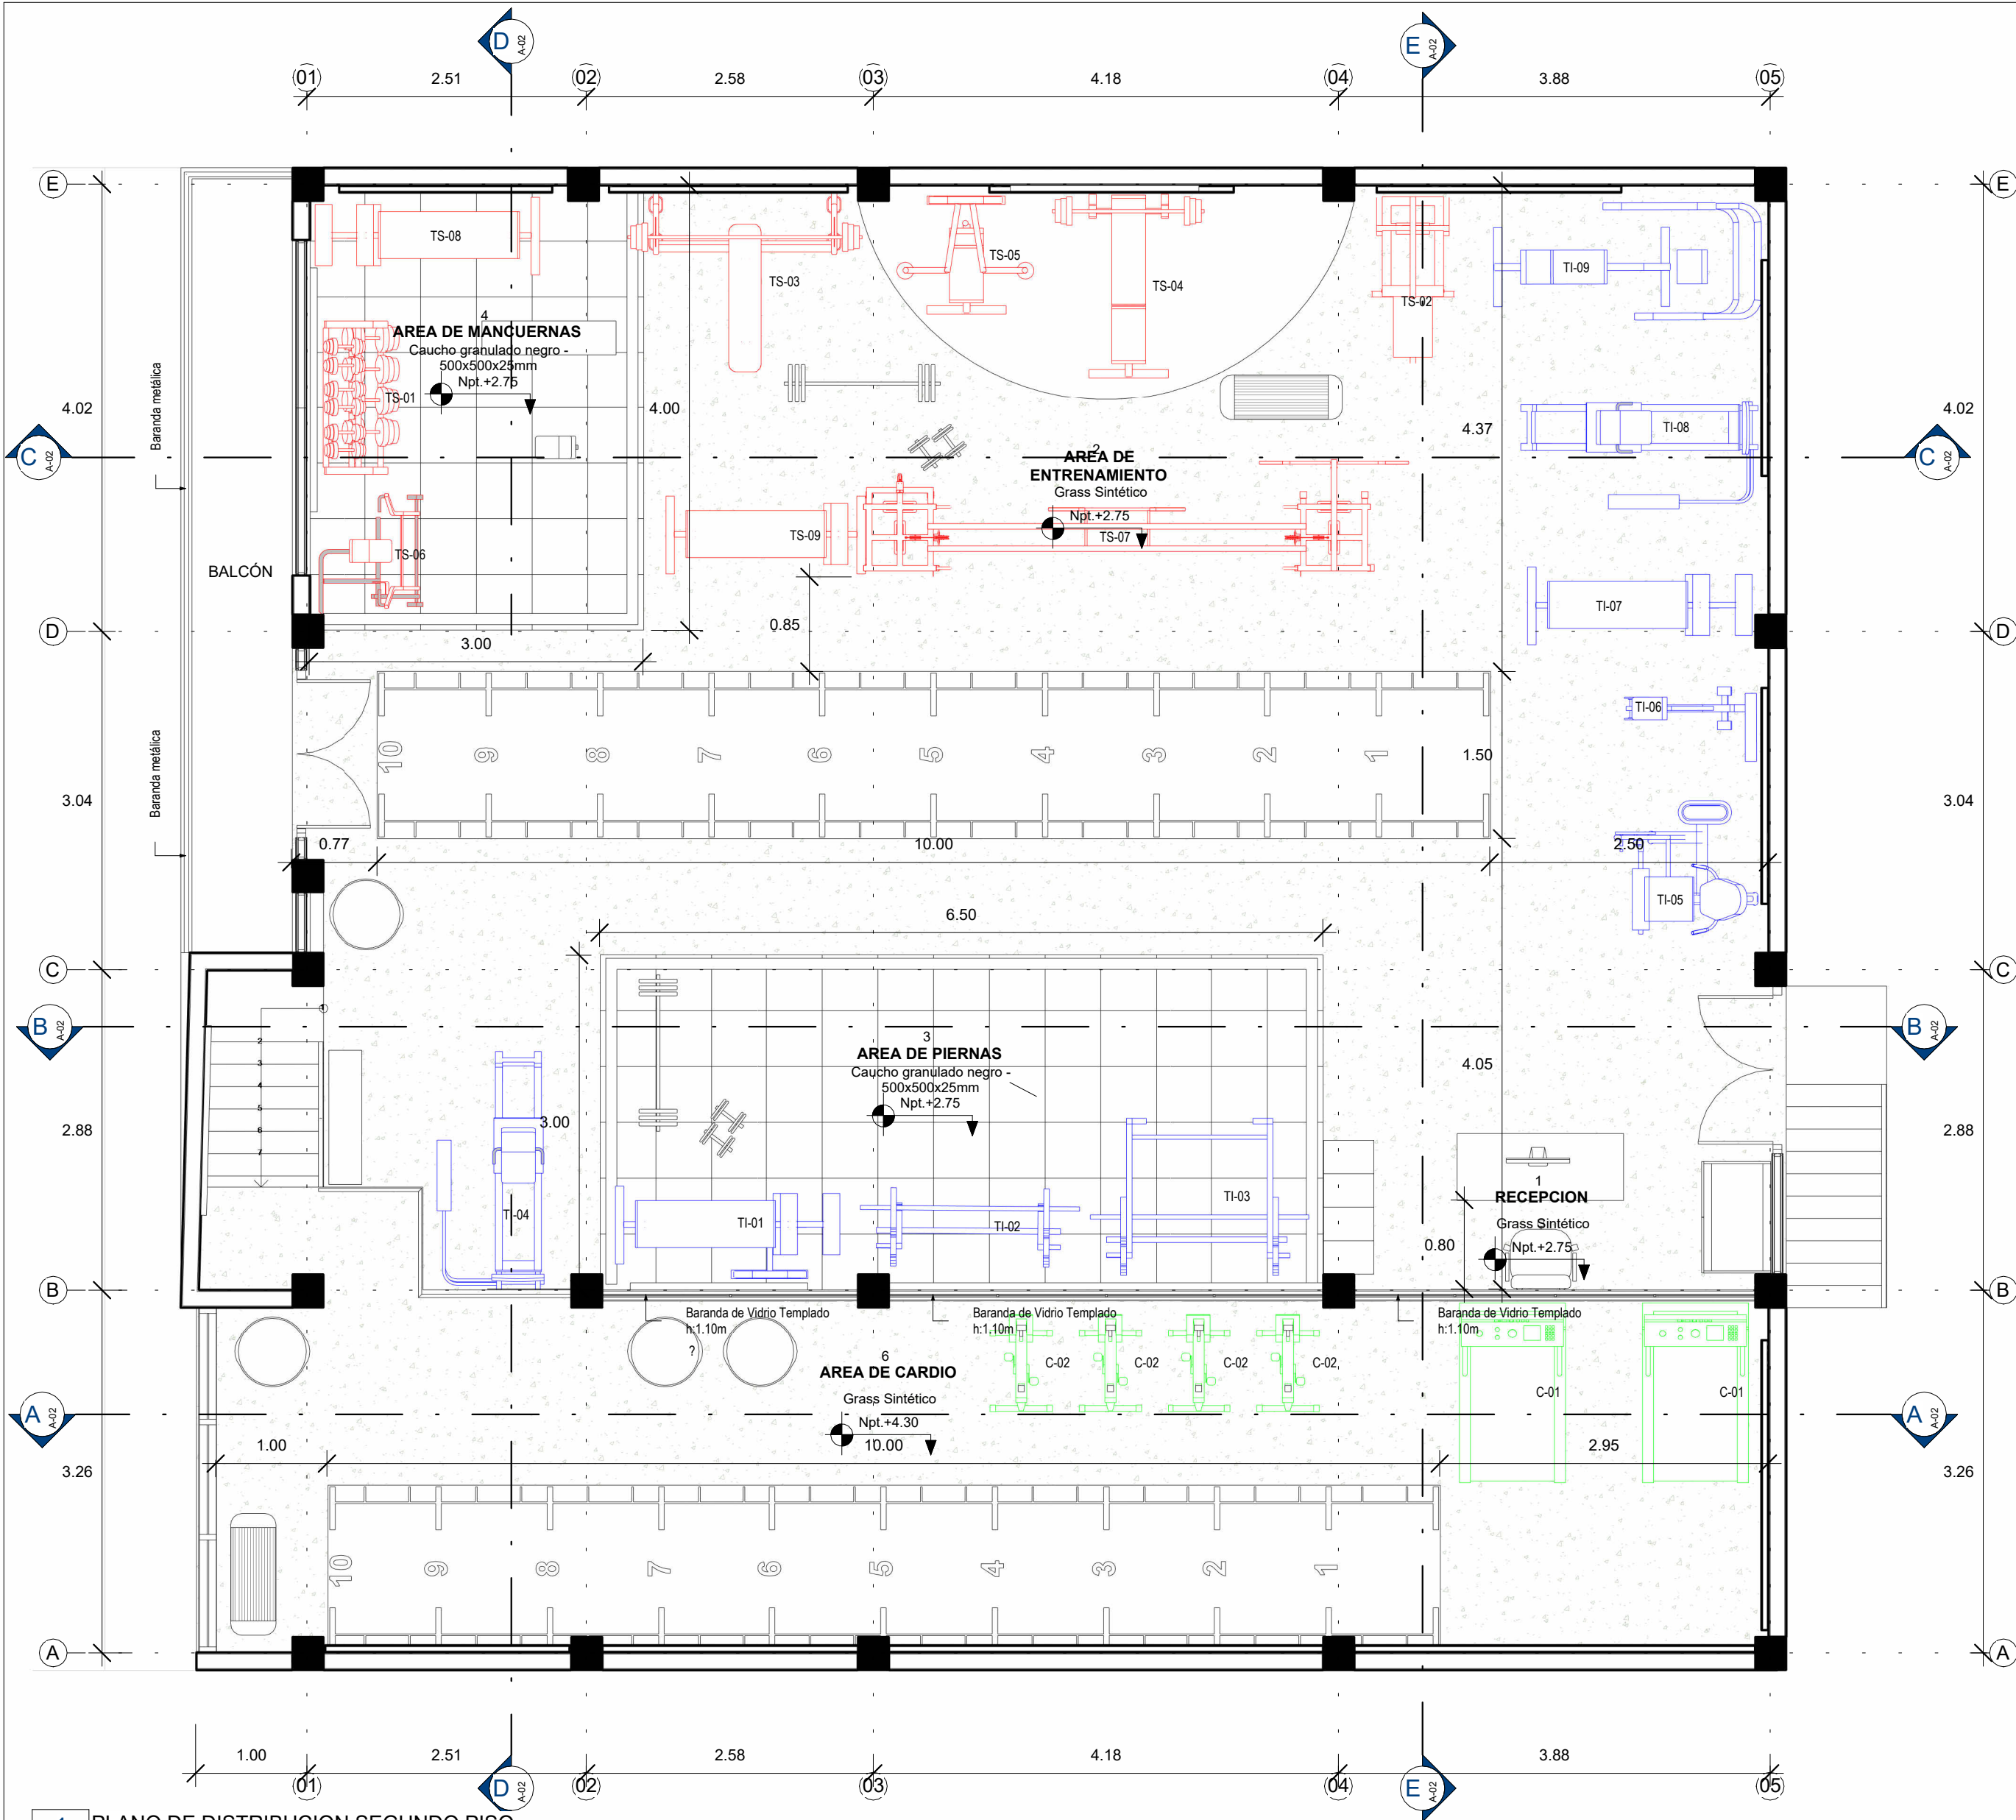

1 PLANO DE DISTRIBUCION SEGUNDO PISO
A-01 1 : 50

Tabla de planificación de equipos especializados				
Ubicación	Marca de tipo	Nivel	Tipo	Descripción
AREA DE PIERNAS	TI-01	Npt.+2.75	Curll de Femoral Tumbado	TREN INFERIOR
AREA DE PIERNAS	TI-02	Npt.+2.75	Rack de Sentadilla	TREN INFERIOR
AREA DE PIERNAS	TI-03	Npt.+2.75	Maquina smith	TREN INFERIOR
AREA DE ENTRENAMIENTO	TI-04	Npt.+2.75	Patada de Gluteo en maquina	TREN INFERIOR
AREA DE ENTRENAMIENTO	TI-05	Npt.+2.75	Extensión de Piernas	TREN INFERIOR
AREA DE ENTRENAMIENTO	TI-06	Npt.+2.75	Maquina de abductor	TREN INFERIOR
AREA DE ENTRENAMIENTO	TI-07	Npt.+2.75	Hiperextensiones	TREN INFERIOR
AREA DE ENTRENAMIENTO	TI-08	Npt.+2.75	Hack de sentadilla	TREN INFERIOR
AREA DE ENTRENAMIENTO	TI-09	Npt.+2.75	Prensa de Piernas	TREN INFERIOR

Tabla de planificación de equipos especializados				
Ubicación	Marca de tipo	Nivel	Tipo	Descripción
AREA DE MANCUERNAS	TS-01	Npt.+2.75	Rack de mancuernas	TREN SUPERIOR
AREA DE ENTRENAMIENTO	TS-02	Npt.+2.75	Polea Alta	TREN SUPERIOR
AREA DE ENTRENAMIENTO	TS-03	Npt.+2.75	Press Horizontal	TREN SUPERIOR
AREA DE ENTRENAMIENTO	TS-04	Npt.+2.75	Press Inclinado	TREN SUPERIOR
AREA DE ENTRENAMIENTO	TS-05	Npt.+2.75	Máquina contractora de pecho	TREN SUPERIOR
AREA DE MANCUERNAS	TS-06	Npt.+2.75	Banco scott	TREN SUPERIOR
AREA DE ENTRENAMIENTO	TS-07	Npt.+2.75	Polea Multifuncional	TREN SUPERIOR
AREA DE MANCUERNAS	TS-08	Npt.+2.75	Barra T	TREN SUPERIOR
AREA DE ENTRENAMIENTO	TS-09	Npt.+2.75	Banco declinado	TREN SUPERIOR

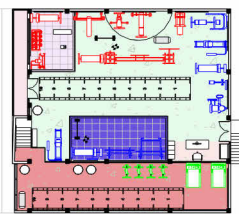


Legenda de número

- AREA DE CARDIO
- AREA DE ENTRENAMIENTO
- AREA DE MANCUERNAS
- AREA DE PIERNAS
- BALCÓN
- RECEPCION

CUADRO DE AREAS				
N°	Nombre	Acabado del suelo	Área	Recomendaciones
1	RECEPCION	Grass Sintético	5.14	Opciones de Pisos mayor a menor costo: 1. Piso de caucho tipo baldosa 0.50x0.50x25mm 2. Piso de caucho Interlock 6 o 10 mm 3. Piso de Grass sintético 4. Alfombra comercial
2	AREA DE ENTRENAMIENTO	Grass Sintético	91.89	Piso de caucho EPDM 1.10mx10mx6mm/similar
3	AREA DE PIERNAS	Caucho granulado negro - 500x500x25mm	18.83	Piso de caucho EPDM 1.10mx10mx6mm/similar
4	AREA DE MANCUERNAS	Caucho granulado negro - 500x500x25mm	11.93	Piso de caucho EPDM 1.10mx10mx6mm/similar
5	BALCÓN	Piso de Cemento Pulido	6.32	Piso existente
6	AREA DE CARDIO	Grass Sintético	45.60	Opciones de Pisos mayor a menor costo: 1. Piso de caucho tipo baldosa 0.50x0.50x25mm 2. Piso de caucho Interlock 6 o 10 mm 3. Piso de Grass sintético 4. Alfombra comercial

Total general: 6 179.72

Acabado de Pisos		
Marca de tipo	Tipo	Área
P-01	Caucho granulado negro - 500x500x25mm	31.50
Total general: 2		31.50

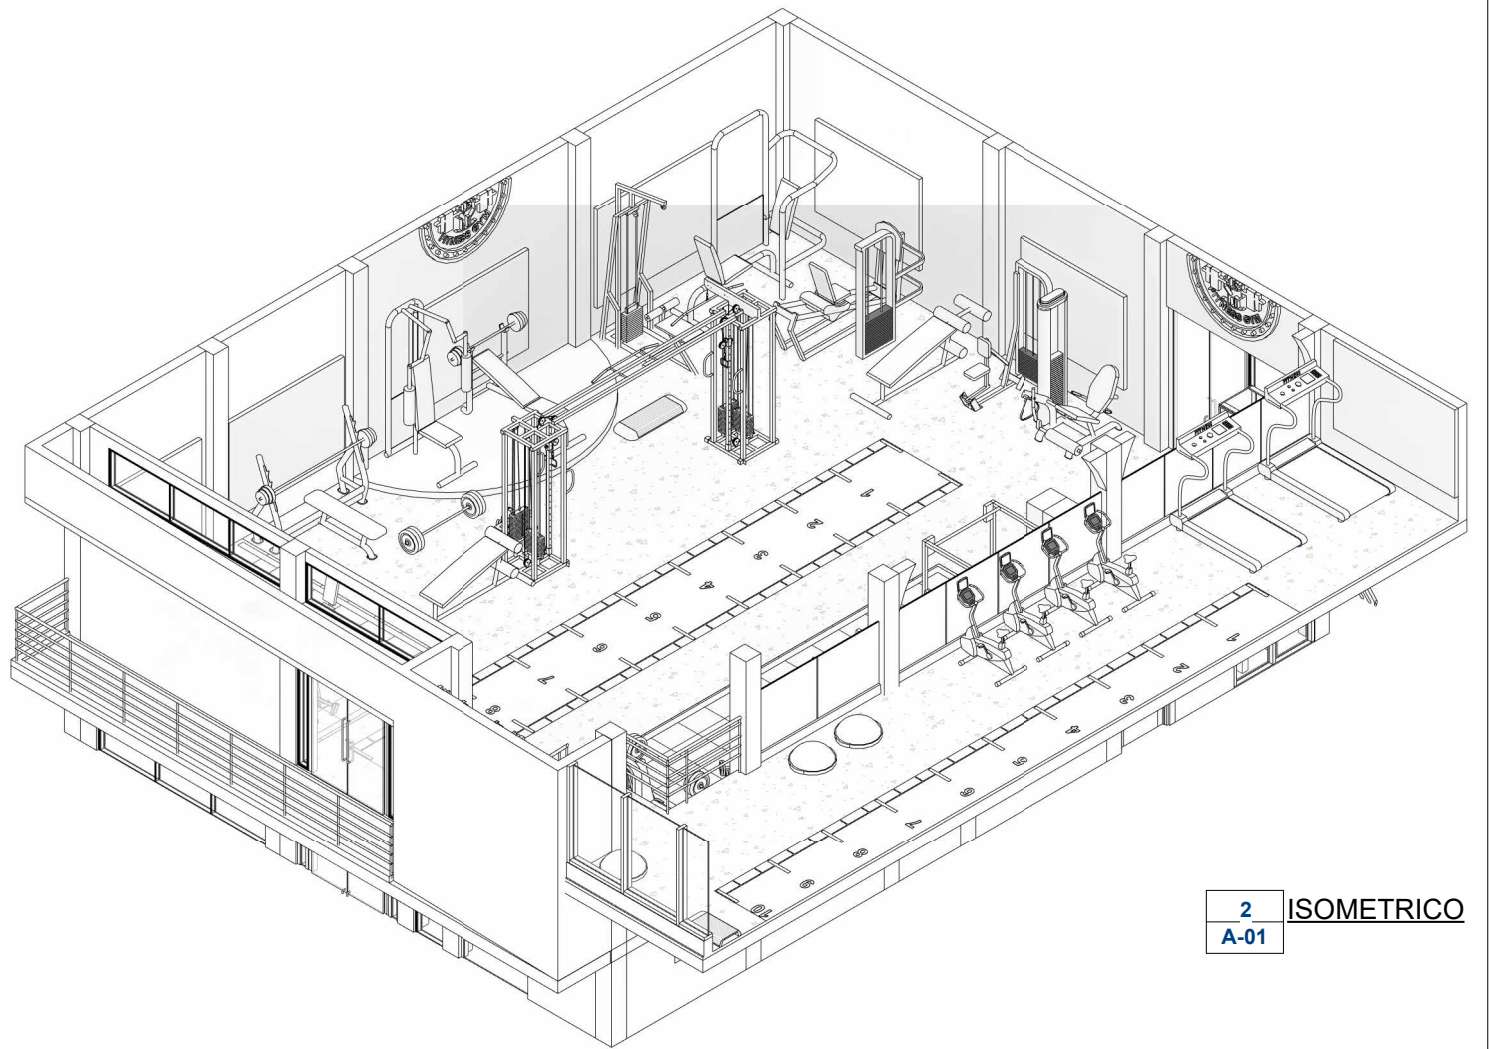


2 ISOMETRICO
A-01


Tabla de planificación de equipos especializados				
Ubicación	Marca de tipo	Nivel	Tipo	Descripción
AREA DE CARDIO	C-01	Npt.+4.30	Trotadora	CARDIO
AREA DE CARDIO	C-01	Npt.+4.30	Trotadora	CARDIO
AREA DE CARDIO	C-02	Npt.+4.30	Bicicleta estacionaria	CARDIO
AREA DE CARDIO	C-02	Npt.+4.30	Bicicleta estacionaria	CARDIO
AREA DE CARDIO	C-02	Npt.+4.30	Bicicleta estacionaria	CARDIO
AREA DE CARDIO	C-02	Npt.+4.30	Bicicleta estacionaria	CARDIO

PROYECTO DE REMODELACION LOCAL COMERCIAL


PROYECTO: REMODELACION GIMNASIO POPEYES GYM			
PLANO: PLANO DE DISTRIBUCION PRIMER	FECHA: MAR-2023	BIM MANAGER: Nelson Daza Donaires	
ESPECIALIDAD: ARQUITECTURA	ESC: Como se indica		
DISEÑO: NELSON DAZA DONAIRES	PLANO: A-01		
UBICACION: Jr. Santa María cdra. 01	Districto: MOYOBAMBA	Provincia: MOYOBAMBA	Región: SAN MARTIN

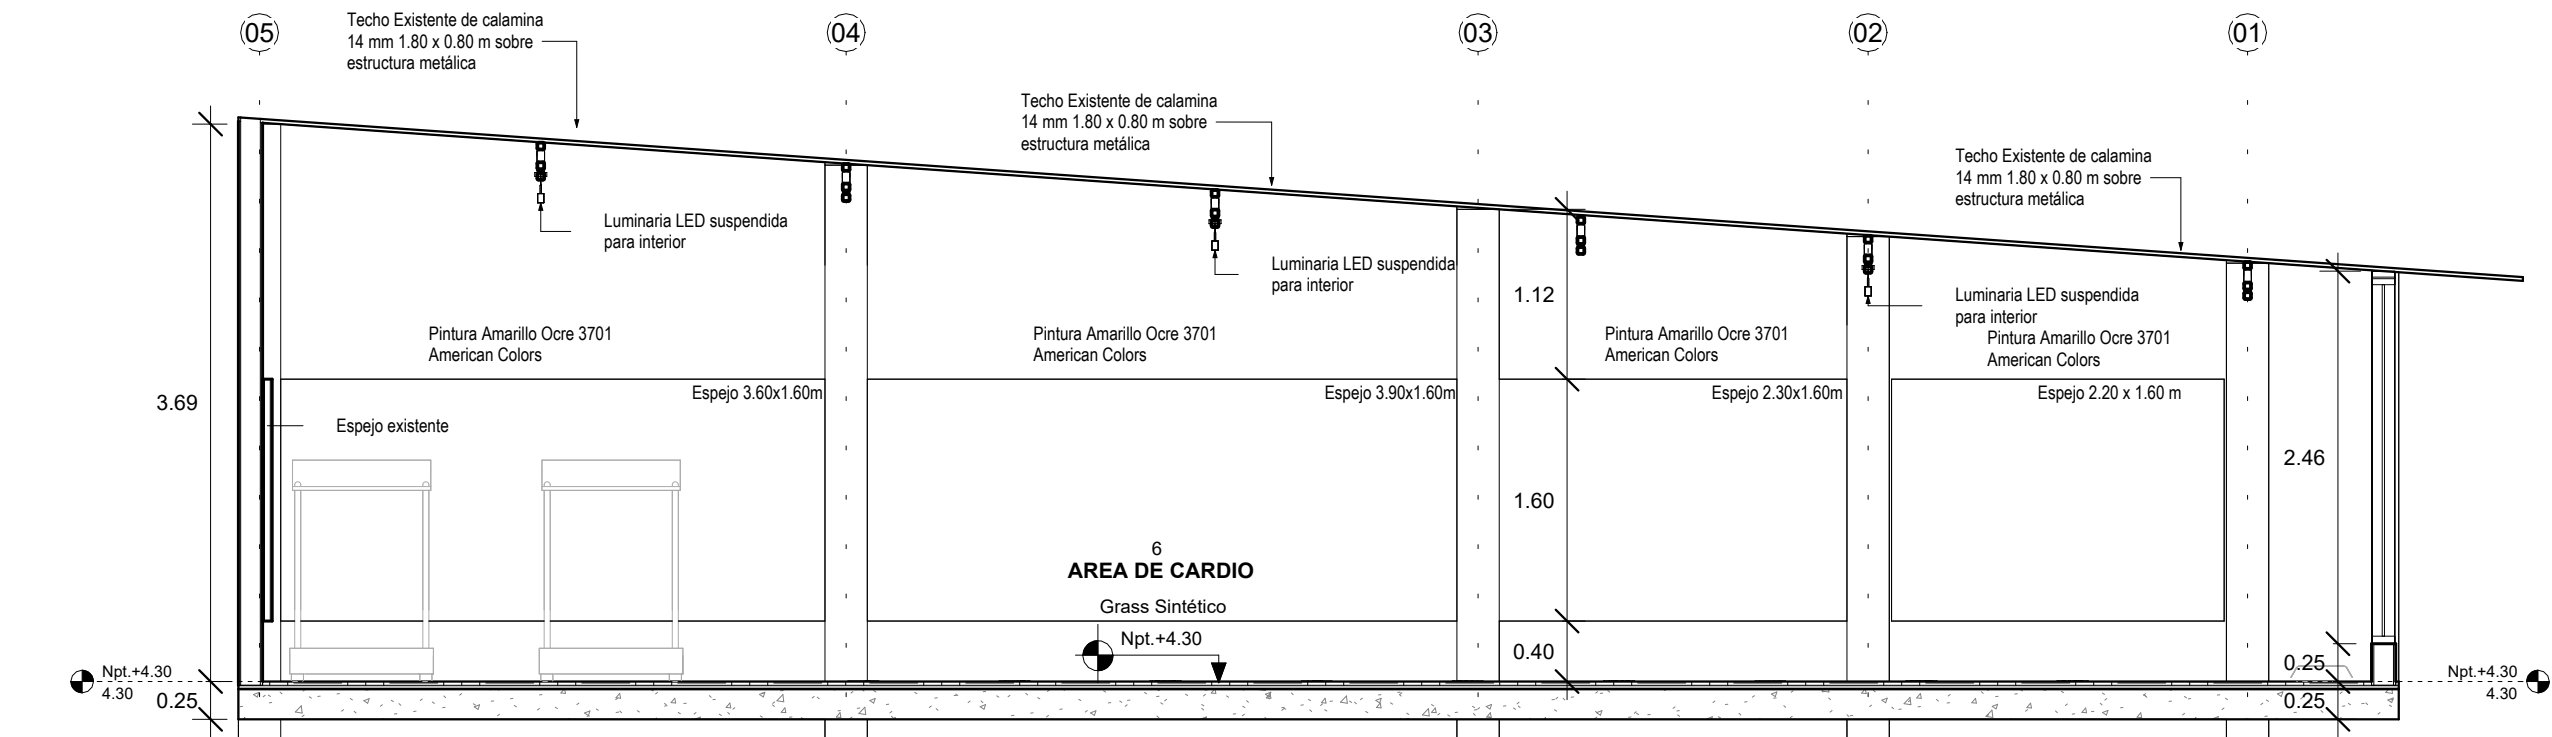


A CORTE LONGITUDINAL A-A
A-02 1:50

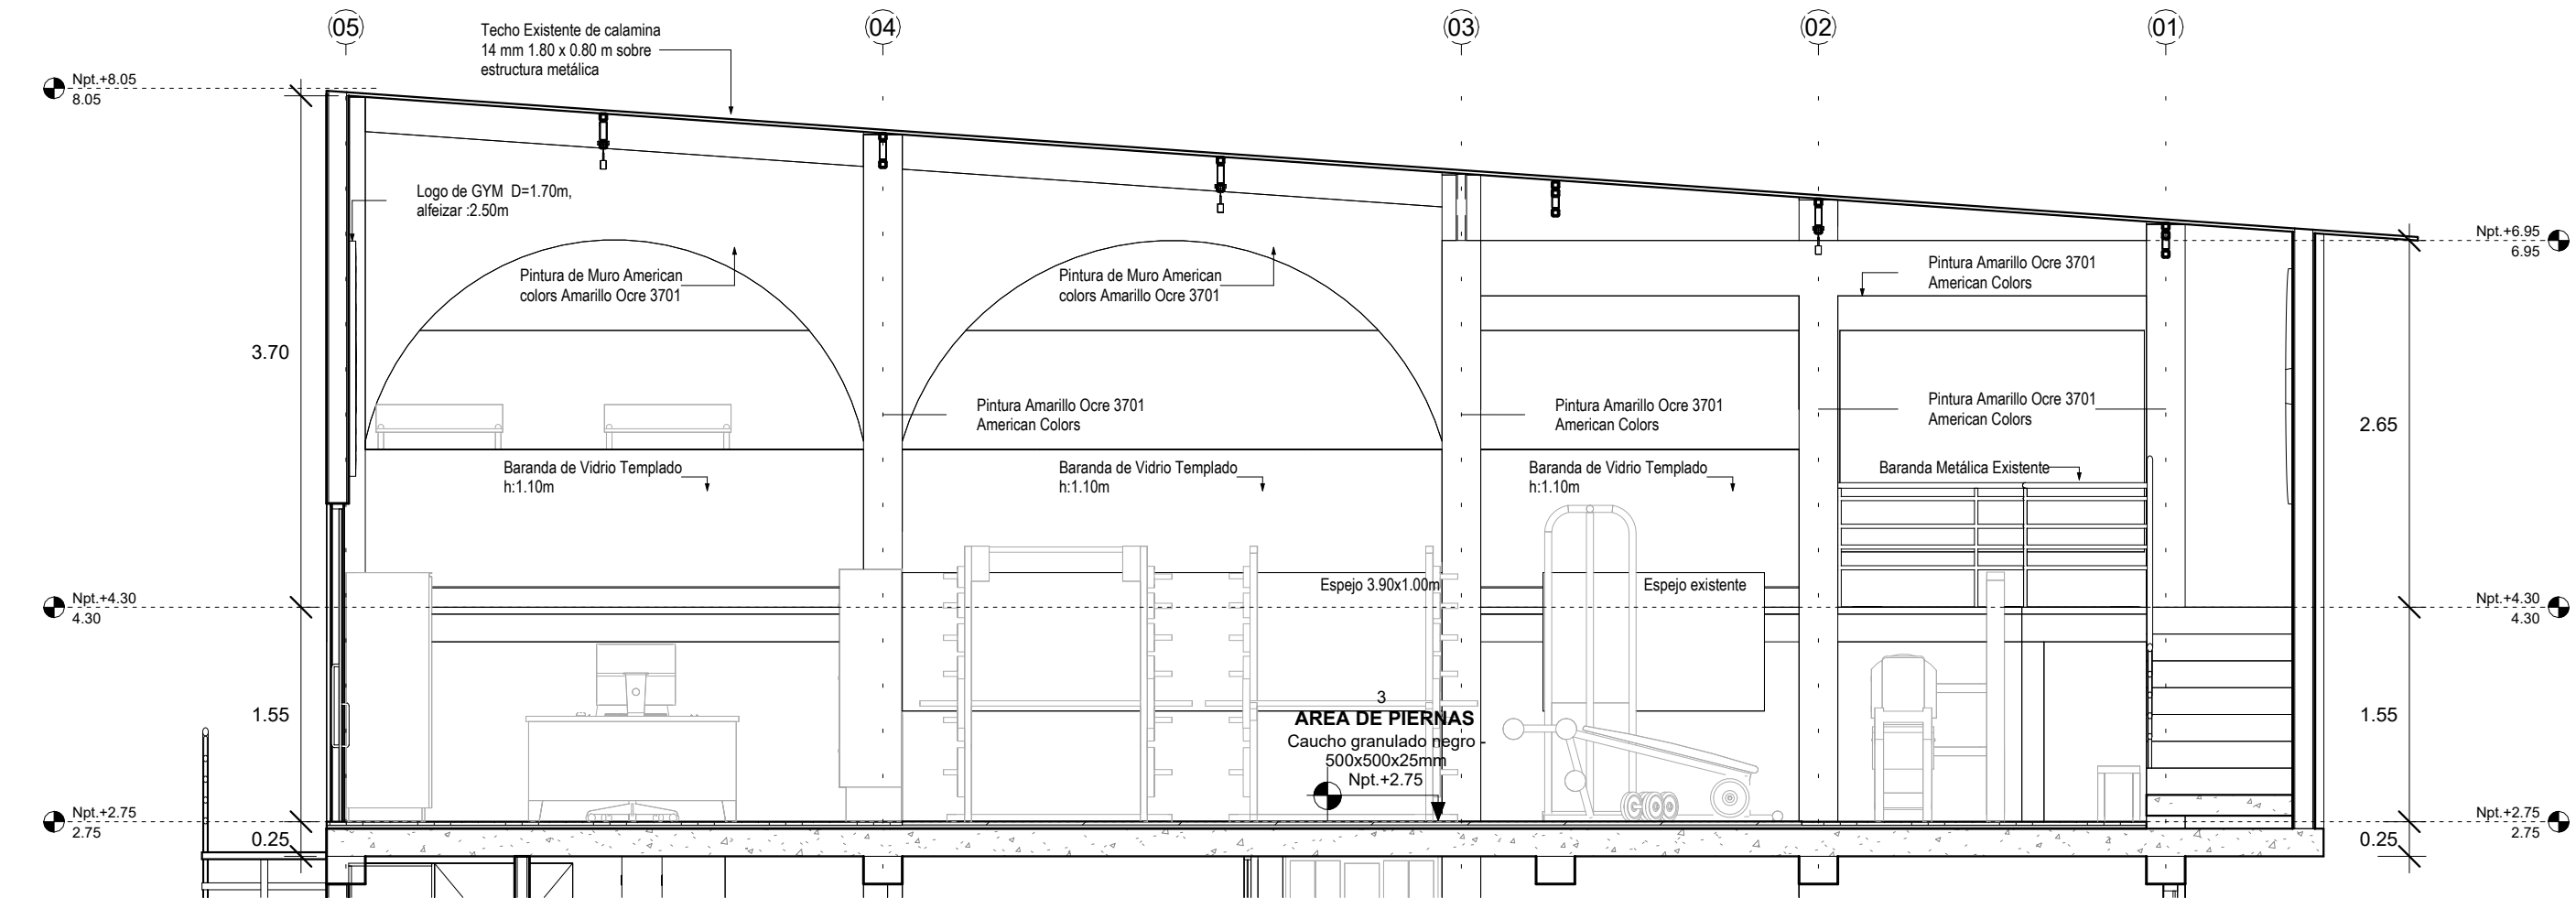


B CORTE LONGITUDINAL B-B
A-02 1:50

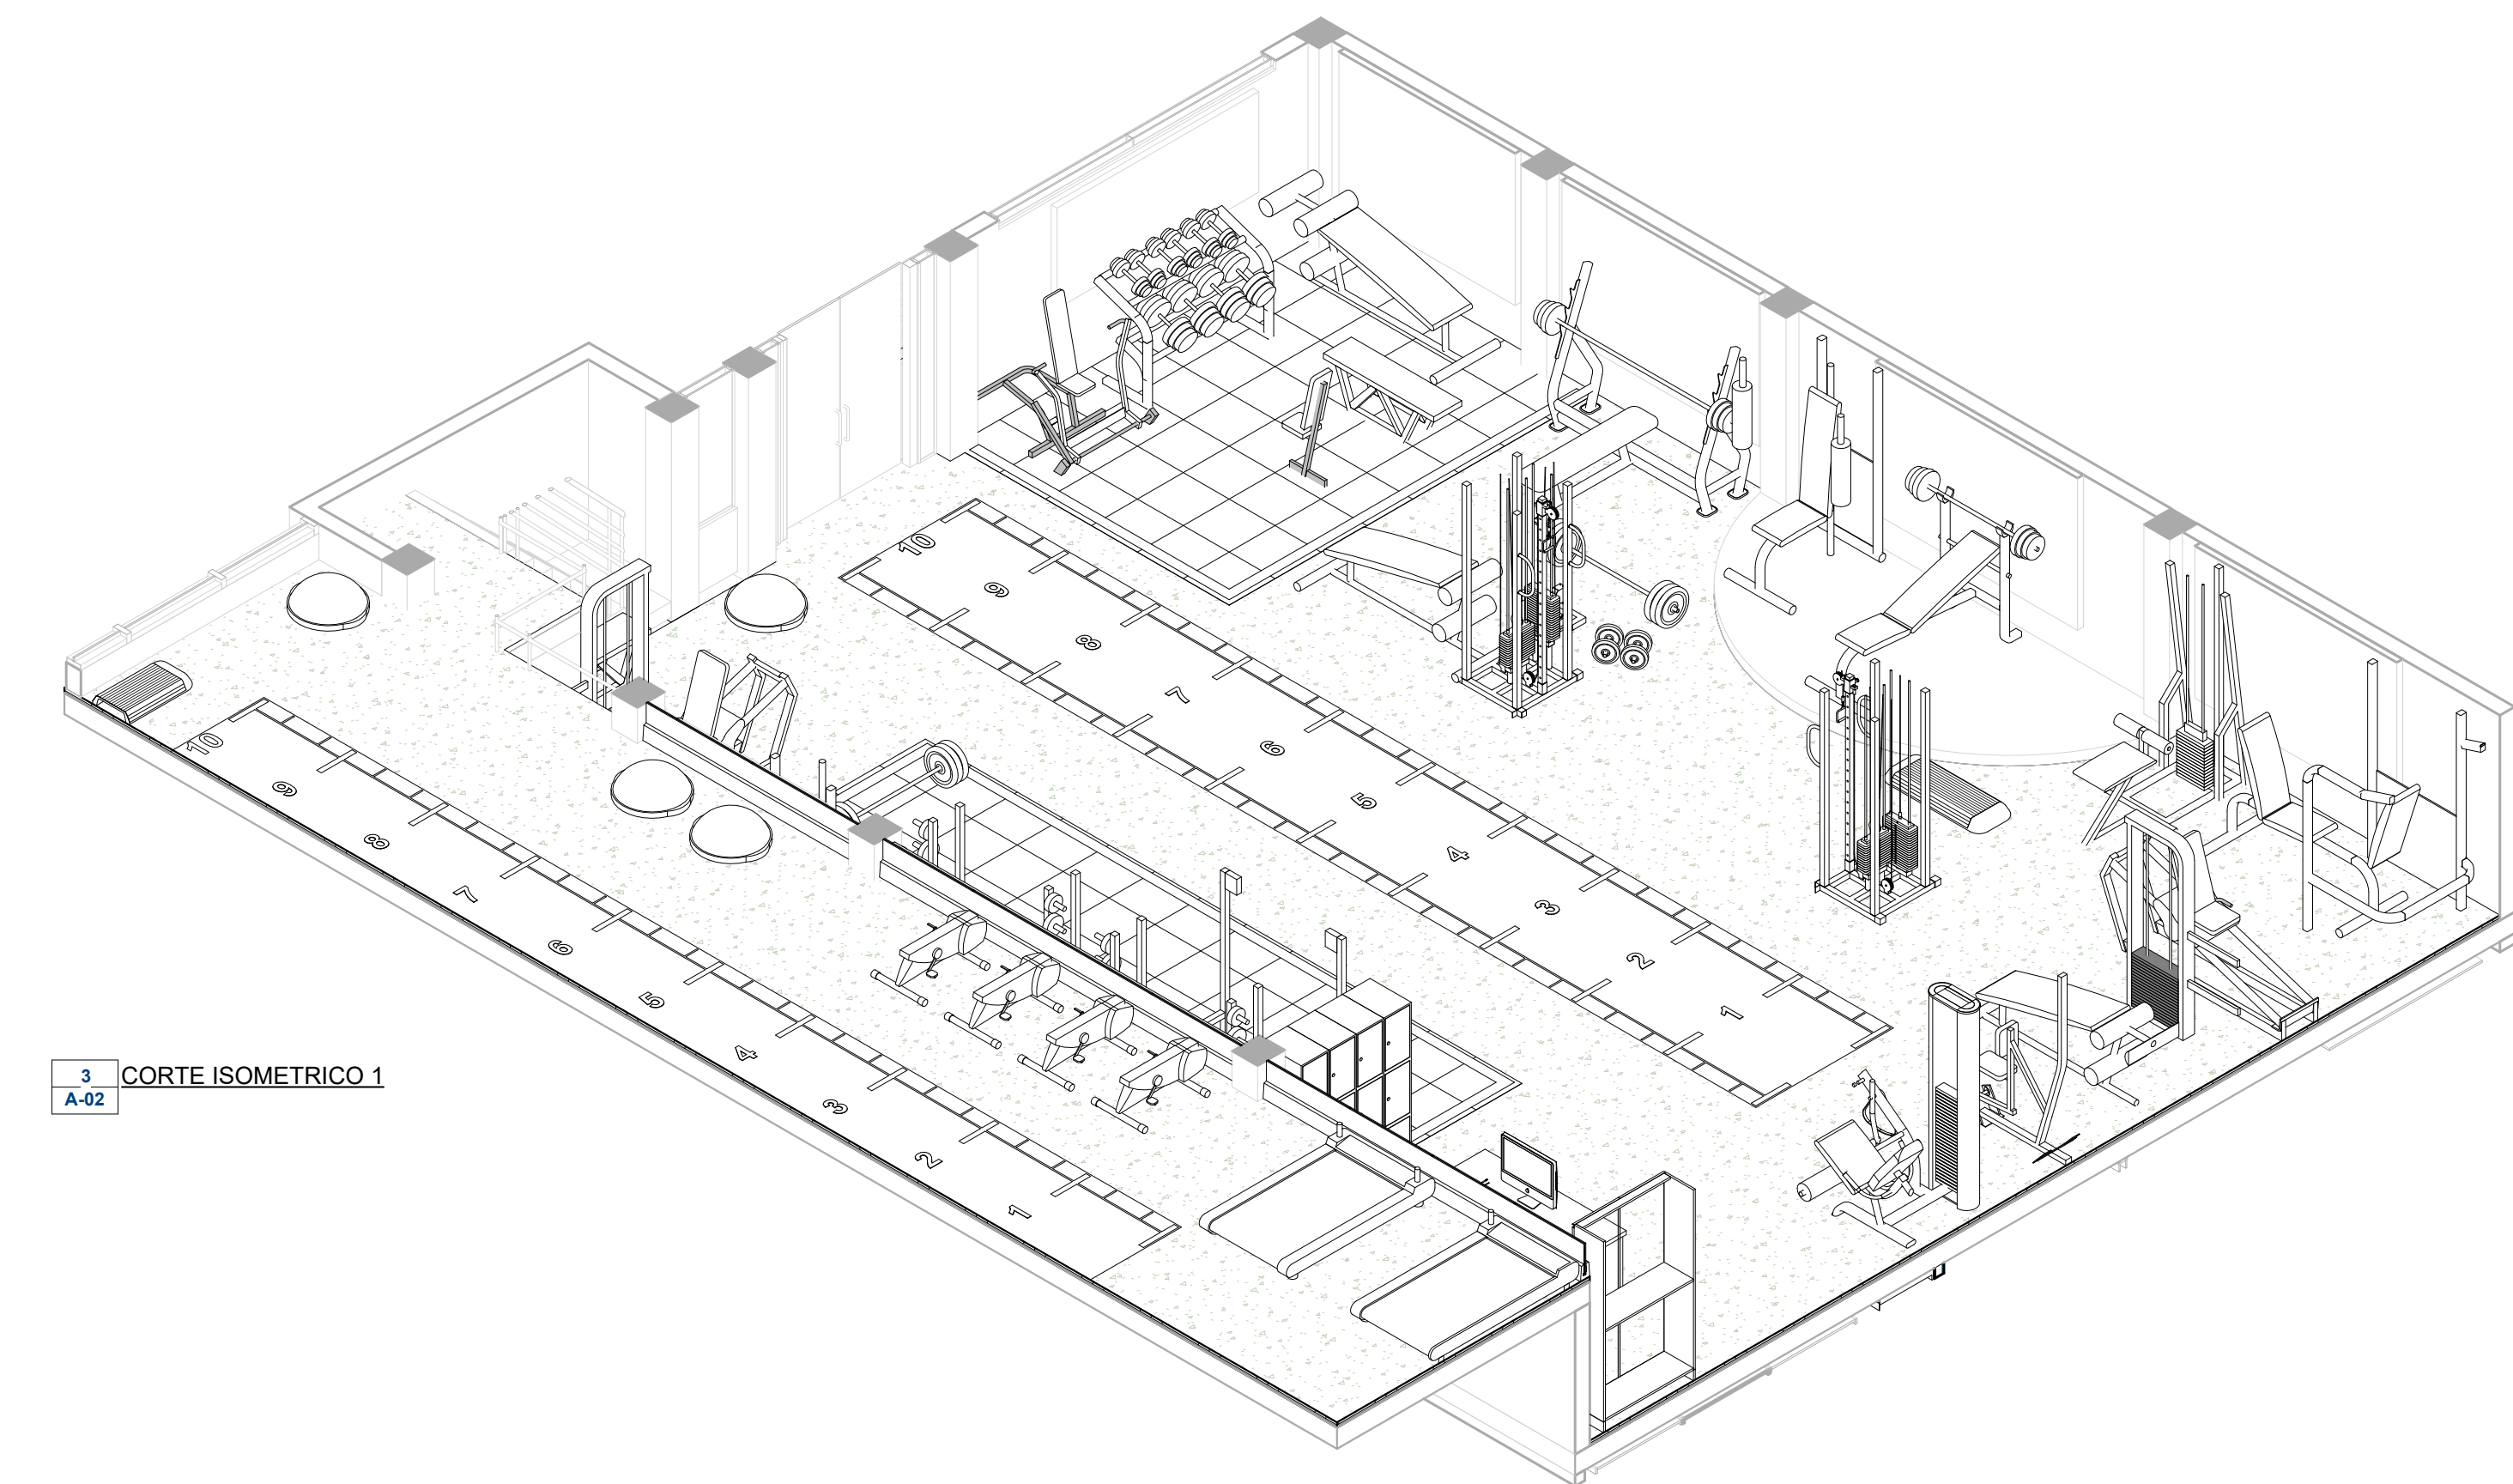


3 CORTE ISOMETRICO 1
A-02

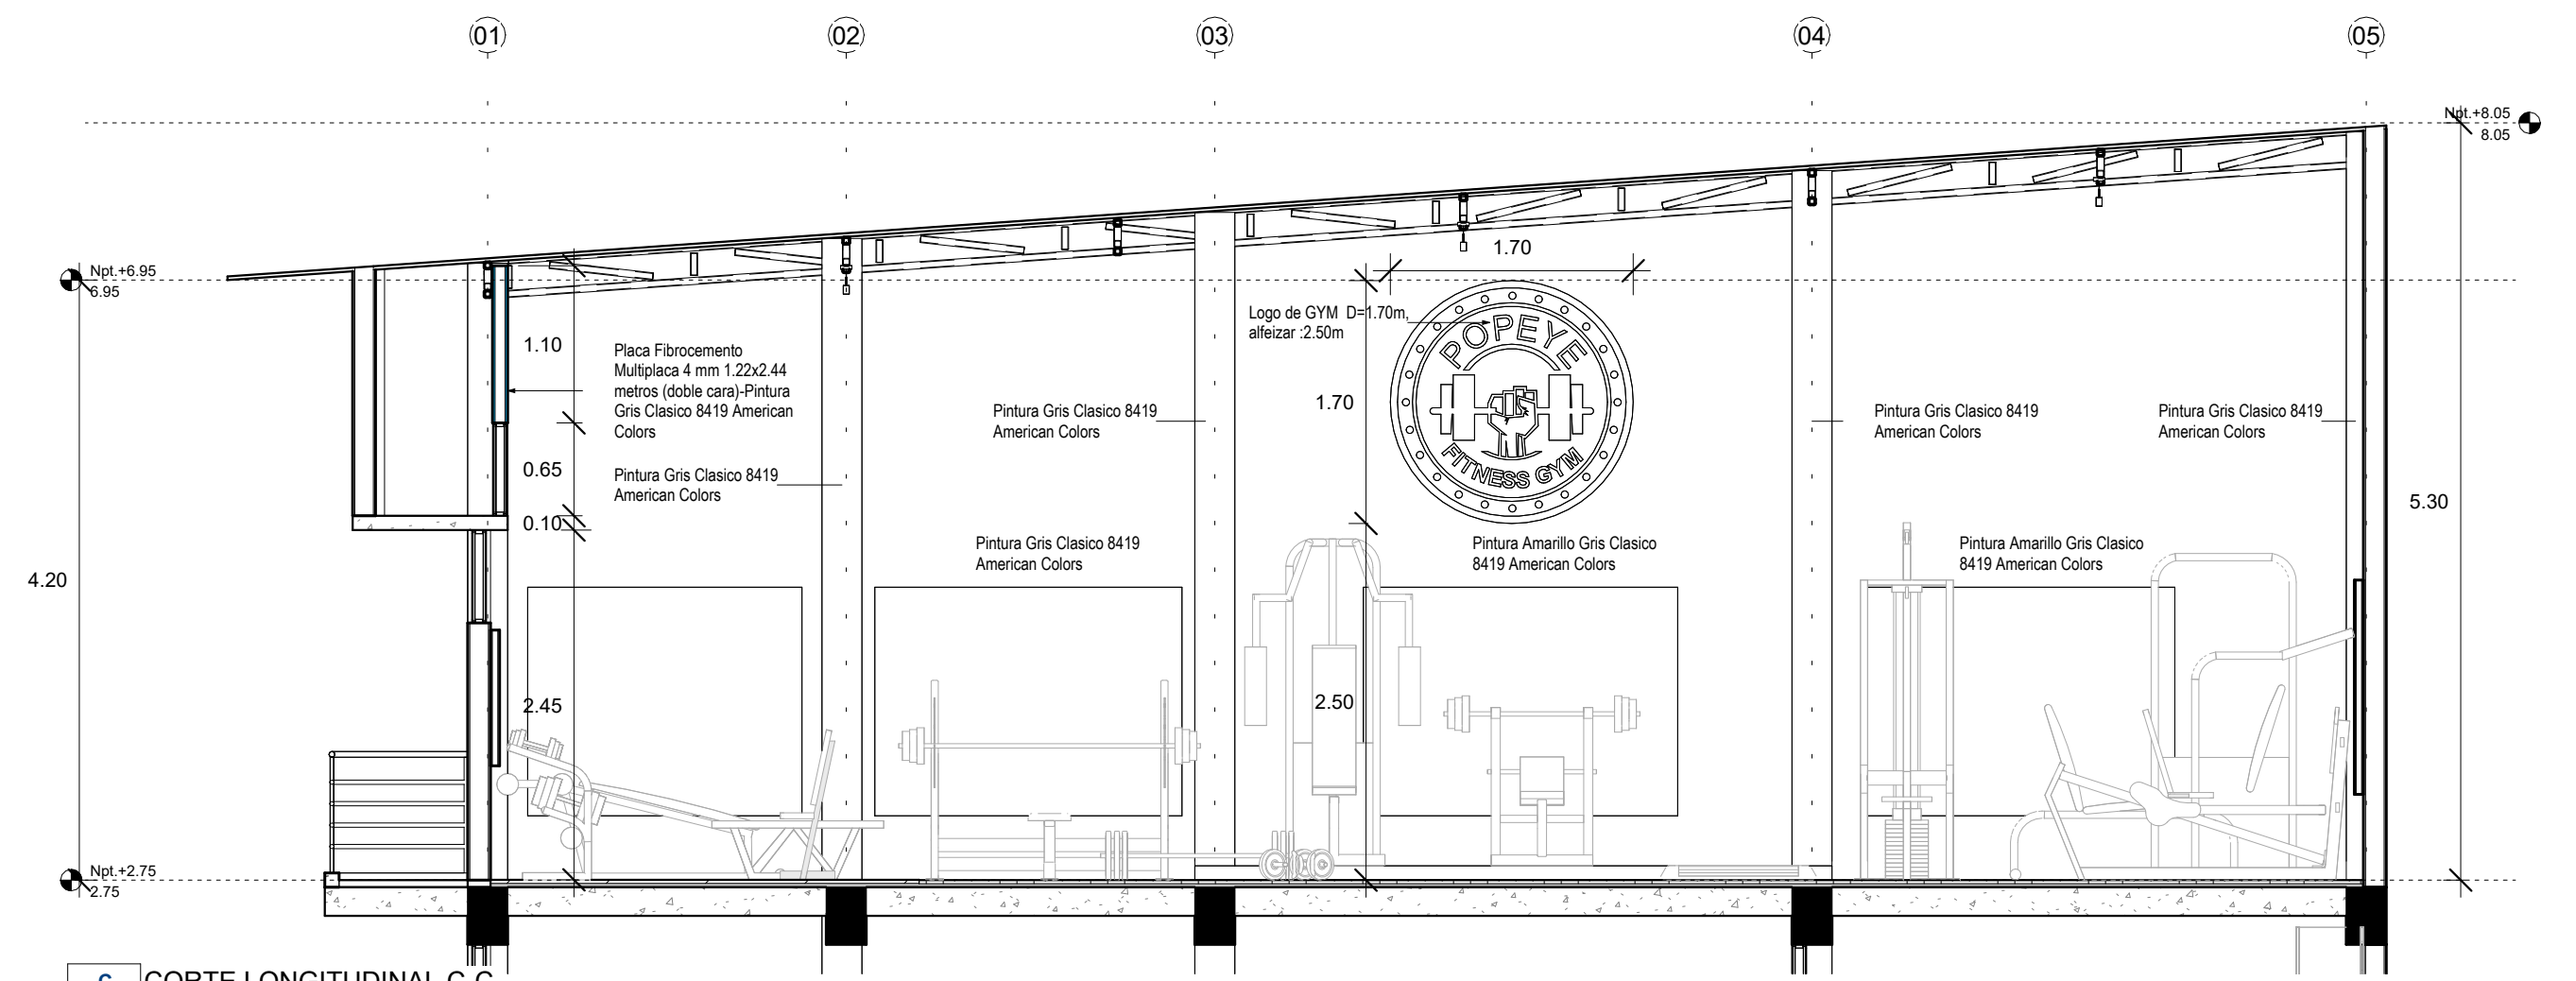

C CORTE LONGITUDINAL C-C
A-02 1:50

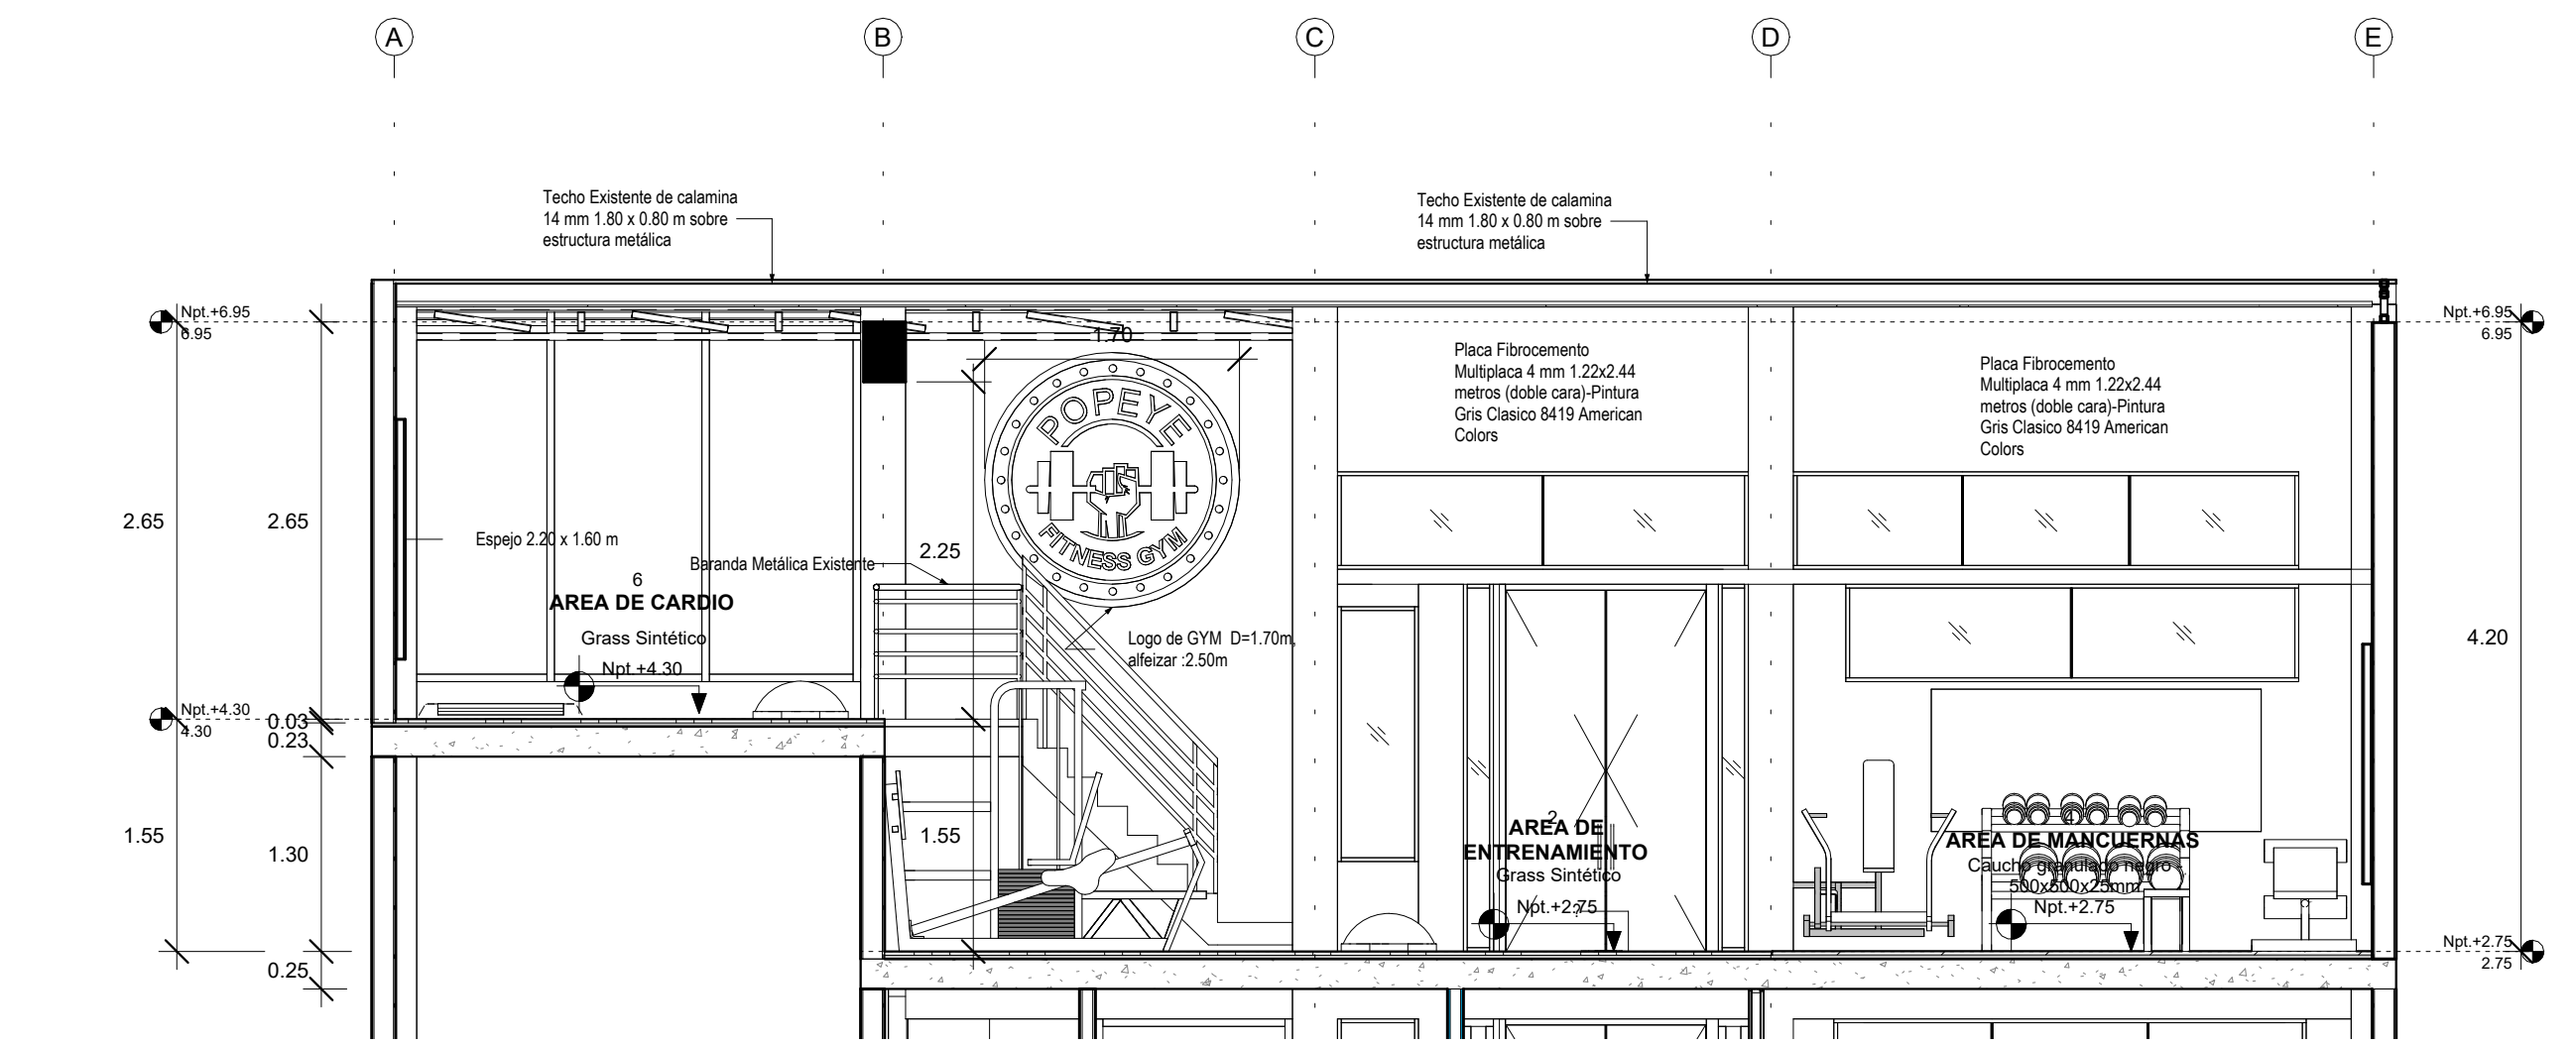


D CORTE TRANSVERSAL D-D
A-02 1:50

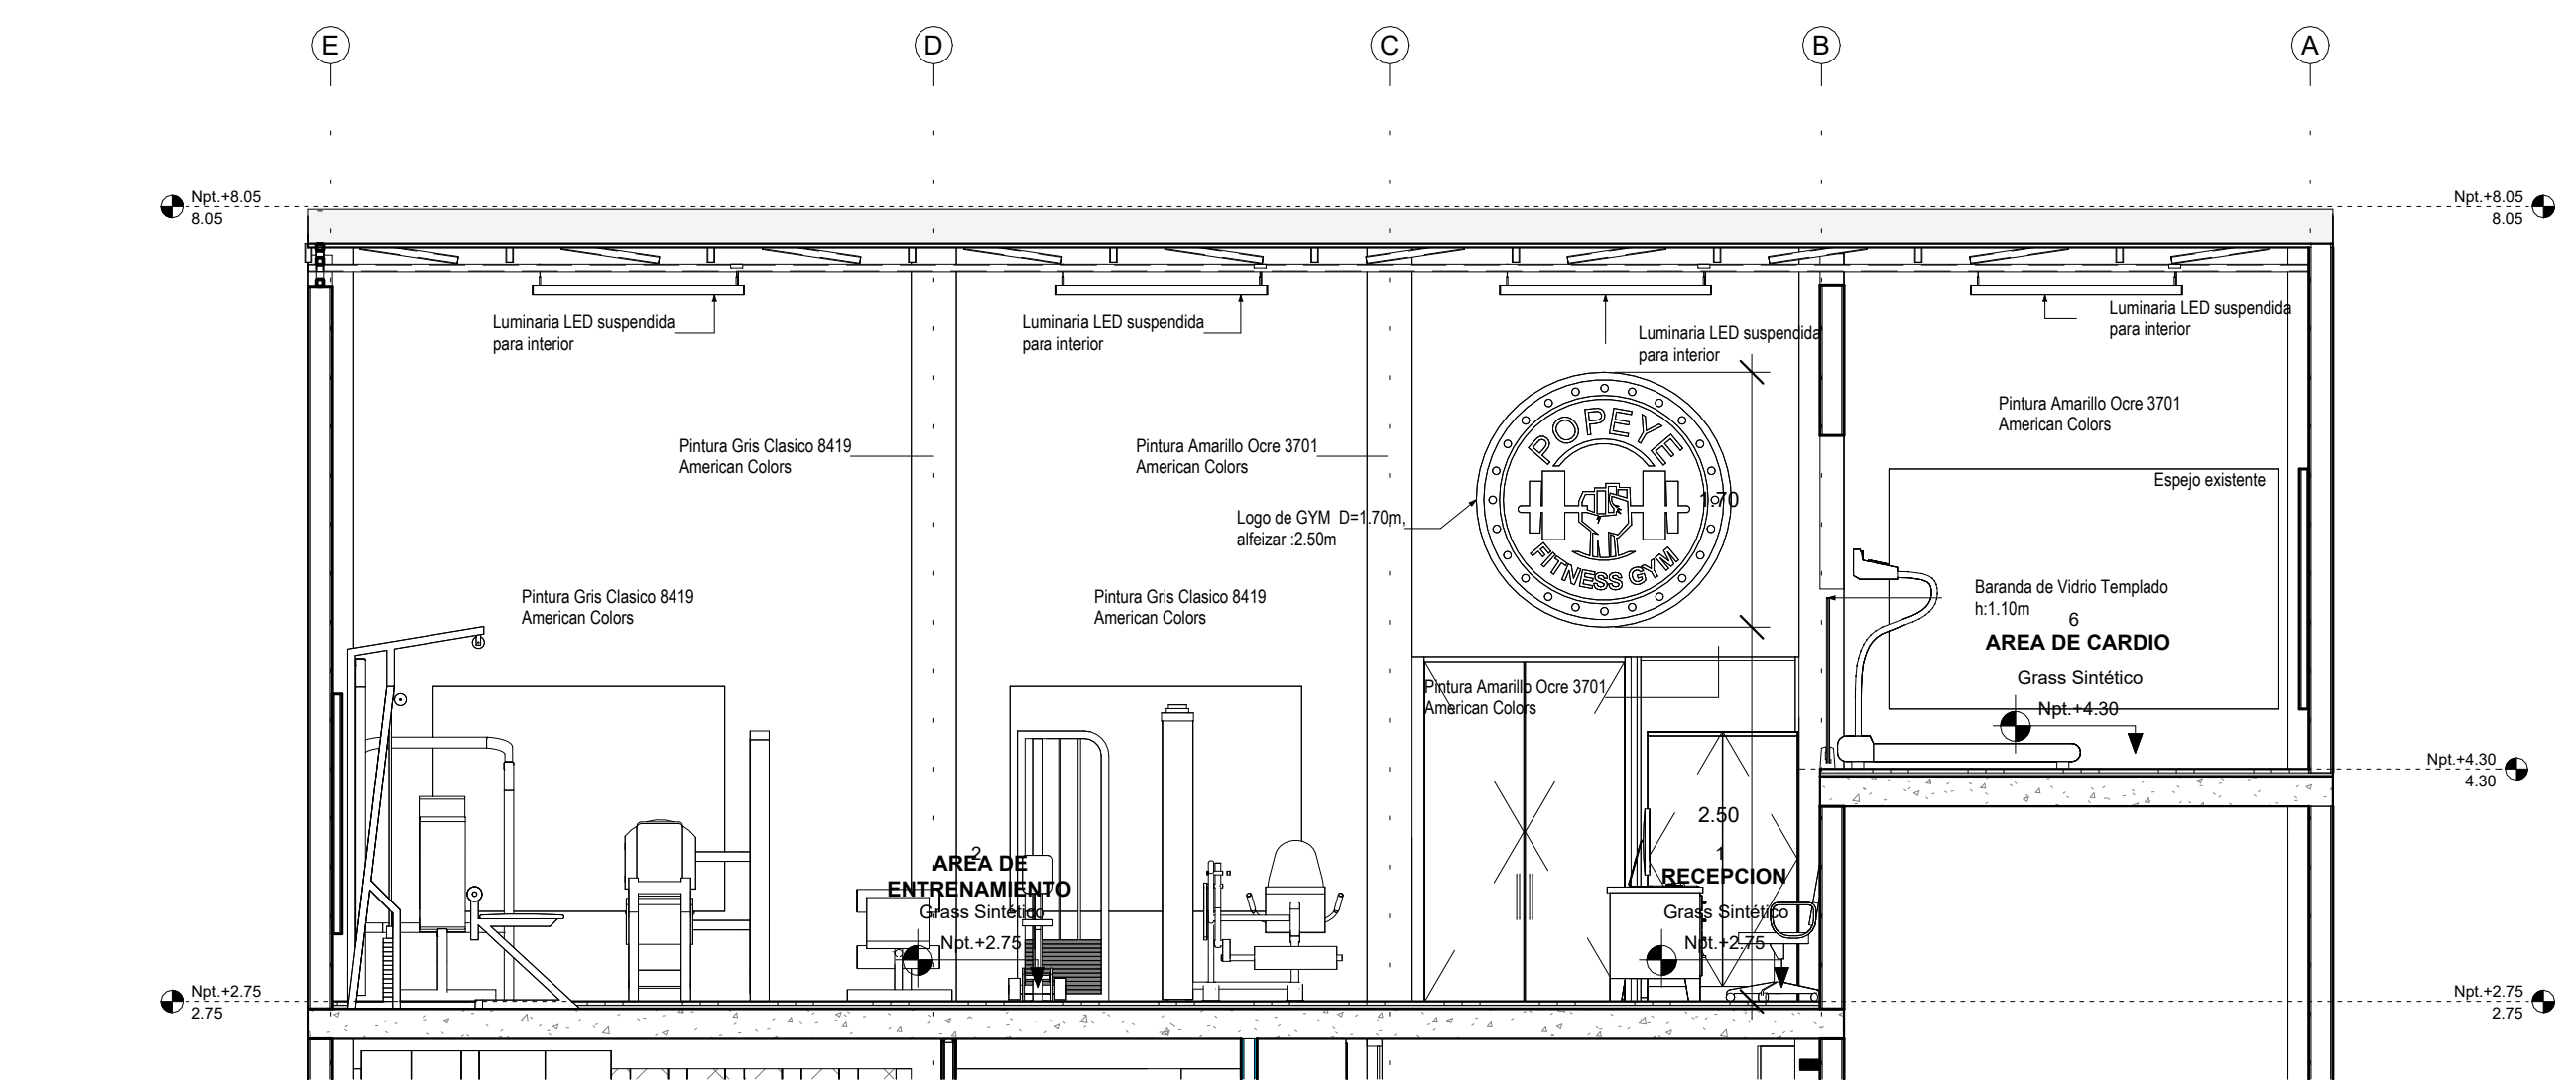


E CORTE TRANSVERSAL E-E
A-02 1:50


PROYECTO DE REMODELACION LOCAL COMERCIAL				
PROYECTO: REMODELACION GIMNASIO POPEYES GYM				
PLANO:	CORTES	FECHA:	MAR-2023	DIBUJO Y MODELADO BIM: A-02 Nelson Daza Donaires
ESPECIALIDAD:	ARQUITECTURA	ESC:	1:50	
DISEÑO:	NELSON DAZA DONAIRES	PLANO:		
UBICACION:	Jr. Santa Maria cdra. 01 Distrito: MOYOBAMBA	Provincia: MOYOBAMBA	Región: SAN MARTIN	

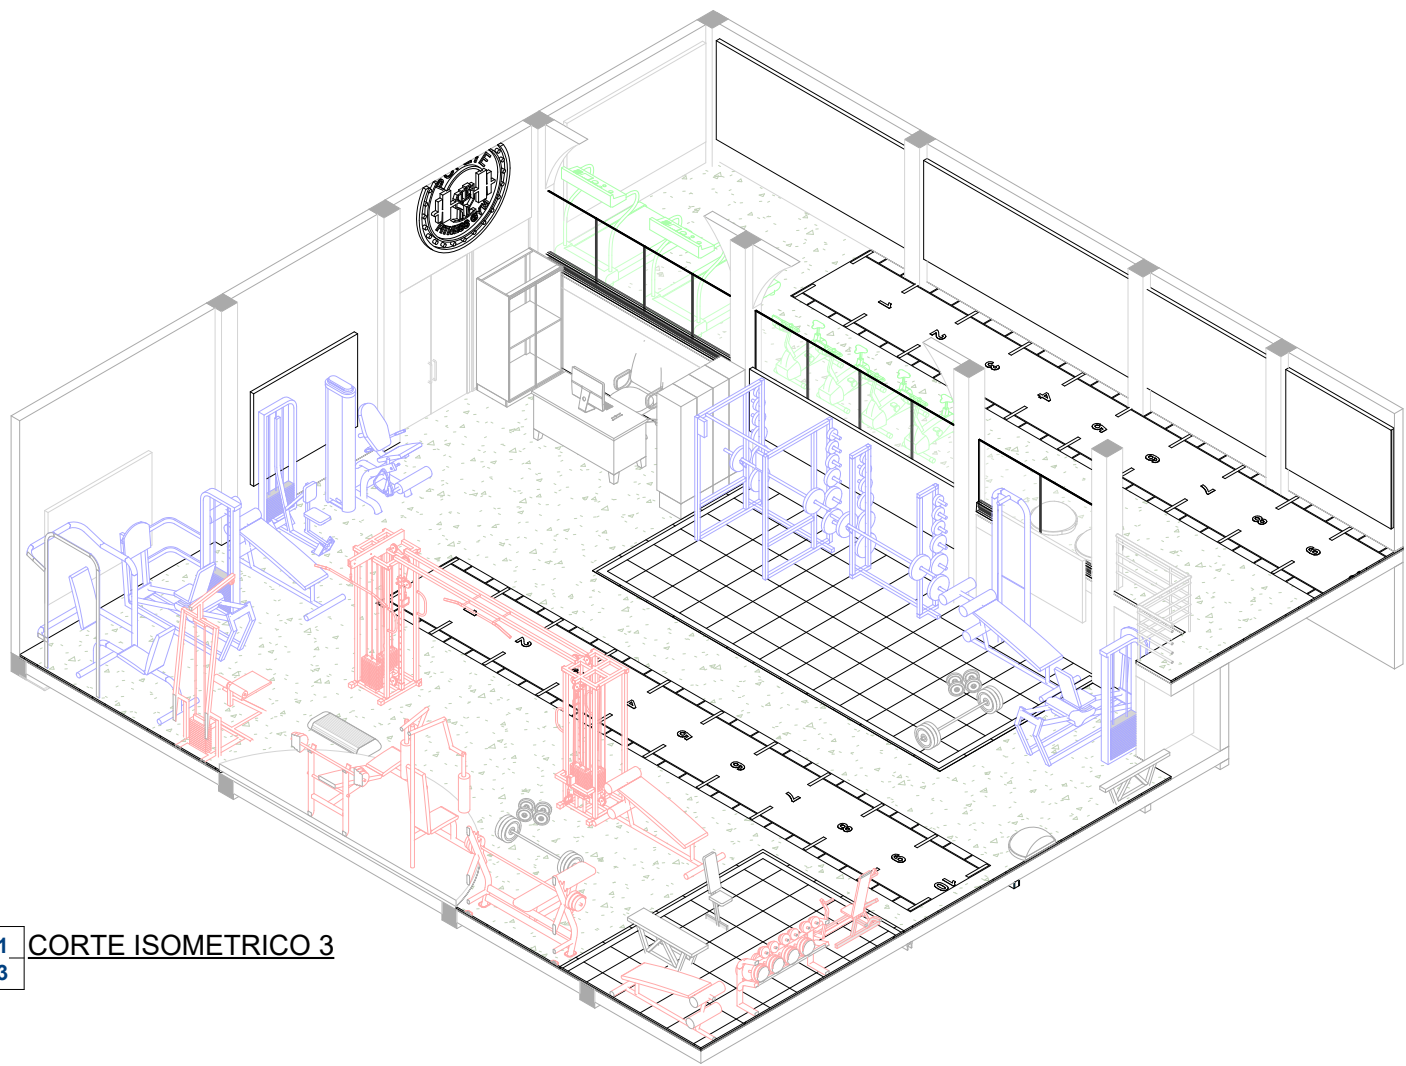

IS01 CORTE ISOMETRICO 3
A-03

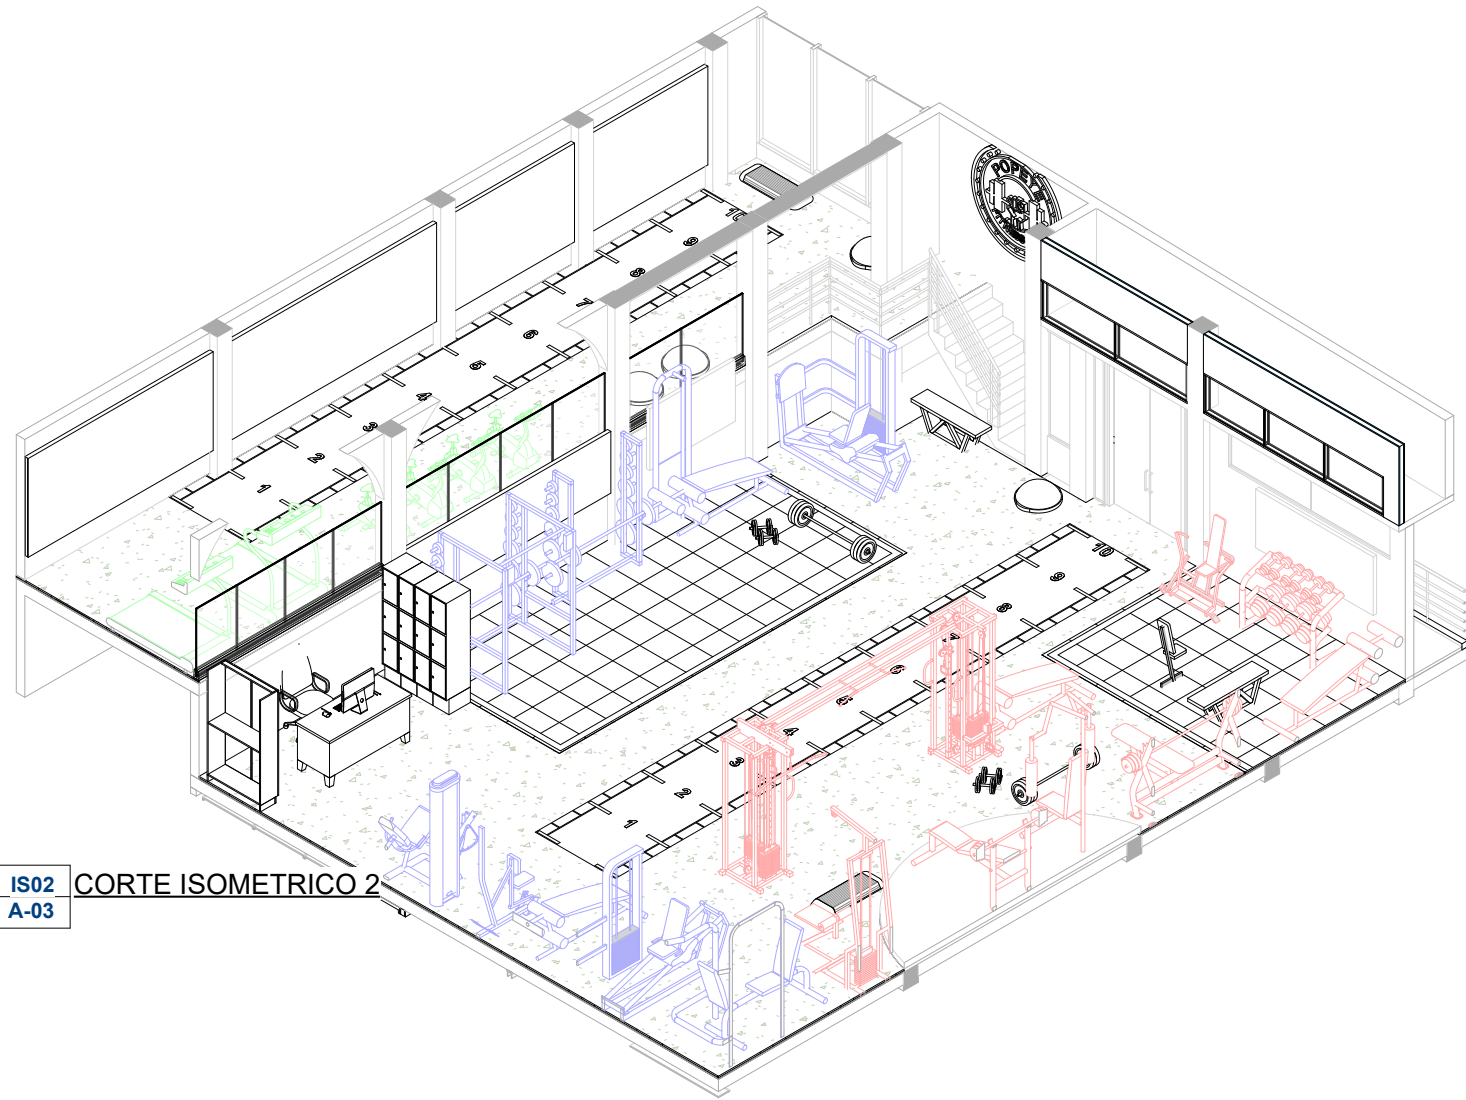

IS02 CORTE ISOMETRICO 2
A-03

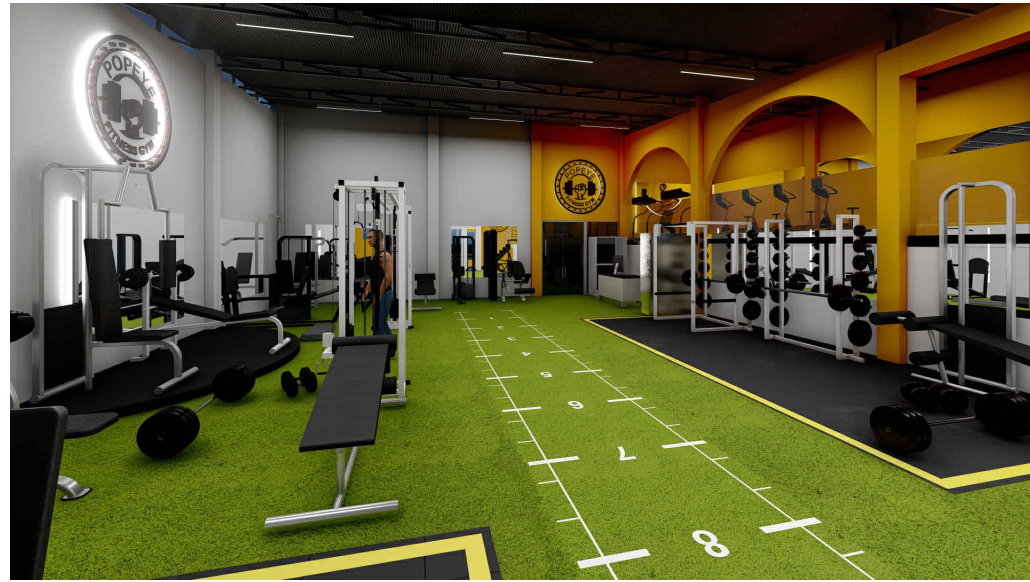

1 01 AREA DE MAQUINAS
A-03 1 : 250



3 03 TREN INFERIOR
A-03 1 : 250



6 06 VISTA GENERAL
A-03 1 : 250



2 02 INGRESO
A-03 1 : 250



4 04 TREN SUPERIOR
A-03 1 : 250



5 05 AREA DE CARDIO
A-03 1 : 250

PROYECTO DE REMODELACION LOCAL COMERCIAL				
PROYECTO: REMODELACION GIMNASIO POPEYES GYM				
PLANO:	CORTES ISOMETRICOS/RENDERS	FECHA:	MAR-2023	BIM MANAGER:
ESPECIALIDAD:	ARQUITECTURA	ESC:	1 : 250	
DISEÑO:	NELSON DAZA DONAIRES	PLANO:		
UBICACION:	Jr. Santa María cdra. 01			
	Distrito: MOYOBAMBA	Provincia: MOYOBAMBA	Región: SAN MARTIN	
A-03				Nelson Daza Donaires