


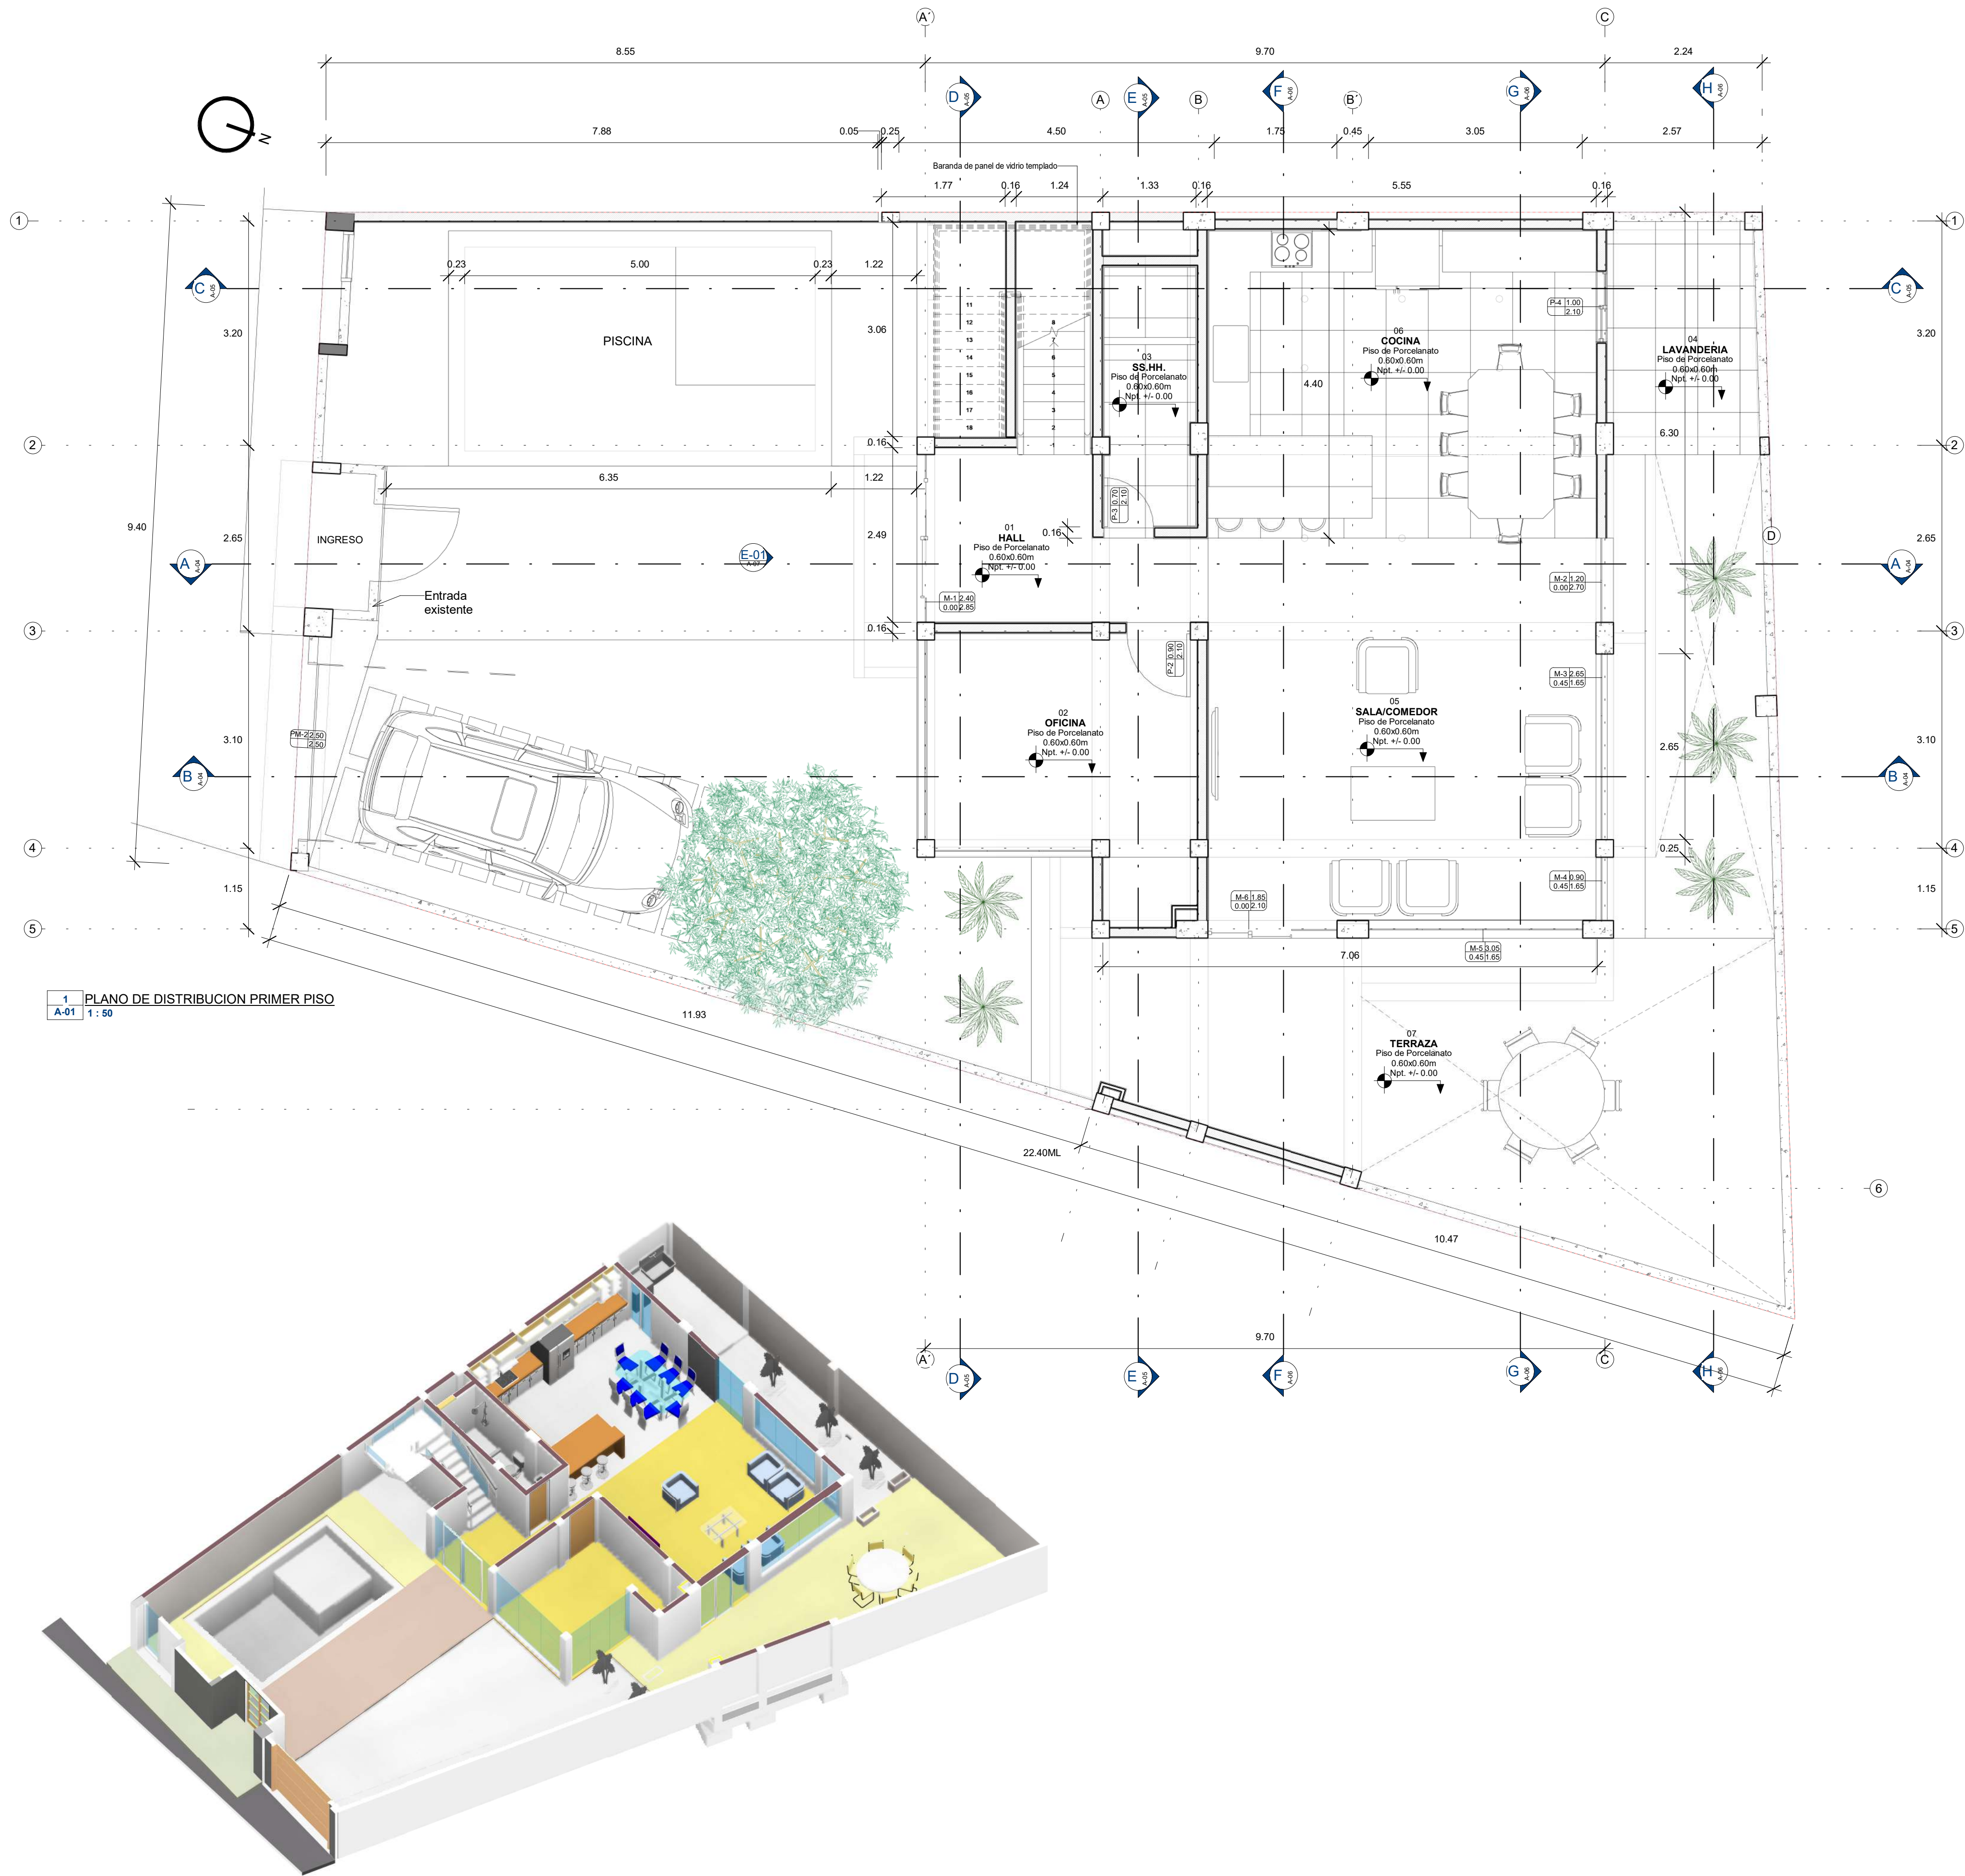

1 PLANO DE DISTRIBUCION PRIMER PISO
A-01 1:50

2 ISOMETRICO PRIMER PISO
A-01

Tabla de planificación de áreas (Area Techada)	
Nombre	Área
Área 1er Piso	130.260
Área 2do Piso	111.807
Área 3er Piso	143.265
Total general: 4	385.332

CUADRO DE VANOS PUERTAS -PRIMER PISO				
COD:	Anchura	Altura	Total	Nivel
P-1	1.10	2.10	1	Npt. +/- 0.00
P-2	0.90	2.10	1	Npt. +/- 0.00
P-3	0.70	2.10	1	Npt. +/- 0.00
P-4	1.00	2.10	2	Npt. +/- 0.00
Npt. +/- 0.00: 5			5	
Total general: 5			5	

CARPINTERIA METALICA - PRIMER PISO					
COD.	Largo	Alto	Alfeizar	Área	Nivel
M-1	2.85	2.85	0.00	8.12	Npt. +/- 0.00
M-1	2.40	2.85	0.00	6.83	Npt. +/- 0.00
M-1	2.25	2.85	0.00	6.41	Npt. +/- 0.00
M-2	1.20	2.70	0.00	3.24	Npt. +/- 0.00
M-2	1.20	2.70	0.00	3.24	Npt. +/- 0.00
M-3	2.65	1.65	0.45	4.37	Npt. +/- 0.00
M-3	2.65	1.65	0.45	4.37	Npt. +/- 0.00
M-4	0.90	1.65	0.45	1.49	Npt. +/- 0.00
M-5	3.05	1.65	0.45	5.03	Npt. +/- 0.00
M-6	1.85	2.10	0.00	3.89	Npt. +/- 0.00
Npt. +/- 0.00: 10					
Total general: 10					

PROGRAMA ARQUITECTONICO			
N°	Nombre	Acabado del suelo	Área
01	HALL	Piso de Porcelanato 0.60x0.60m	7.86
02	OFICINA	Piso de Porcelanato 0.60x0.60m	13.18
03	SS.HH.	Piso de Porcelanato 0.60x0.60m	4.88
04	LAVANDERIA	Piso de Porcelanato 0.60x0.60m	7.01
05	SALA/COMEDOR	Piso de Porcelanato 0.60x0.60m	30.21
06	COCINA	Piso de Porcelanato 0.60x0.60m	24.49
07	TERRAZA	Piso de Porcelanato 0.60x0.60m	39.81
Npt. +/- 0.00: 7			127.44
08	BIBLIOTECA	Piso de Porcelanato 0.60x0.60m	17.62
09	OFICINA	Piso de Porcelanato 0.60x0.60m	18.91
10	HABITACION PRINCIPAL	Piso de Porcelanato 0.60x0.60m	32.10
11	TERRAZA	Piso de Porcelanato 0.60x0.60m	6.47
12	SS.HH. 01	Piso de Porcelanato 0.60x0.60m	6.54
13	BALCON 01	Piso de Porcelanato 0.60x0.60m	6.72
14	HABITACION 02	Piso de Porcelanato 0.60x0.60m	17.43
15	SS.HH. 02	Piso de Porcelanato 0.60x0.60m	3.32
16	TERRAZA	Piso de Porcelanato 0.60x0.60m	6.65
Npt.+3.30: 9			105.75
19	ESTAR	Piso de Porcelanato 0.60x0.60m	13.89
20	GYMNASIO	Piso de Porcelanato 0.60x0.60m	25.67
21	SS.HH.	Piso de Porcelanato 0.60x0.60m	3.18
22	SALON	Piso de Porcelanato 0.60x0.60m	43.91
Npt.+6.60: 4			86.65
Total general: 20			319.84

EDIFICIO UNIFAMILIAR

PROYECTO: VIVIENDA UNIFAMILIAR

PLANO: PLANO DE DISTRIBUCION PRIMER PISO

ESPECIALIDAD: ARQUITECTURA

DISEÑO: NELSON DAZA DONAIRES

UBICACION: Jr. Actual C-01, Barrio de Suchiche
Distrito: TARAPOTO
Provincia: SAN MARTIN
Región: SAN MARTIN

FECHA: NOV-2021


ESC: 1:50

PLANO:

A-01

DIBUJO Y MODELADO BIM:


Nelson Daza Donaires

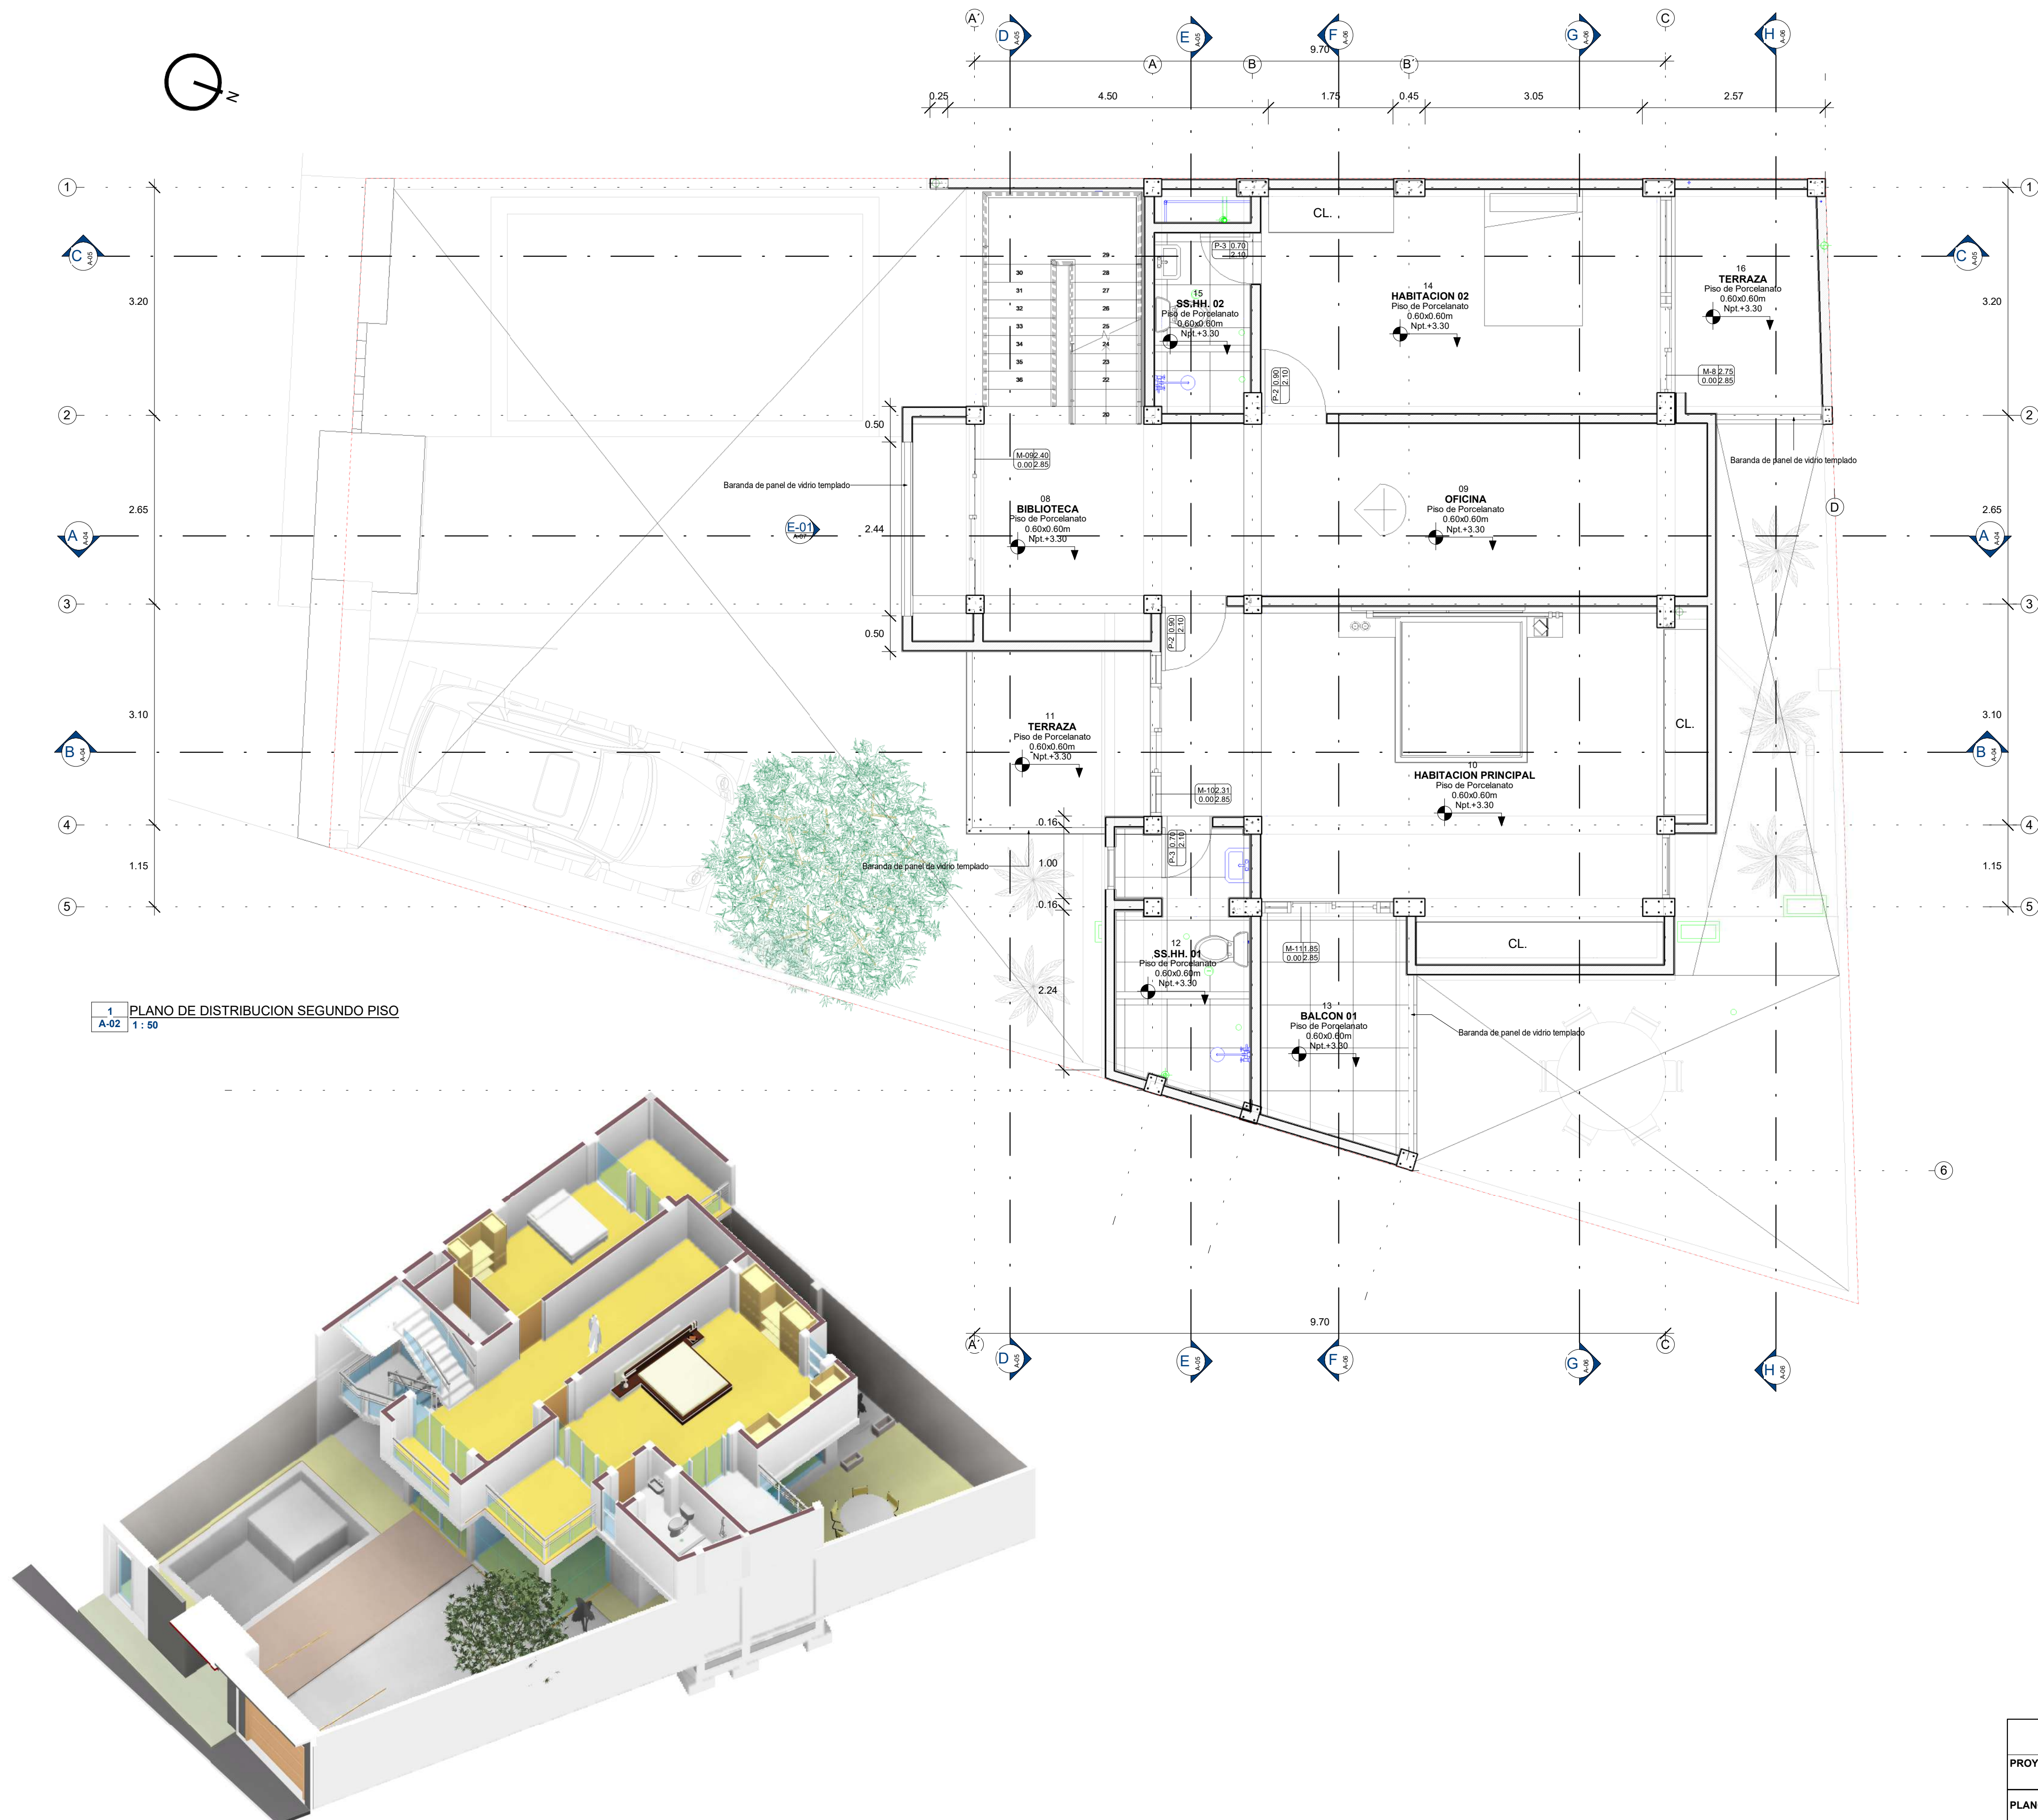

1 PLANO DE DISTRIBUCION SEGUNDO PISO
A-02 1:50

2 ISOMETRICO SEGUNDO PISO
A-02

EDIFICIO UNIFAMILIAR				
PROYECTO:		VIVIENDA UNIFAMILIAR		
PLANO:	PLANO DE DISTRIBUCION SEGUNDO PISO		FECHA:	NOV-2021
ESPECIALIDAD:	ARQUITECTURA		ESC:	1 : 50
DISEÑO:	NELSON DAZA DONAIRES		PLANO:	A-02
UBICACION:		Jr. Actual C-01, Barrio de Suchiche		
Districto:	TARAPOTO	Provincia:	SAN MARTIN	
		Region:	SAN MARTIN	Nelson Daza Donaires

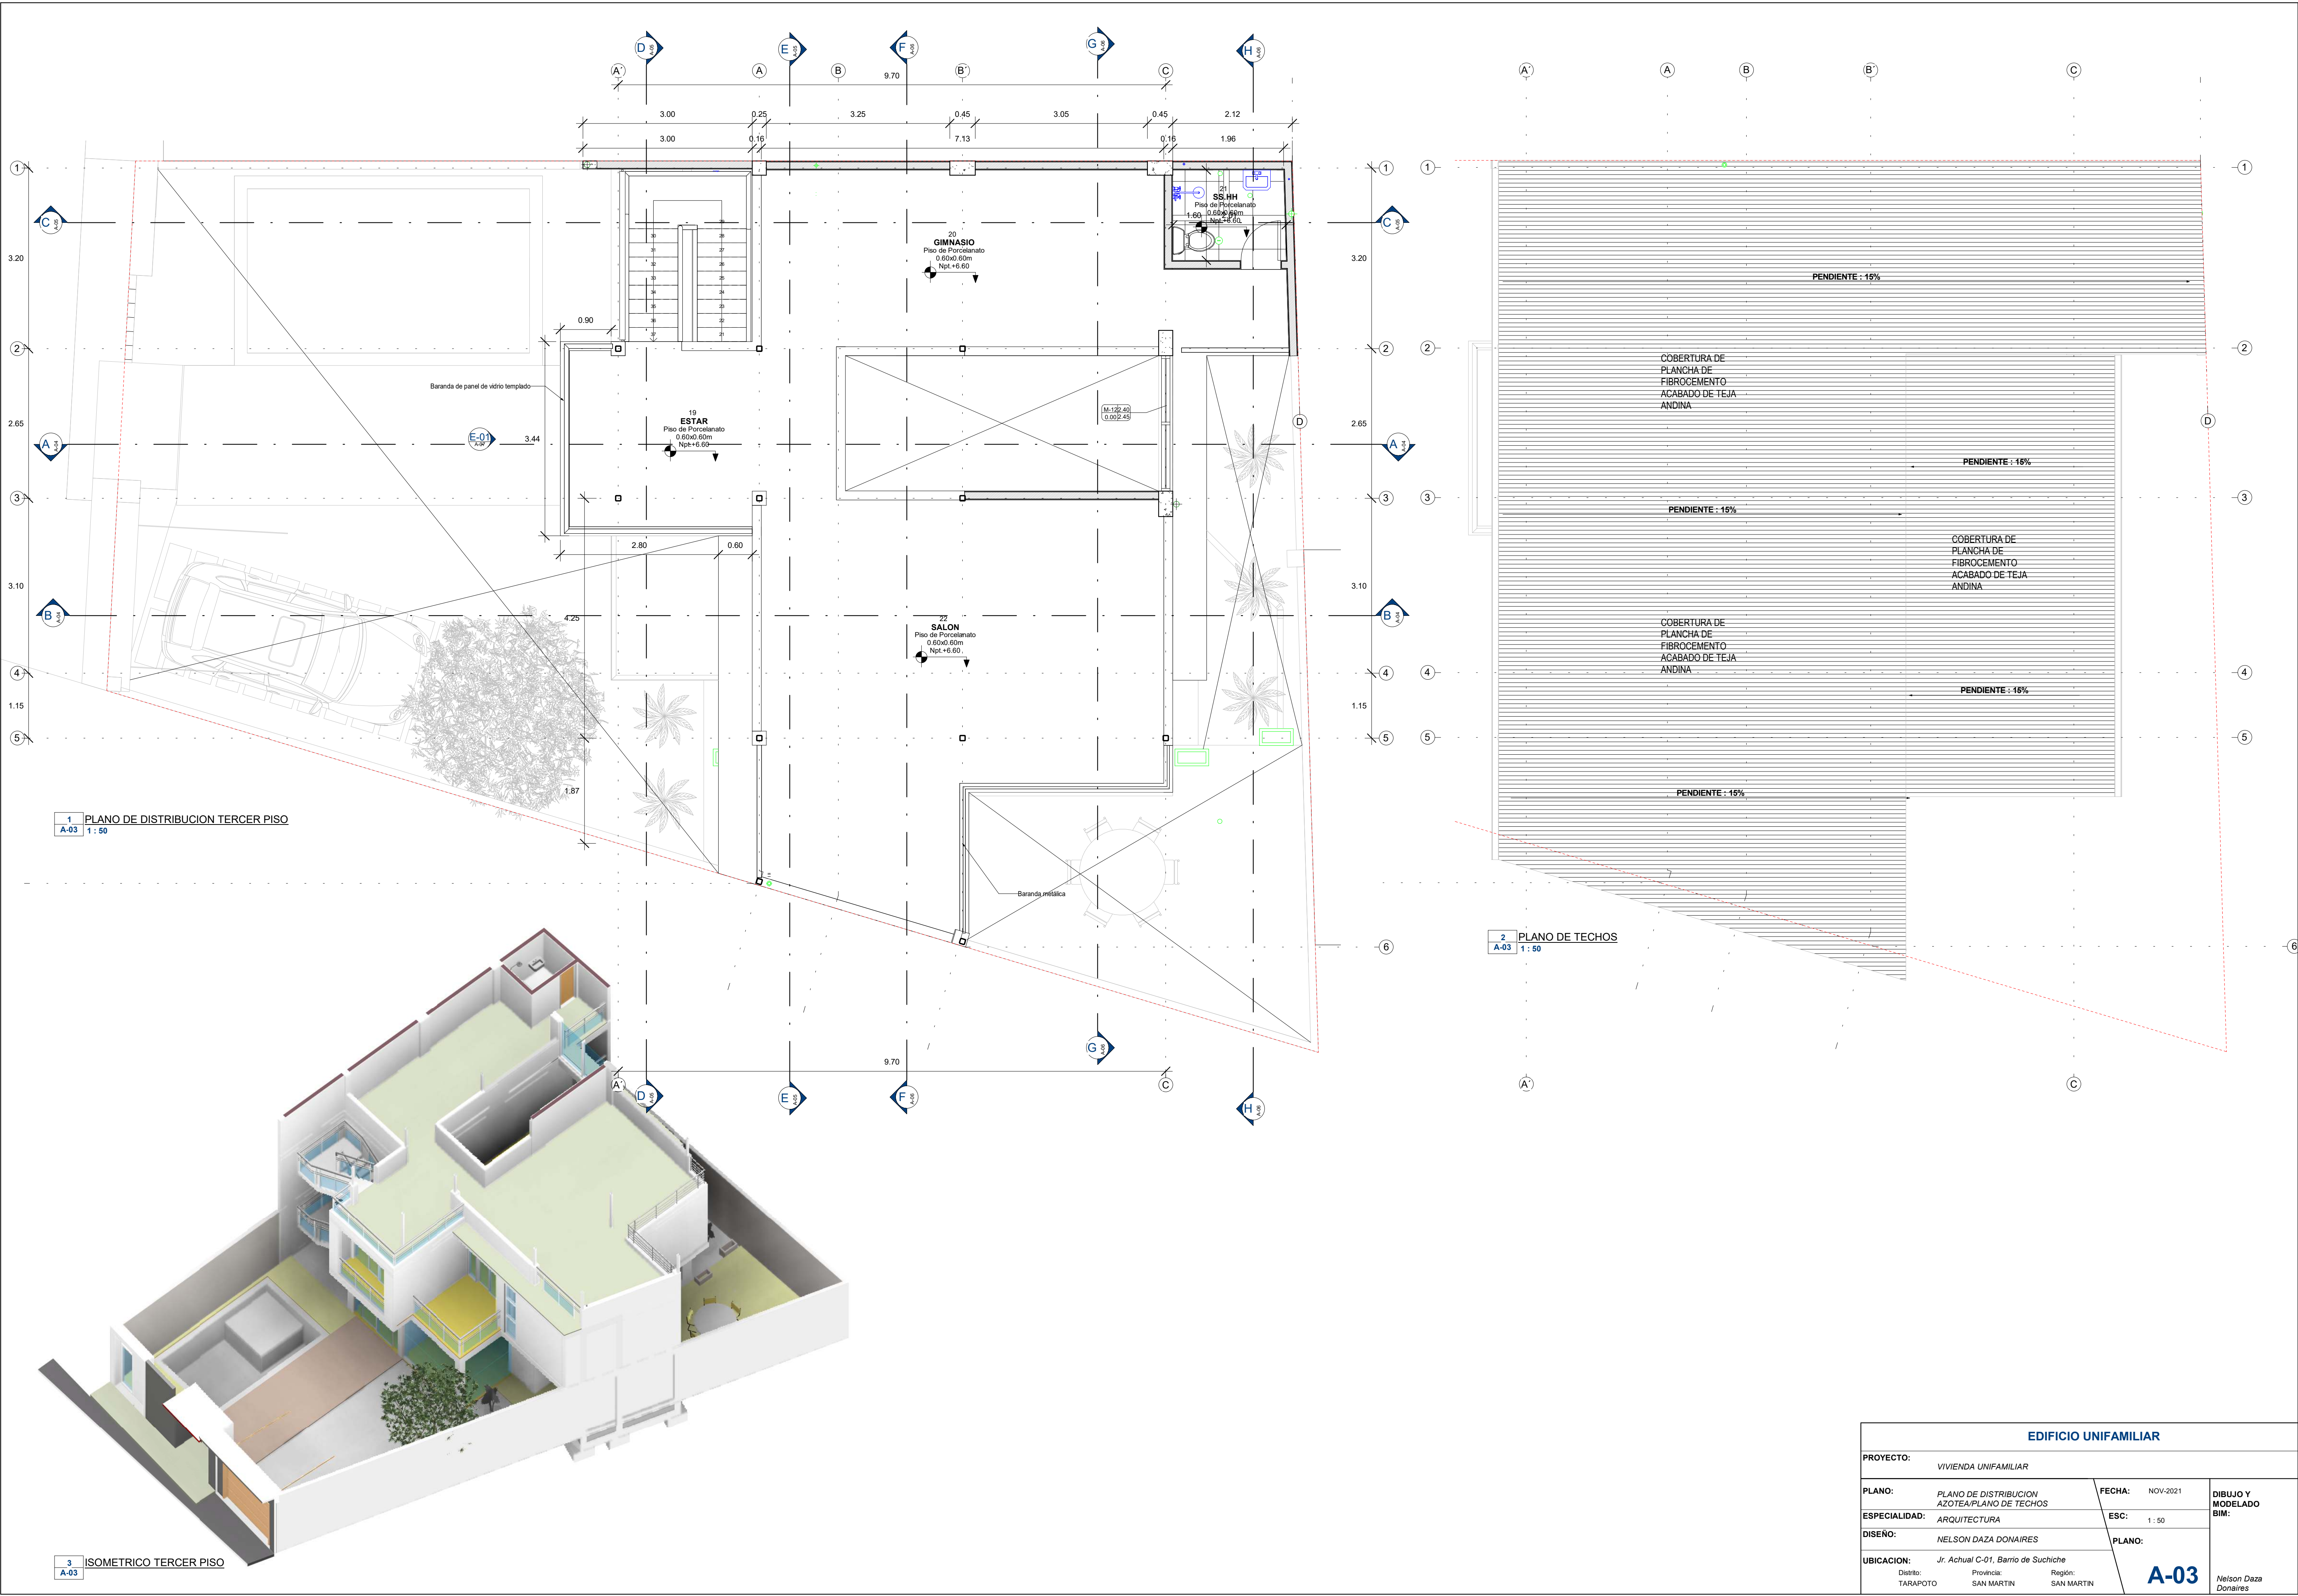


1 PLANO DE DISTRIBUCION TERCER PISO
A-03 1:50


2 PLANO DE TECHOS
A-03 1:50

3 ISOMETRICO TERCER PISO
A-03

EDIFICIO UNIFAMILIAR				
PROYECTO:		VIVIENDA UNIFAMILIAR		
PLANO:	PLANO DE DISTRIBUCION AZOTEA/PLANO DE TECHOS	FECHA:	NOV-2021	DIBUJO Y MODELADO BIM:
ESPECIALIDAD:	ARQUITECTURA	ESC:	1:50	
DISEÑO:	NELSON DAZA DONAIRES	PLANO:		
UBICACION:		Jr. Actual C-01, Barrio de Suchiche		A-03 Nelson Daza Donaires
Districto:	TARAPOTO	Provincia:	SAN MARTIN	
		Región:	SAN MARTIN	

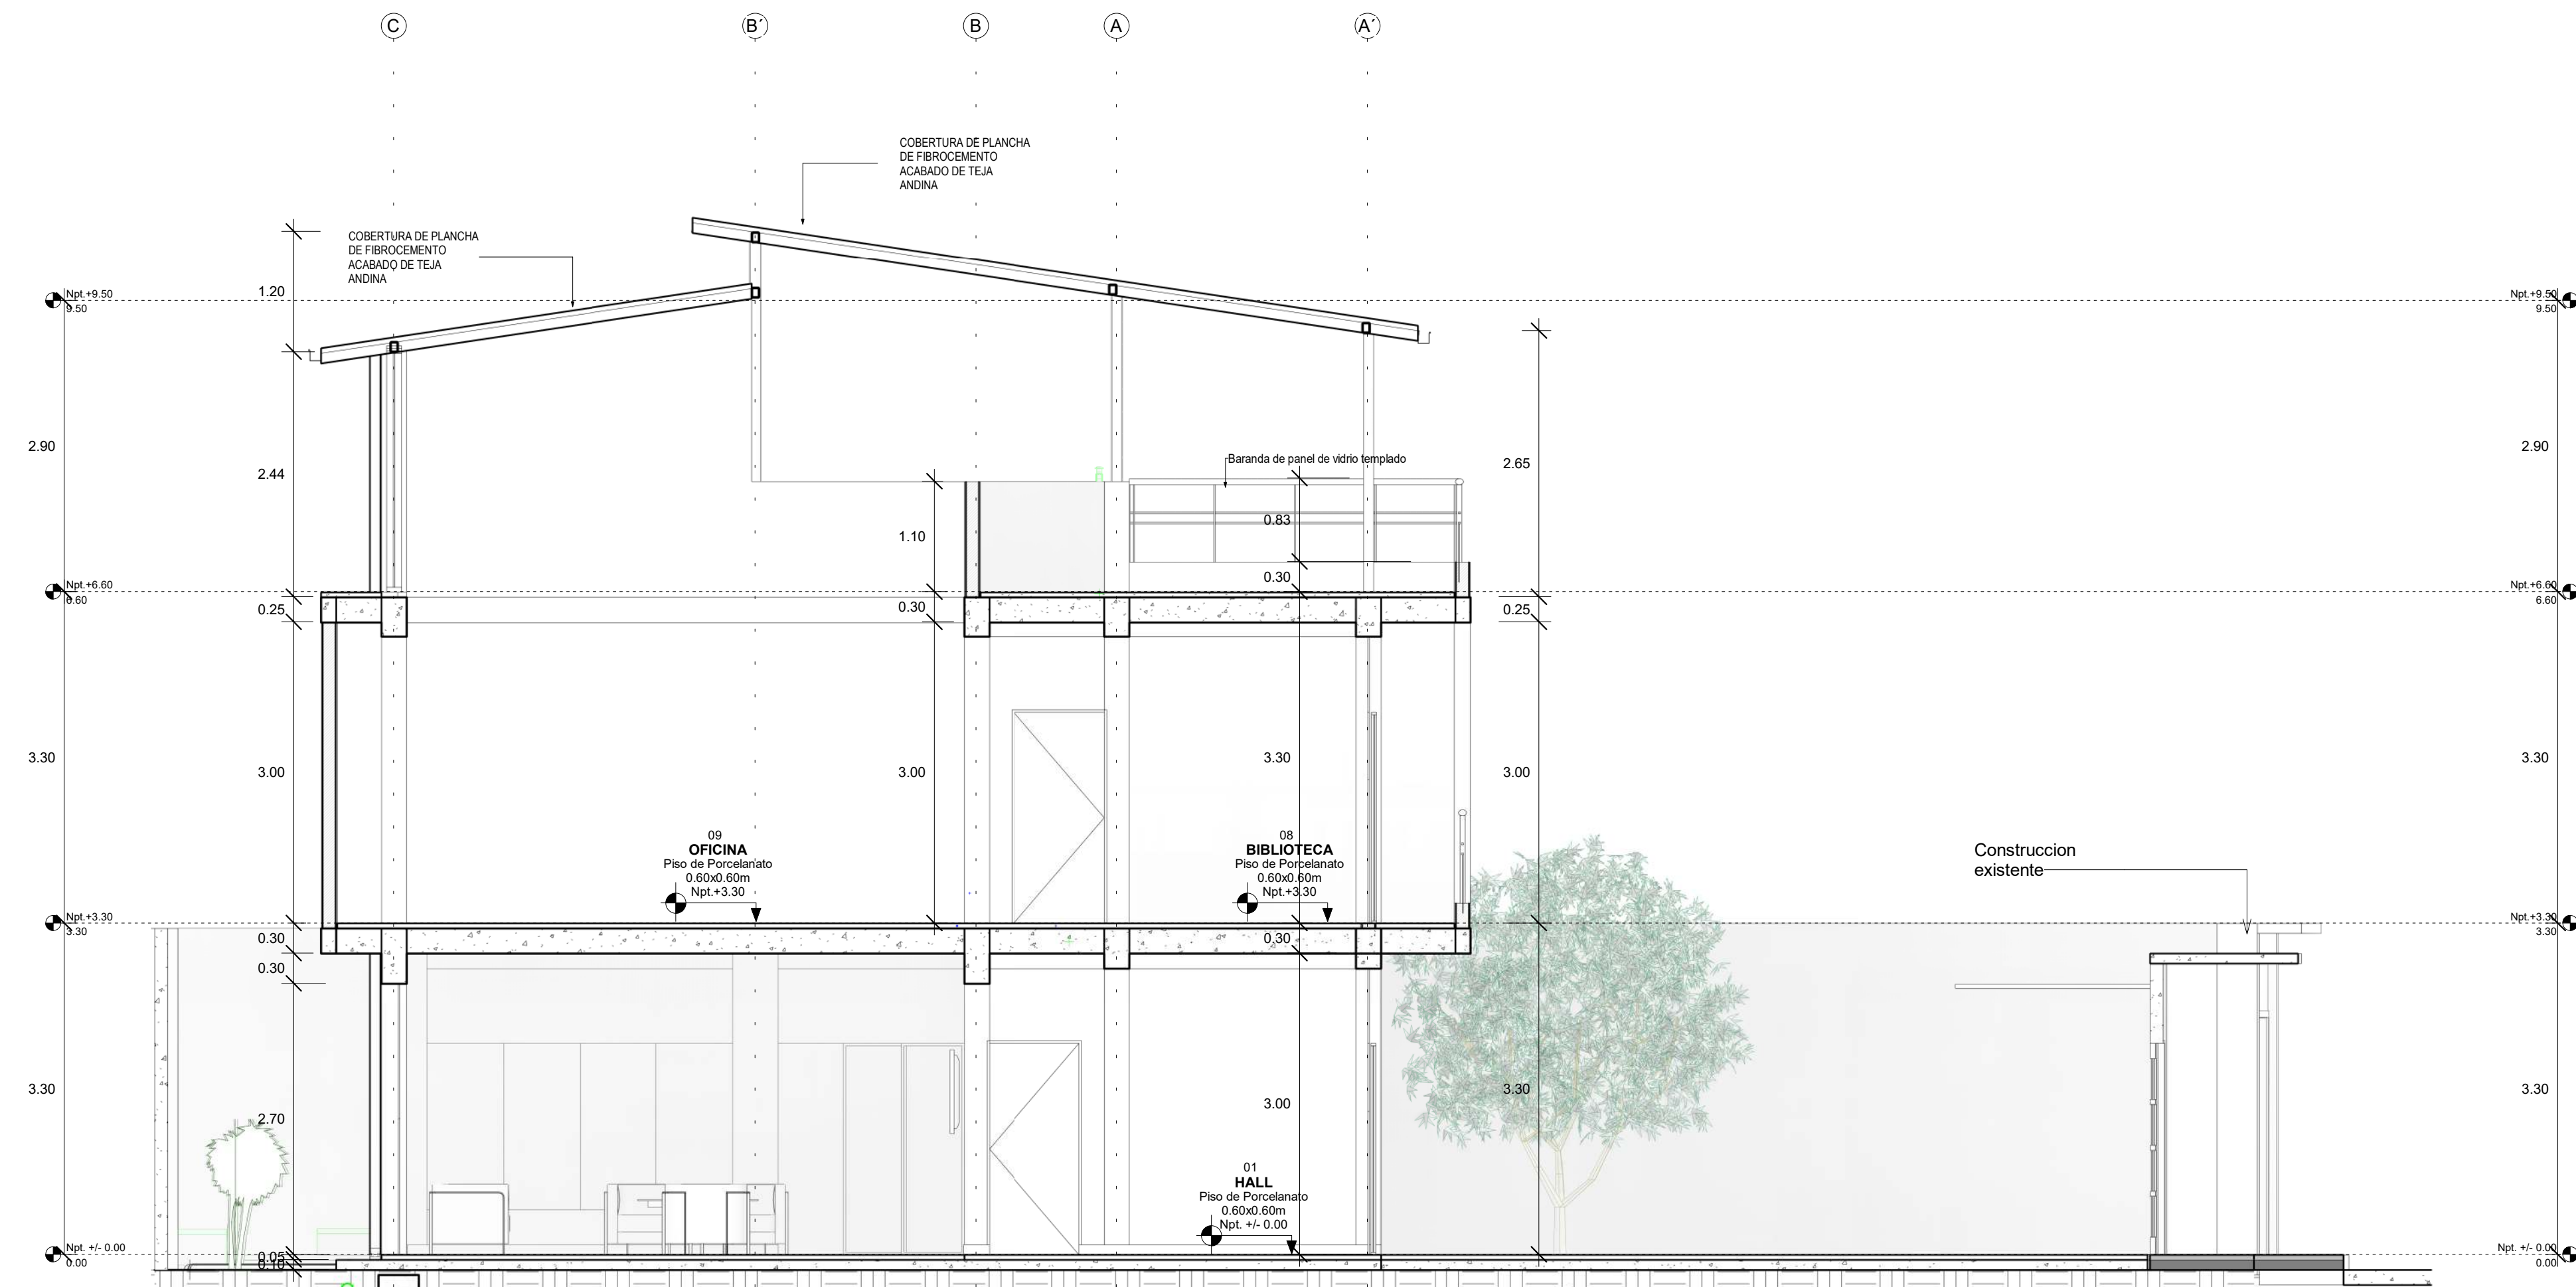


A CORTE LONGITUDINAL A-A
A-04 1:50

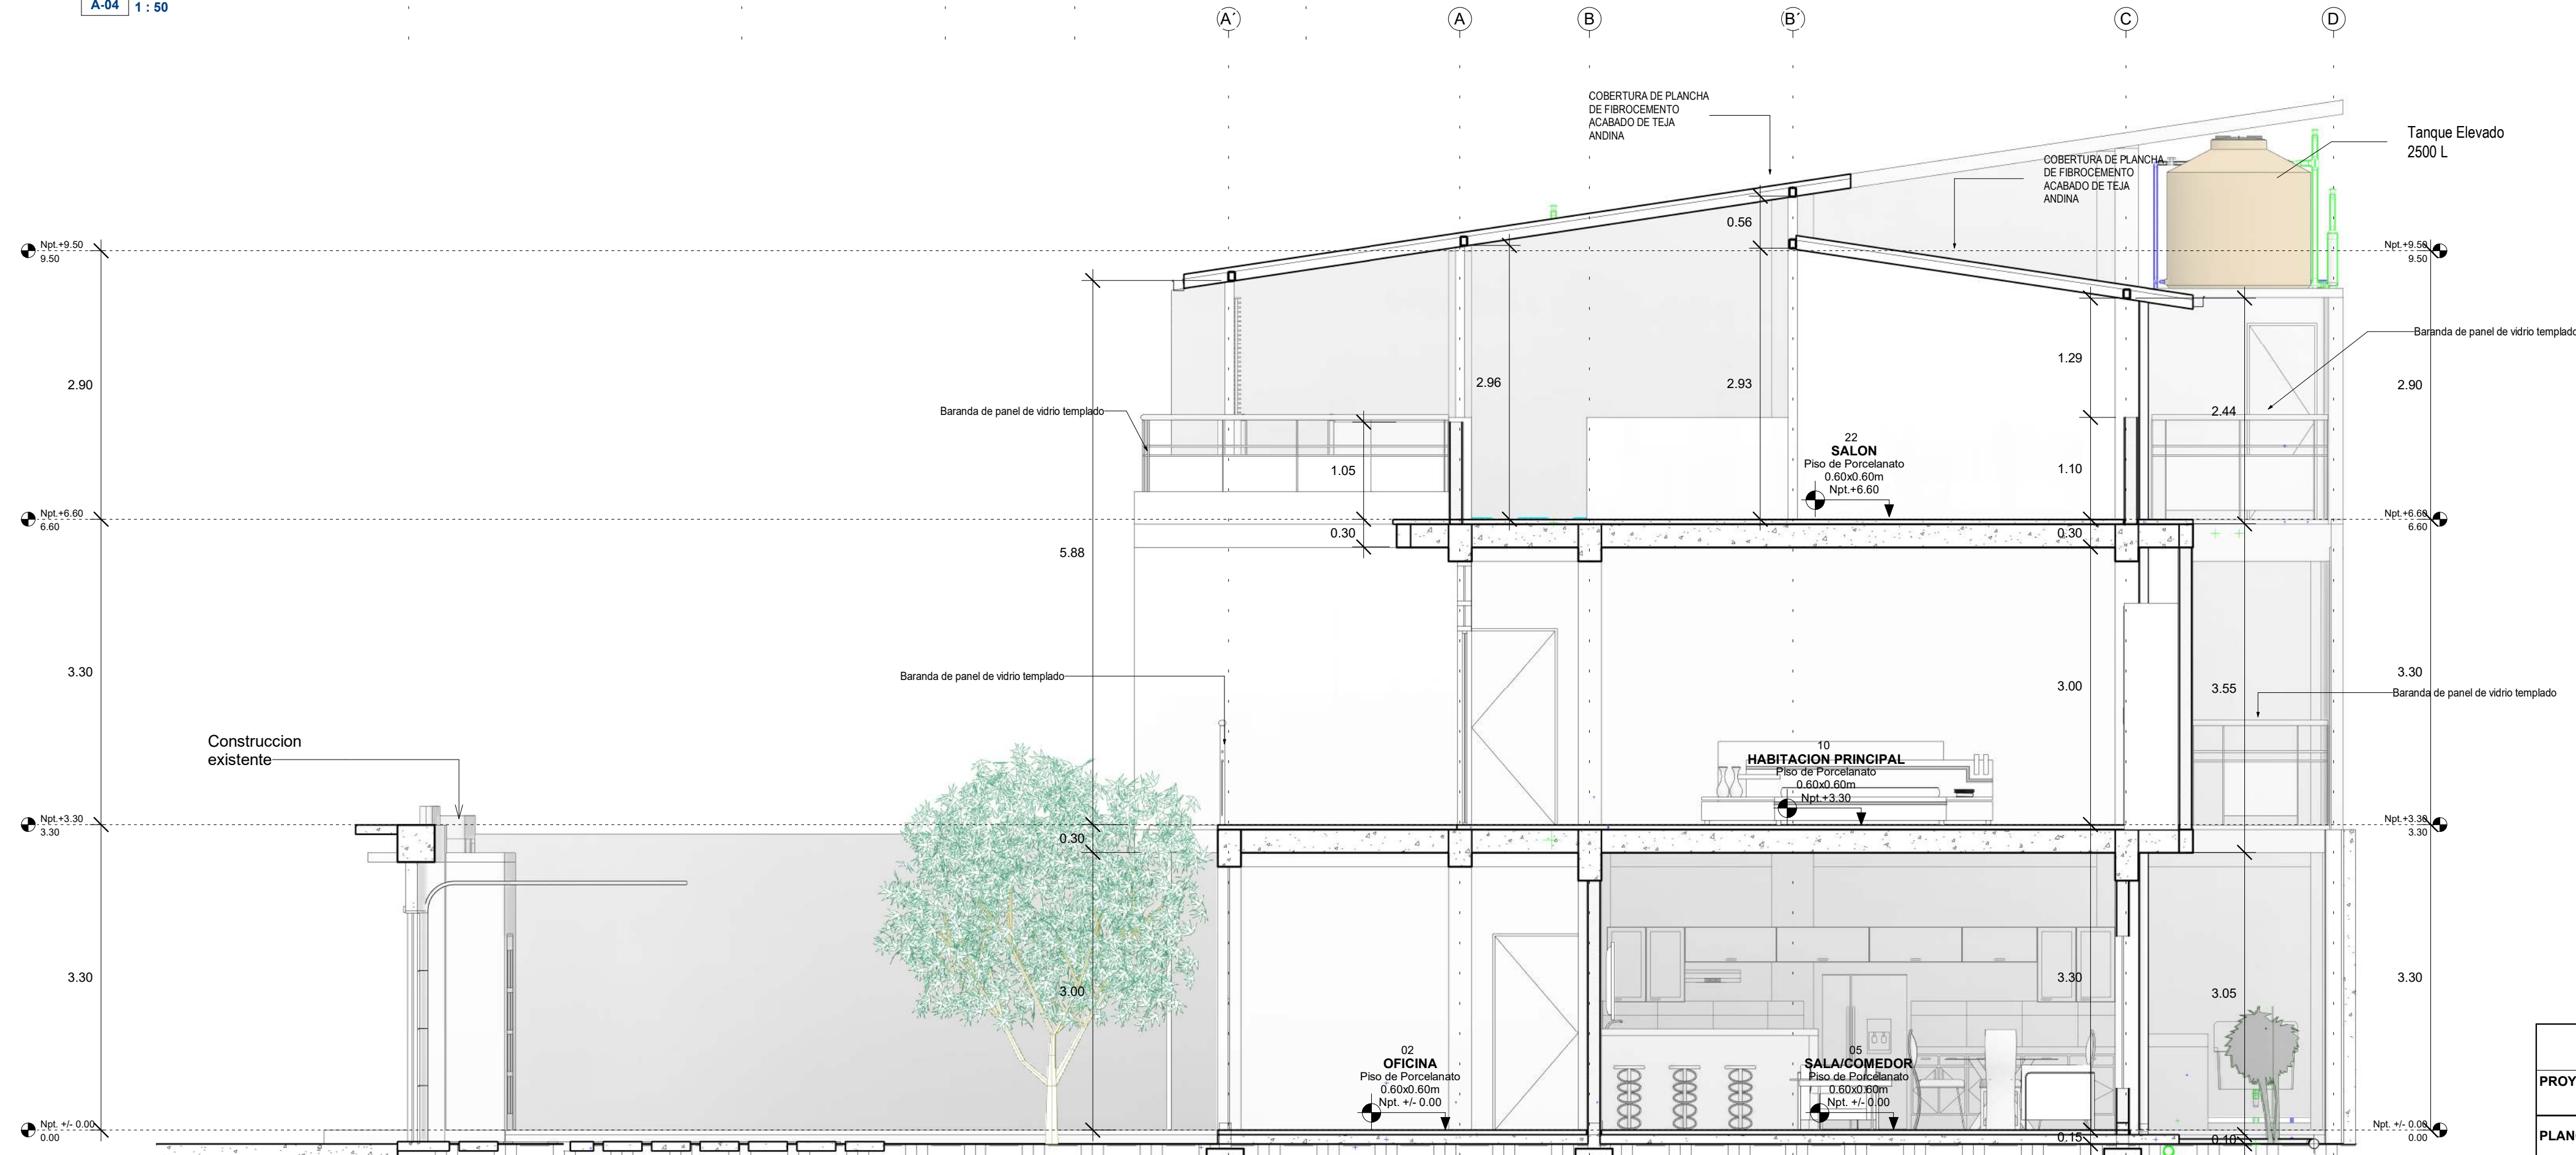


B CORTE LONGITUDINAL B-B
A-04 1:50


EDIFICIO UNIFAMILIAR				
PROYECTO: VIVIENDA UNIFAMILIAR				
PLANO: CORTES		FECHA: NOV-2021	DIBUJO Y MODELADO BIM: 	

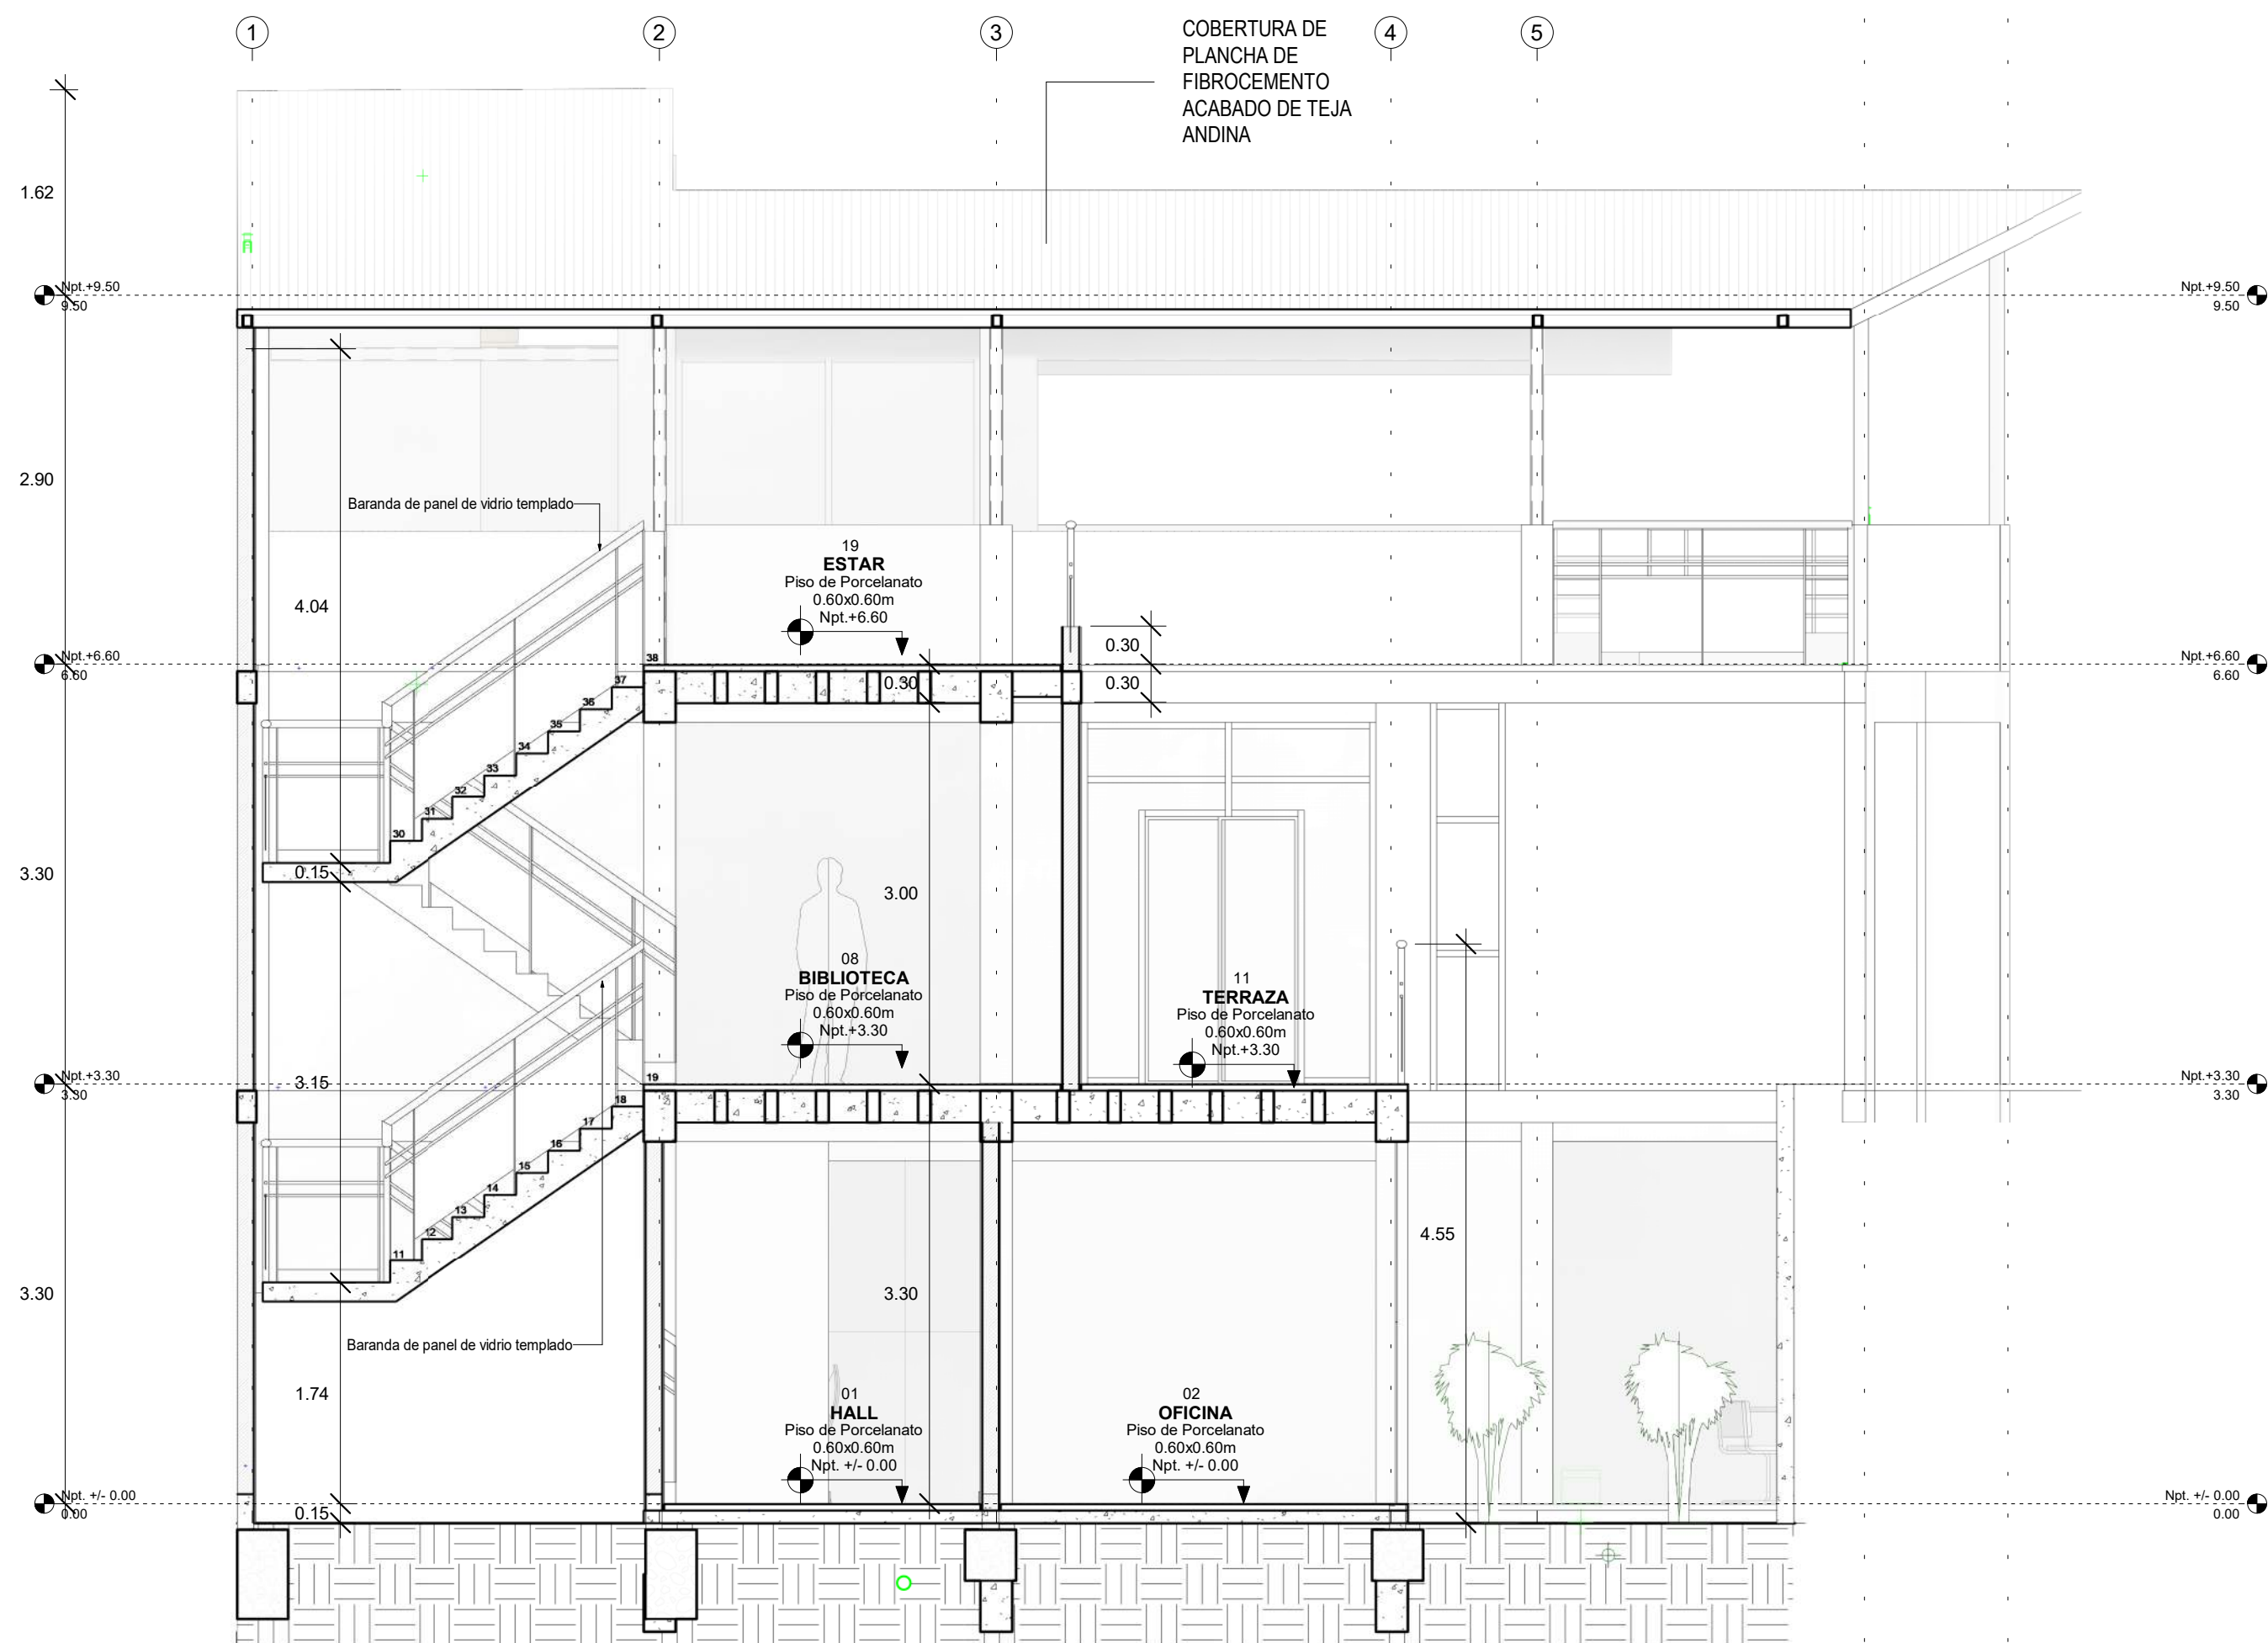

D CORTE TRANSVERSAL D-D
A-05 1 : 50

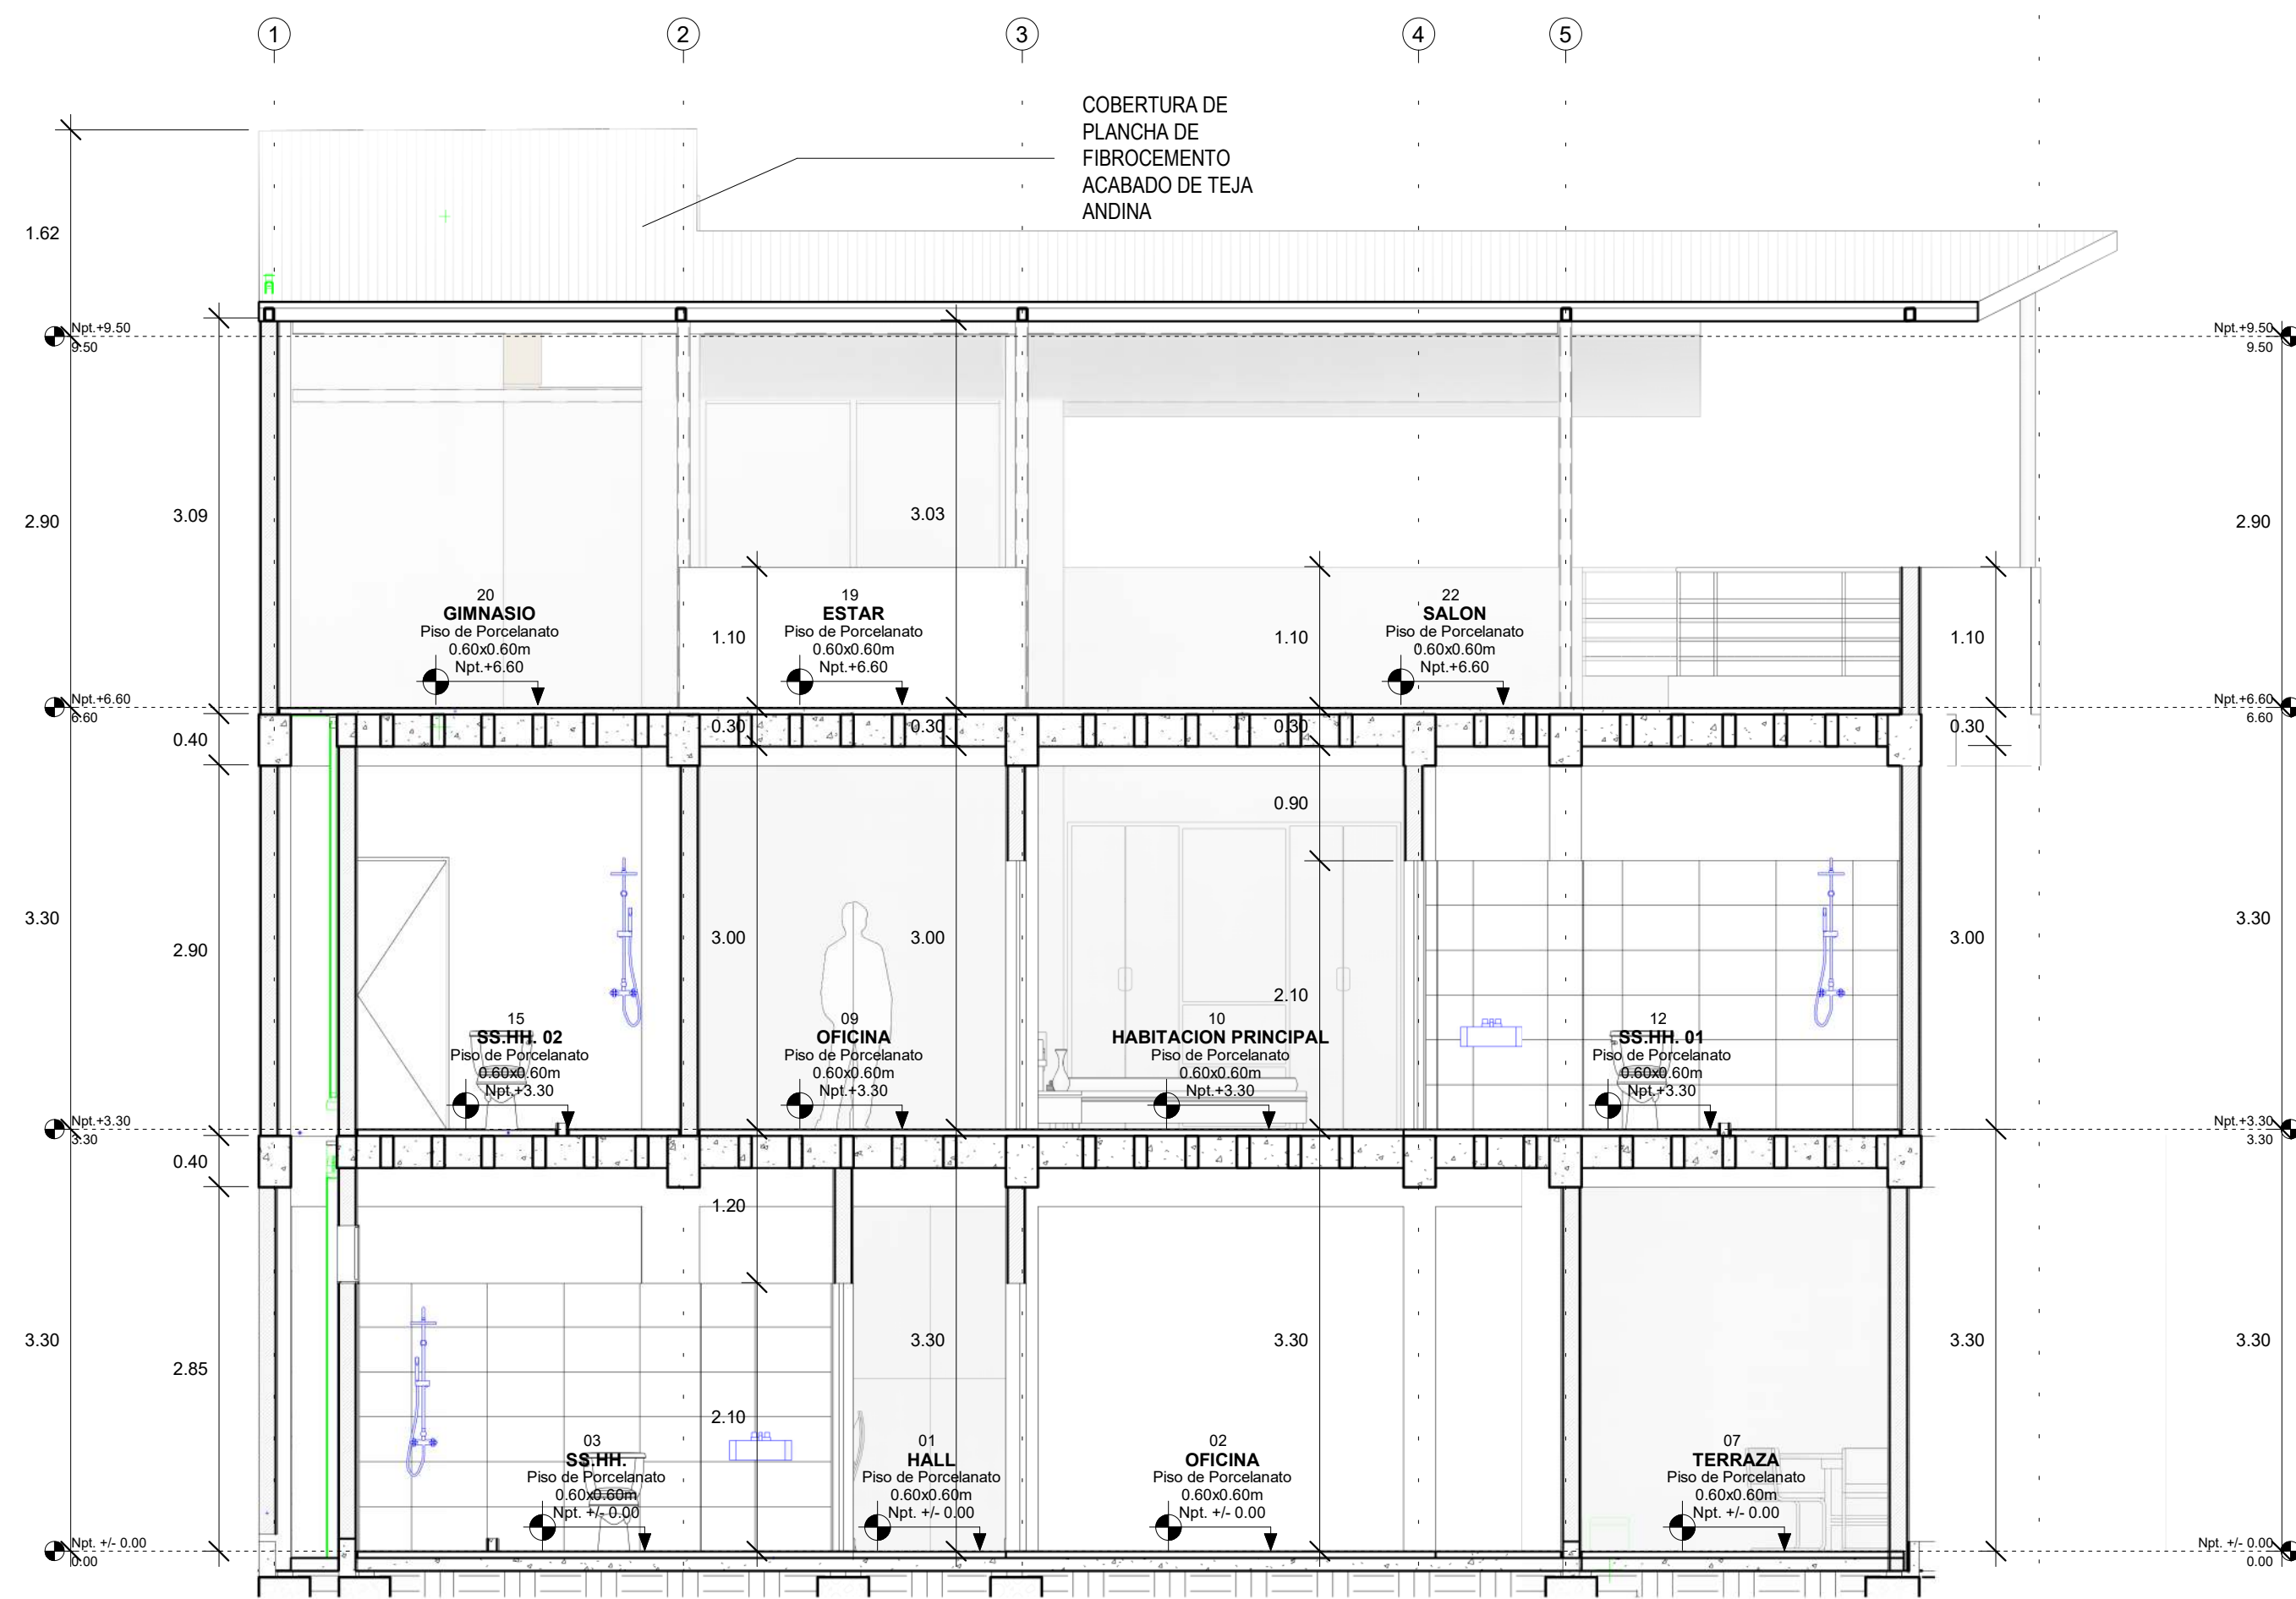

E CORTE TRANSVERSAL E-E
A-05 1 : 50

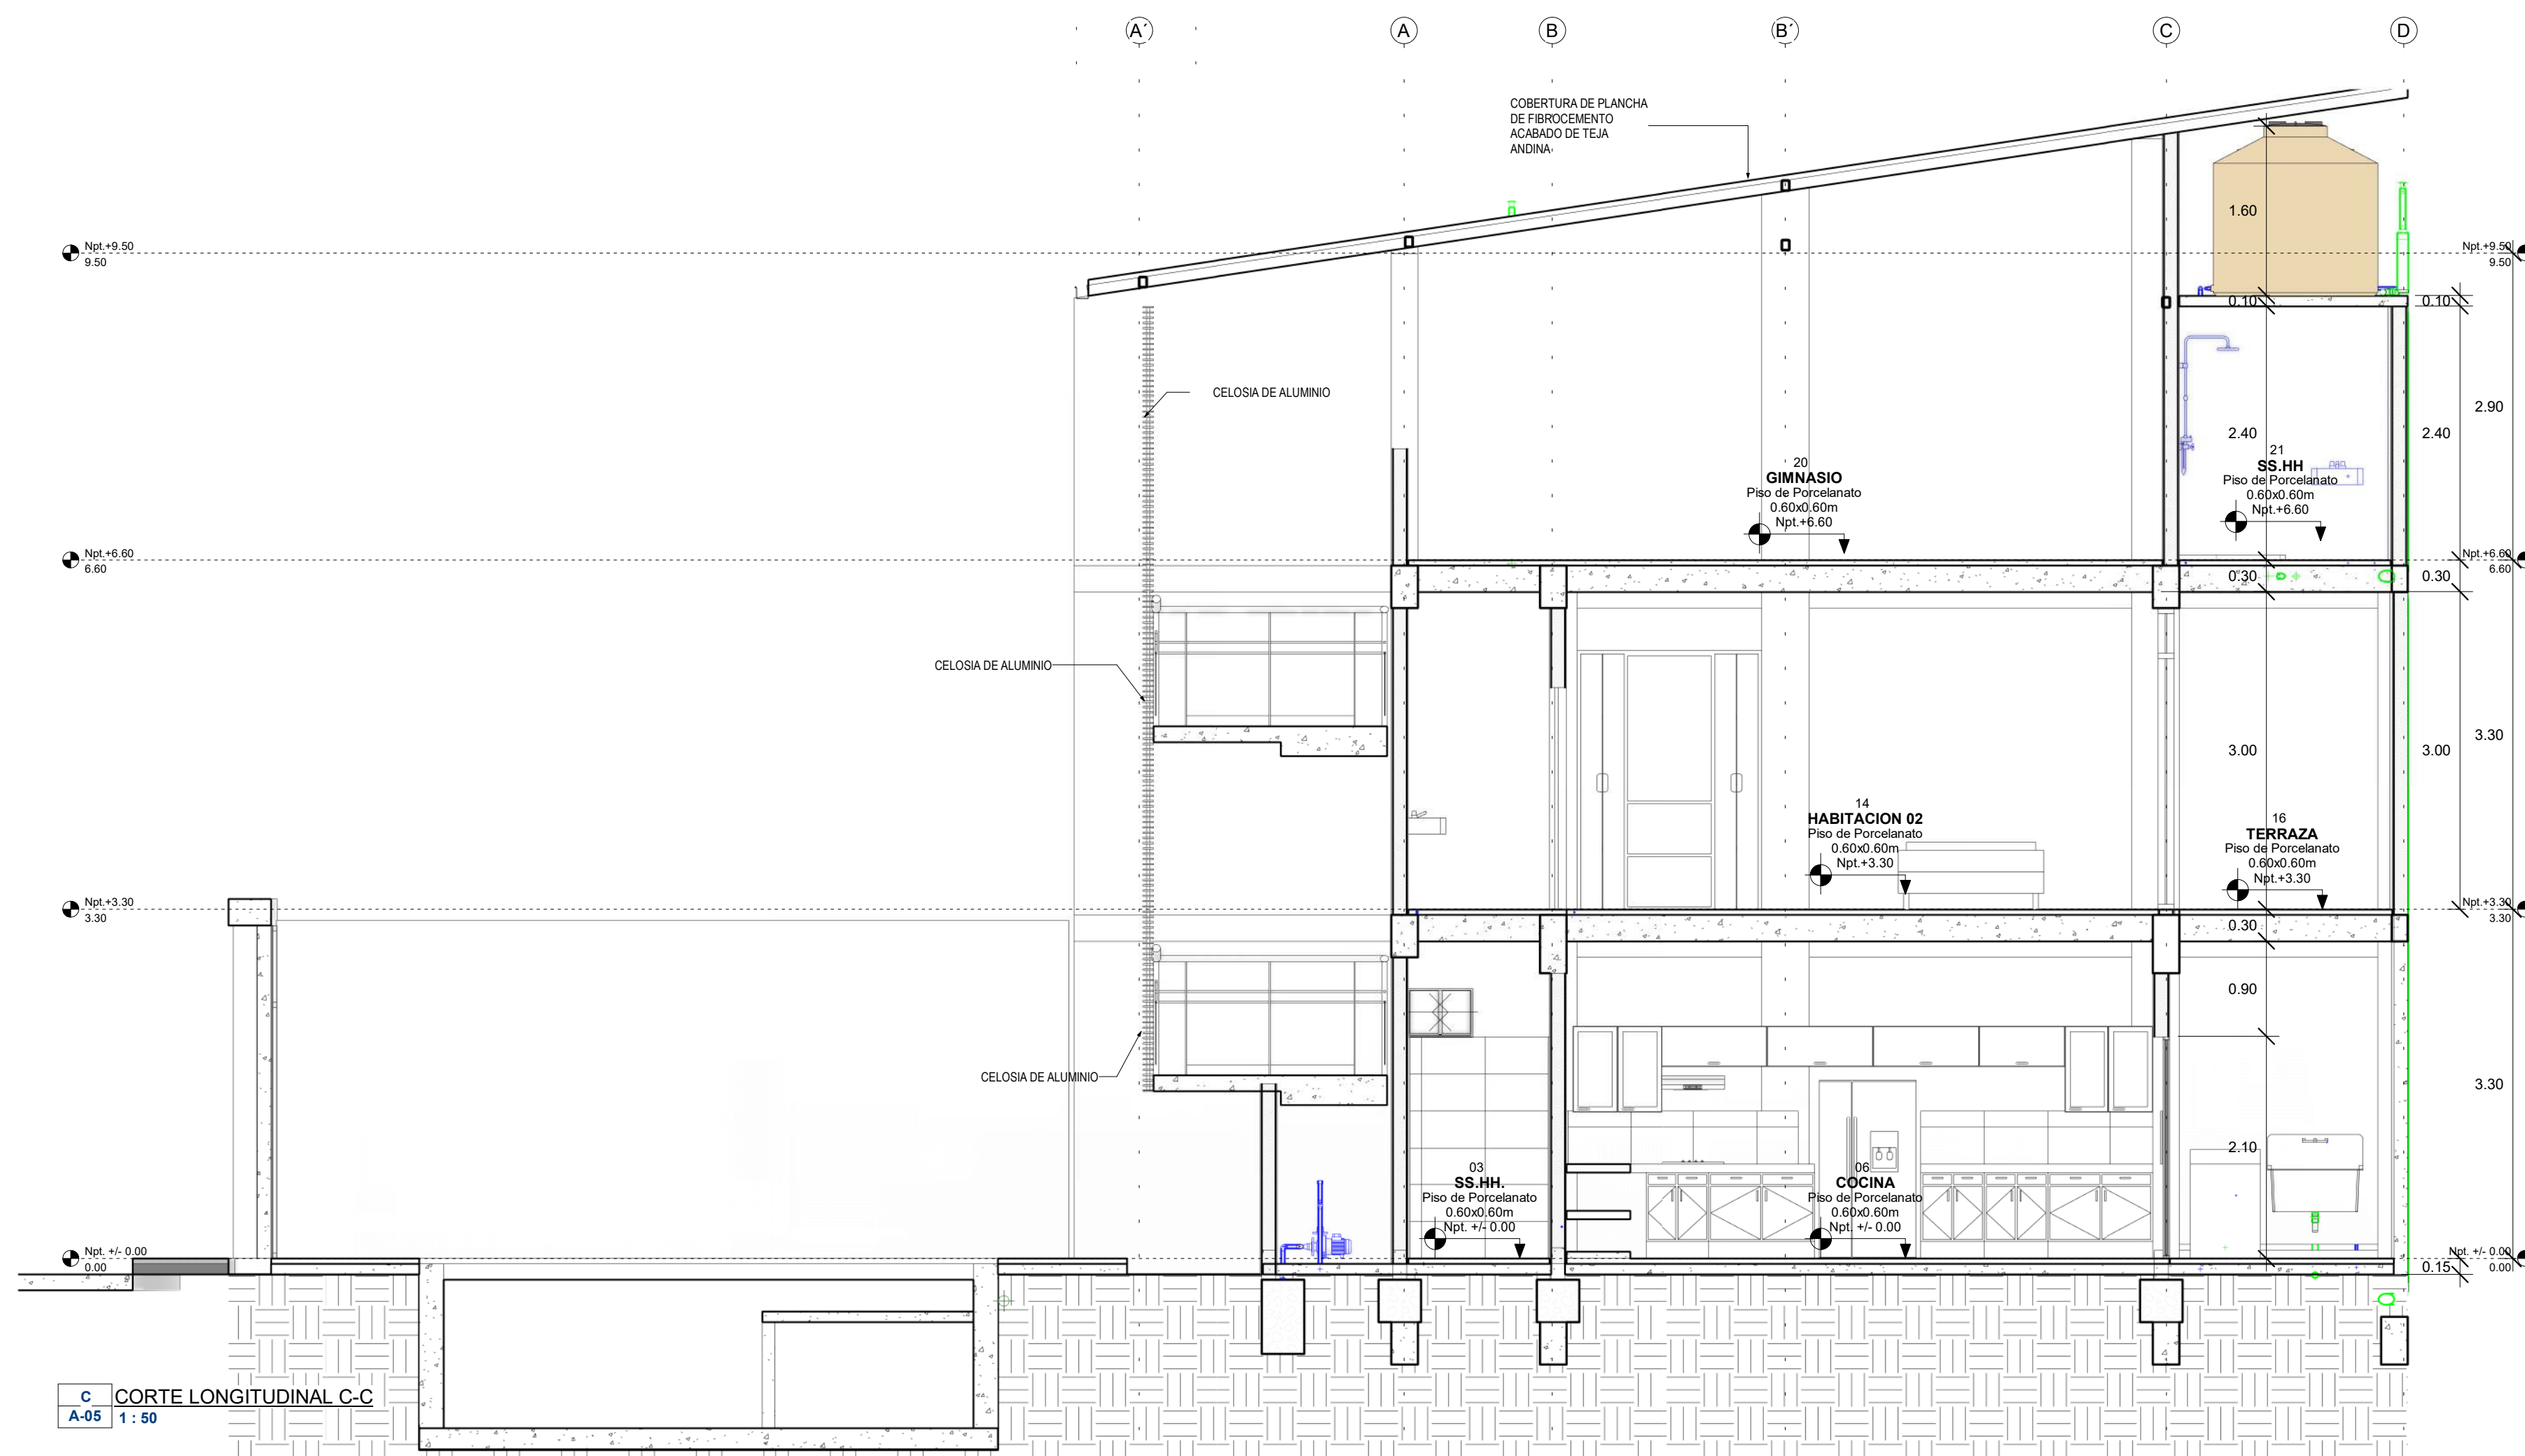

C CORTE LONGITUDINAL C-C
A-05 1 : 50

EDIFICIO UNIFAMILIAR

PROYECTO: VIVIENDA UNIFAMILIAR

PLANO: CORTES

ESPECIALIDAD: ARQUITECTURA

DISEÑO: NELSON DAZA DONAIRES

UBICACION: Jr. Achual C-01, Barrio de Suchiche

FECHA: NOV-2021


ESC: 1 : 50

PLANO:


A-05

DIBUJO Y
MODELADO
BIM:


Nelson Daza
Donaires

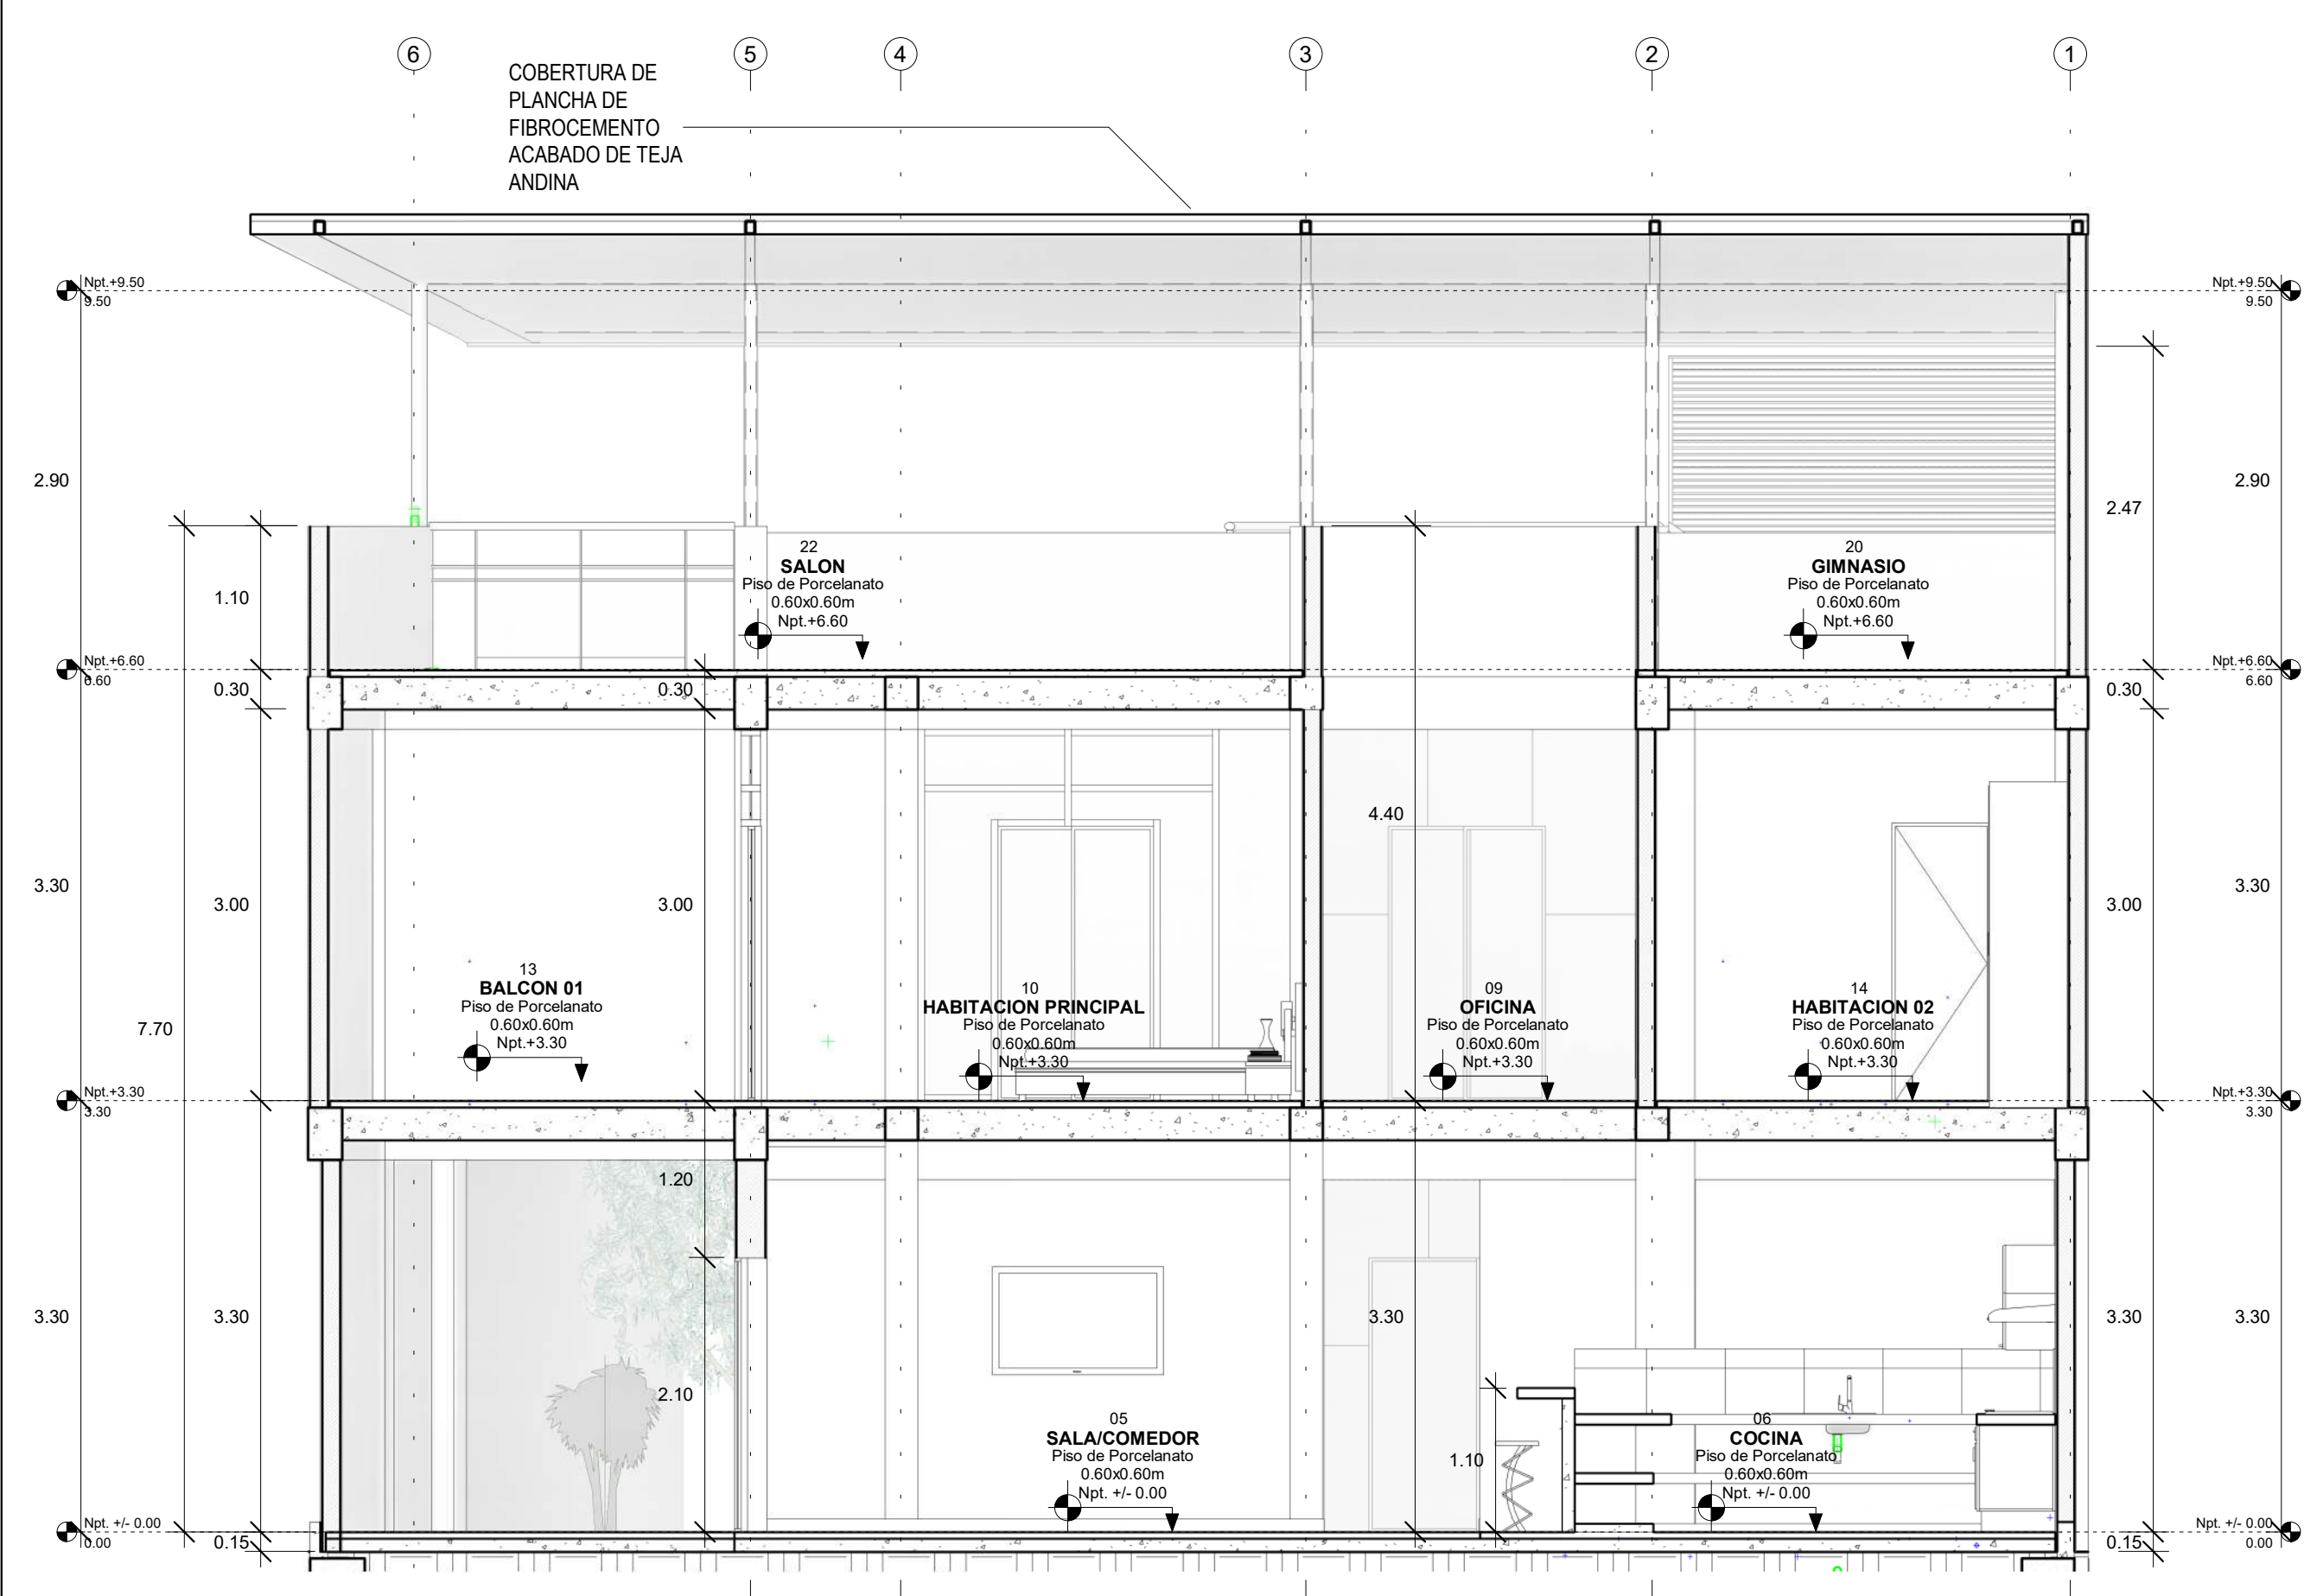

F CORTE TRANSVERSAL F-F
A-06 1:50


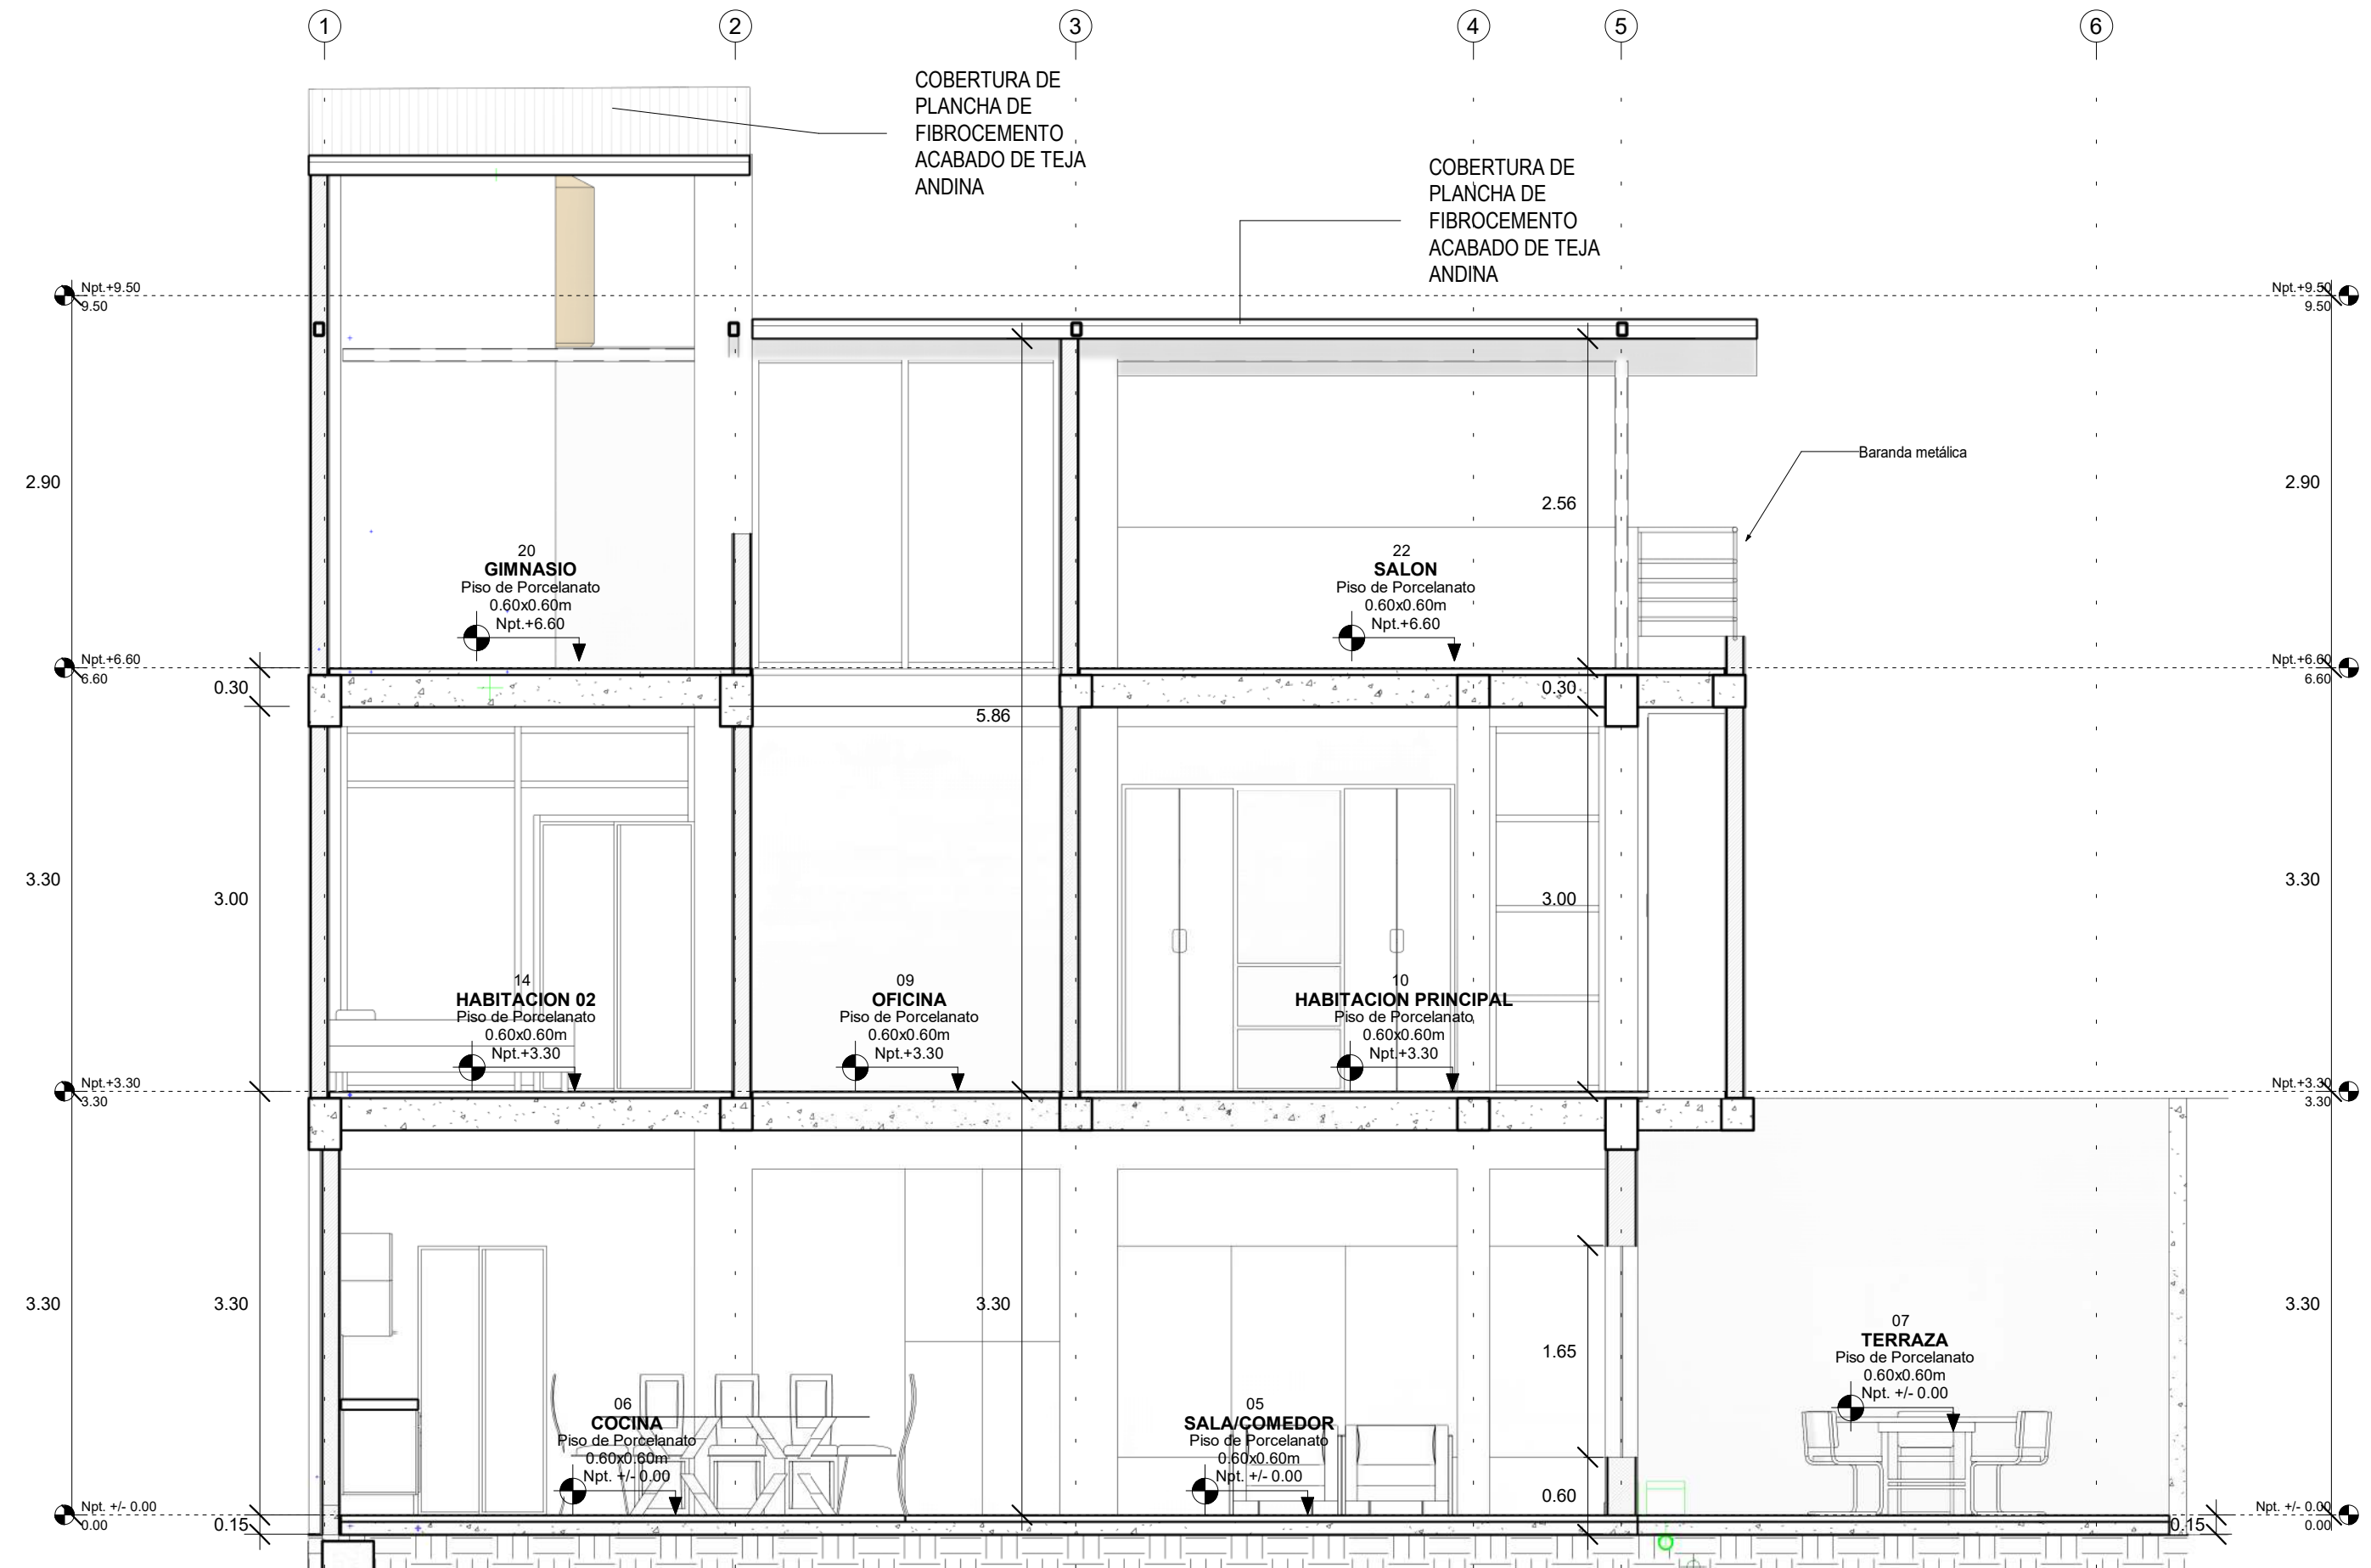


G CORTE TRANSVERSAL G-G
A-06 1:50

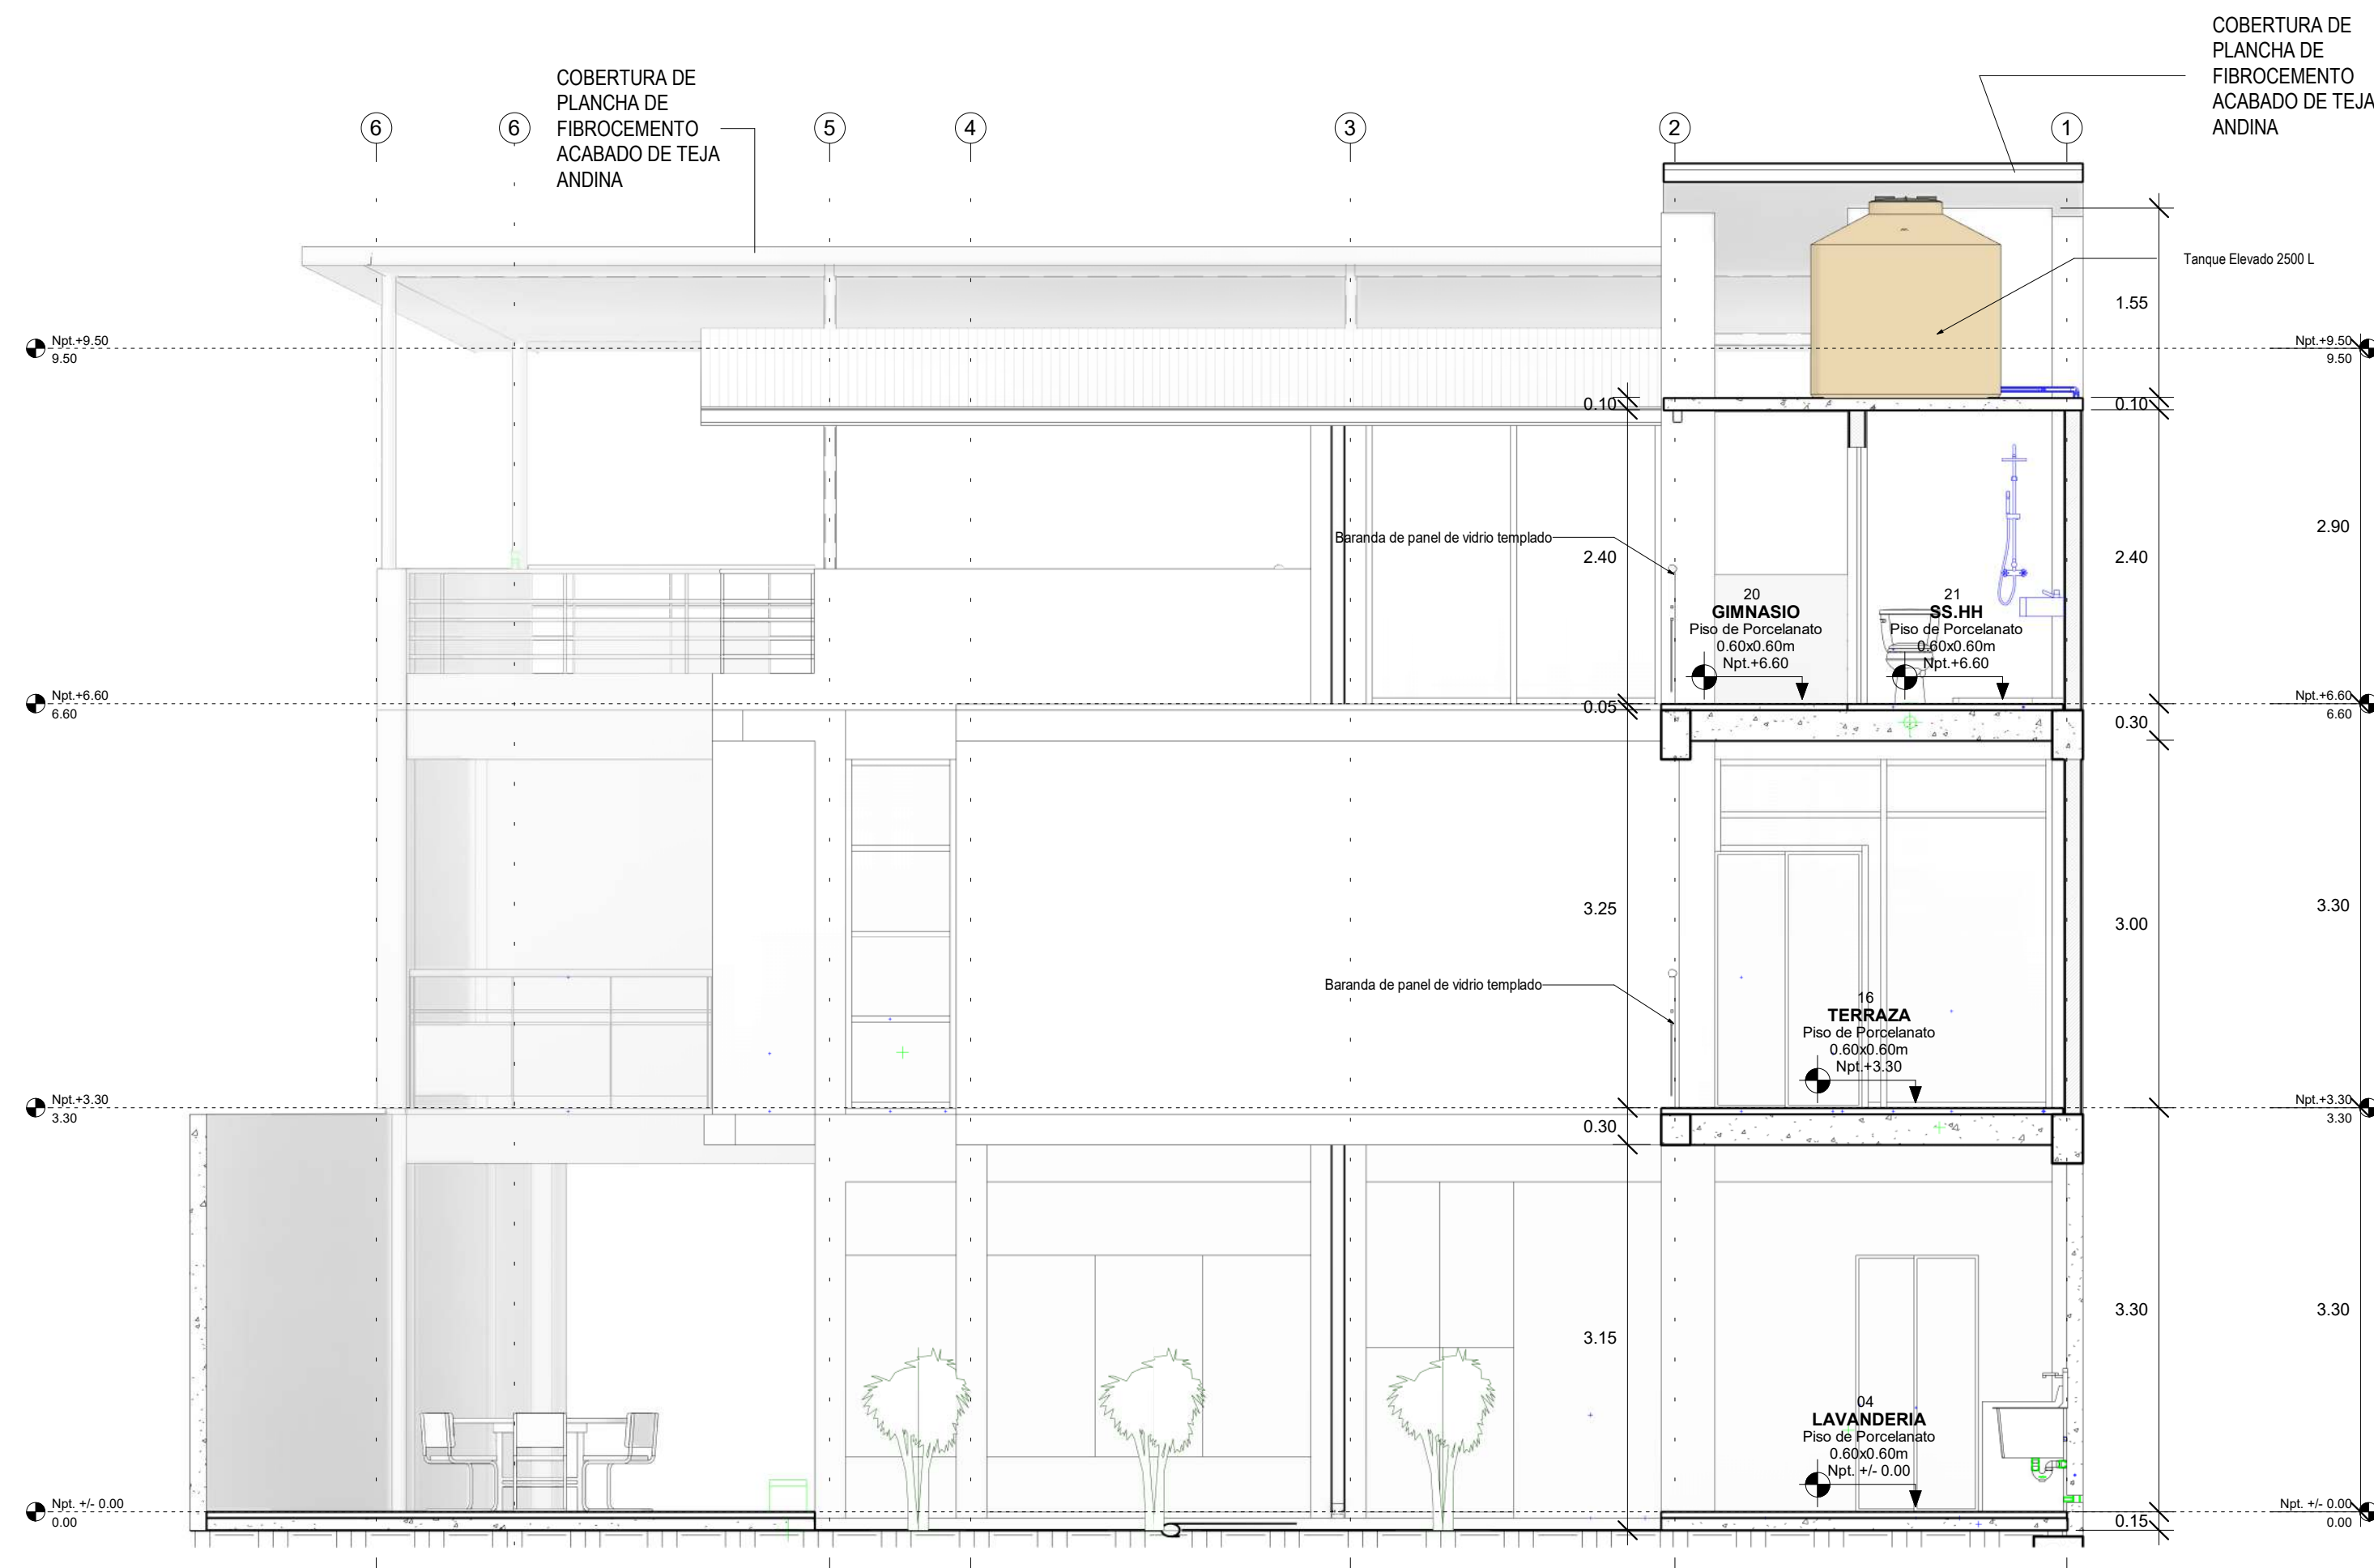

H CORTE TRANSVERSAL H-H
A-06 1:50

EDIFICIO UNIFAMILIAR				
PROYECTO: VIVIENDA UNIFAMILIAR				
PLANO: CORTES	FECHA: NOV-2021	DIBUJO Y MODELADO BIM: A-06 Nelson Daza Donaires		
ESPECIALIDAD: ARQUITECTURA	ESC: 1:50			
DISEÑO: NELSON DAZA DONAIRES	PLANO:			
UBICACION: Jr. Actual C-01, Barrio de Suchiche				
Districto: TARAPOTO	Provincia: SAN MARTIN	Región: SAN MARTIN		

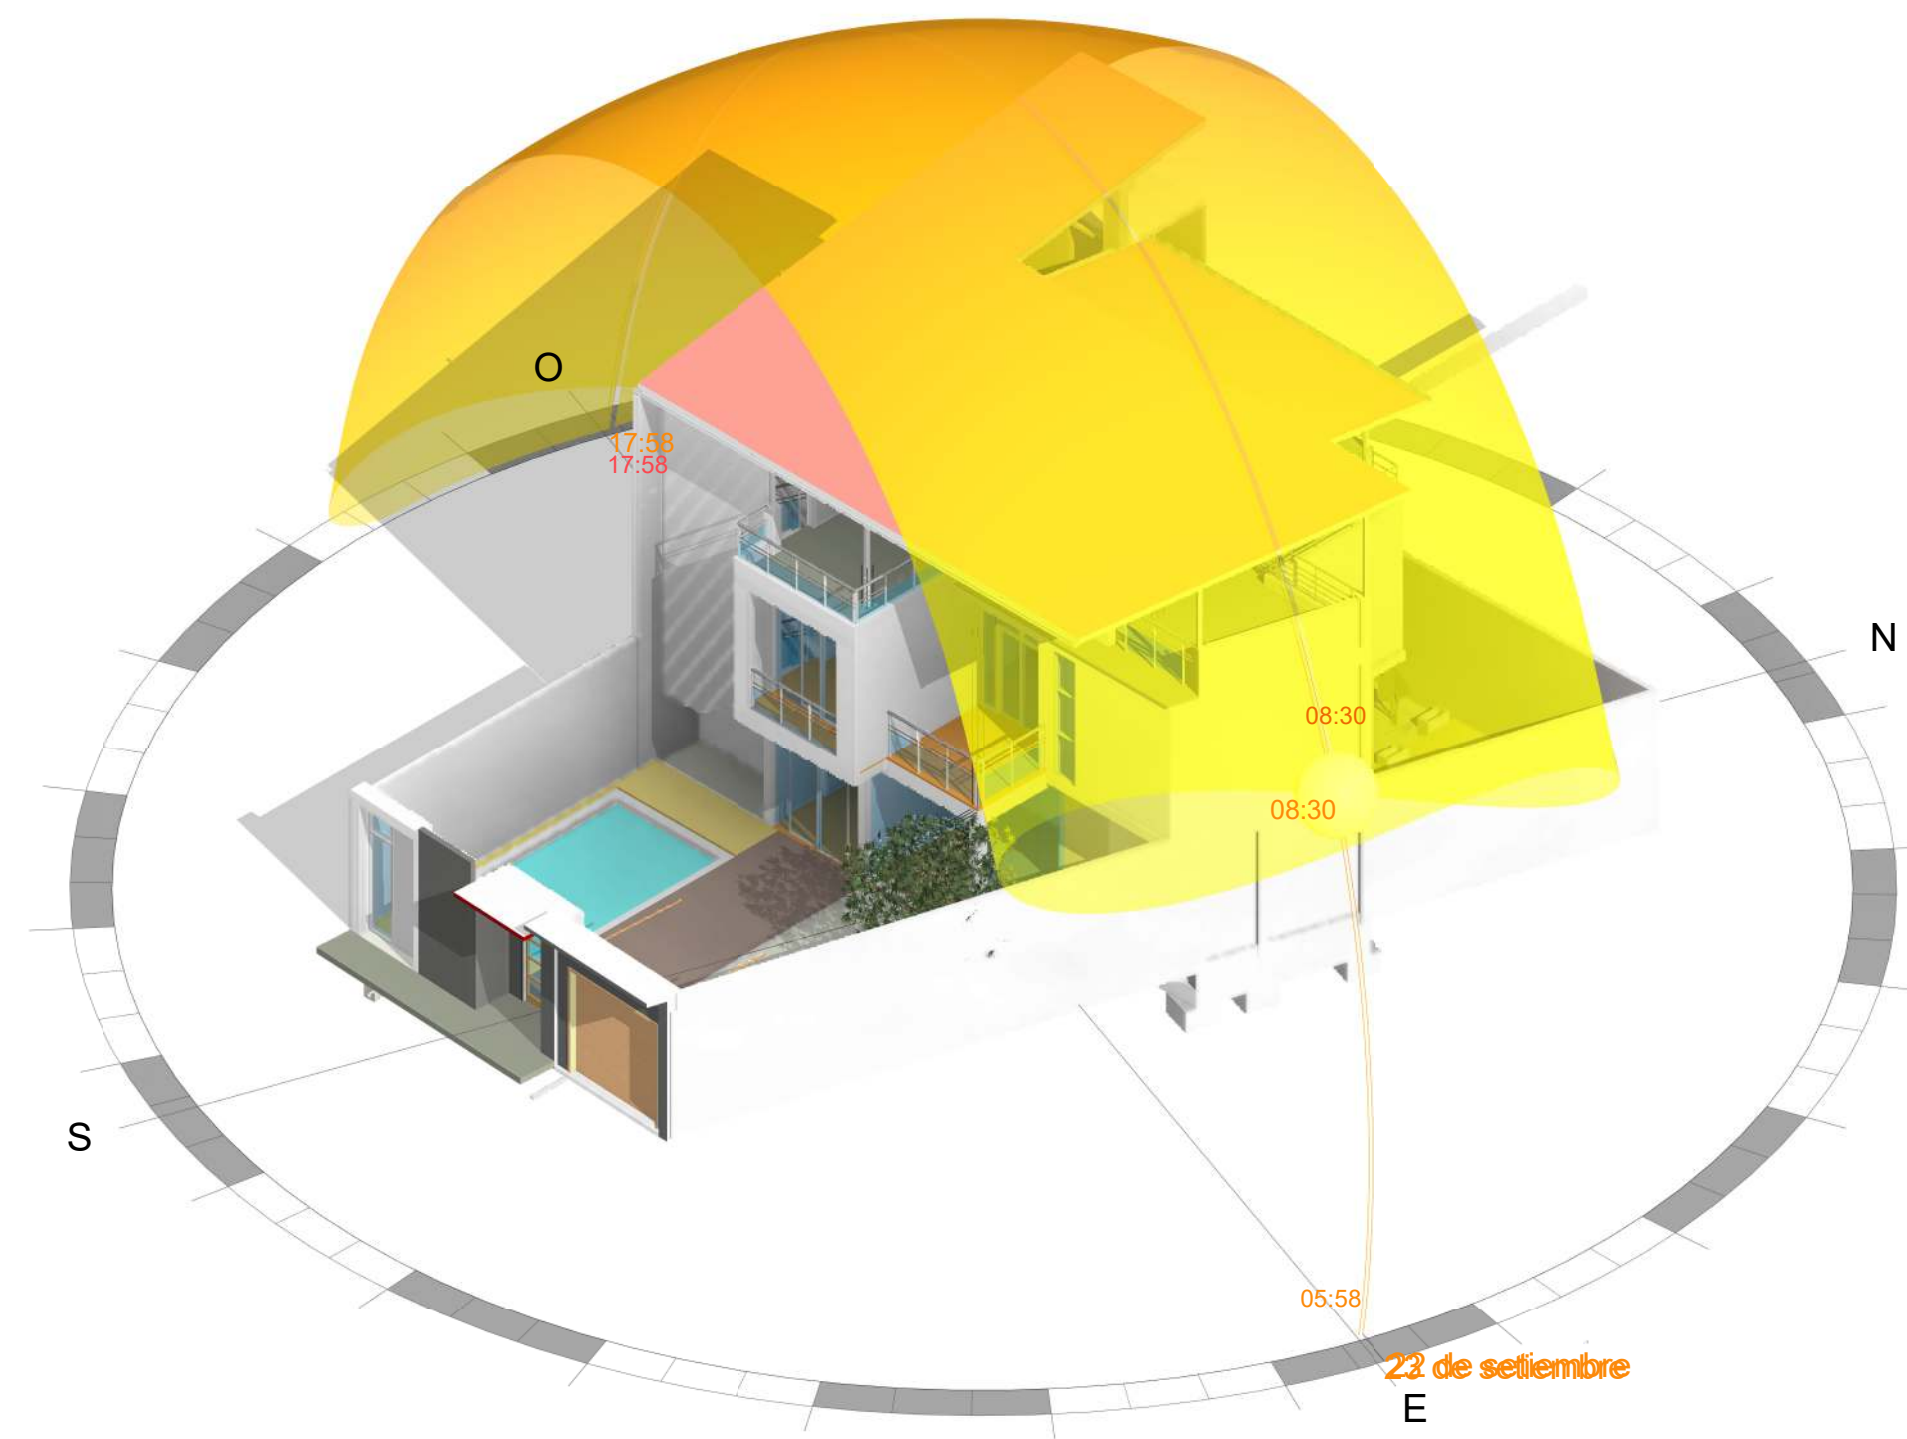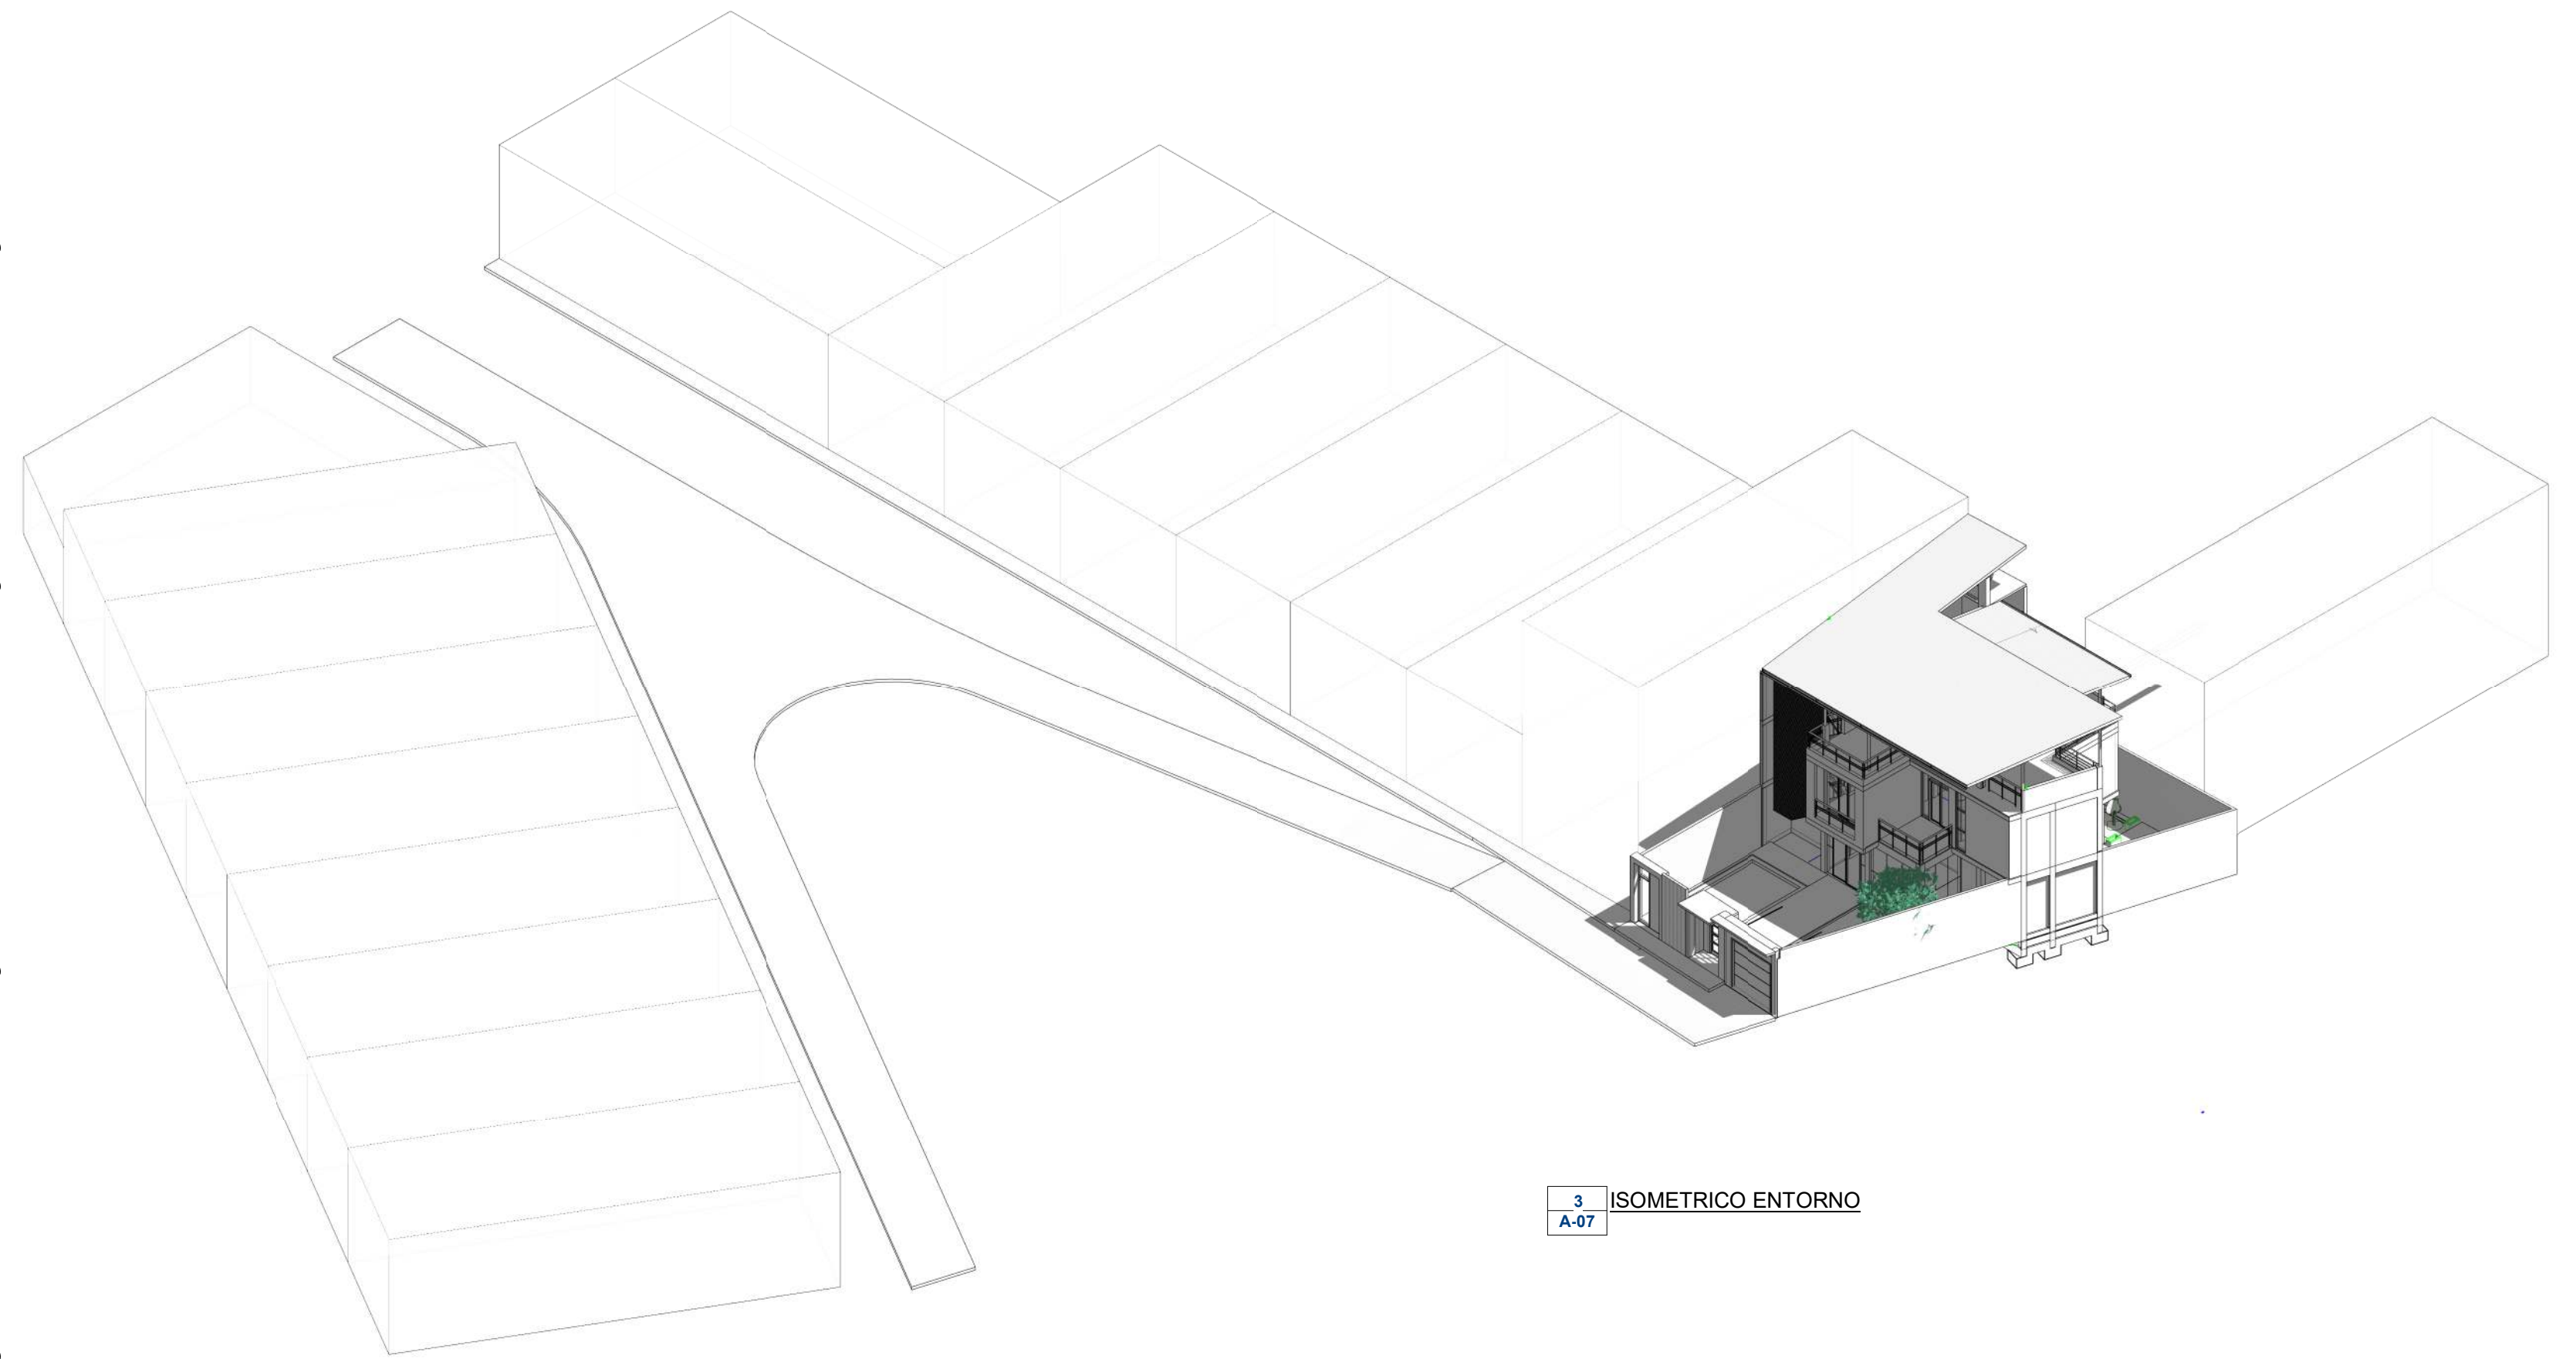

EDIFICIO UNIFAMILIAR				
PROYECTO:		VIVIENDA UNIFAMILIAR		
PLANO:	ELEVACIONES		FECHA:	NOV-2021
ESPECIALIDAD:	ARQUITECTURA		ESC:	1 : 50
DISEÑO:	NELSON DAZA DONAIRES		PLANO:	A-07
UBICACION:	Jr. Achual C-01, Barrio de Suchiche			
Districto:	TARAPOTO	Provincia:	SAN MARTIN	
		Región:	SAN MARTIN	Nelson Daza Donaires